




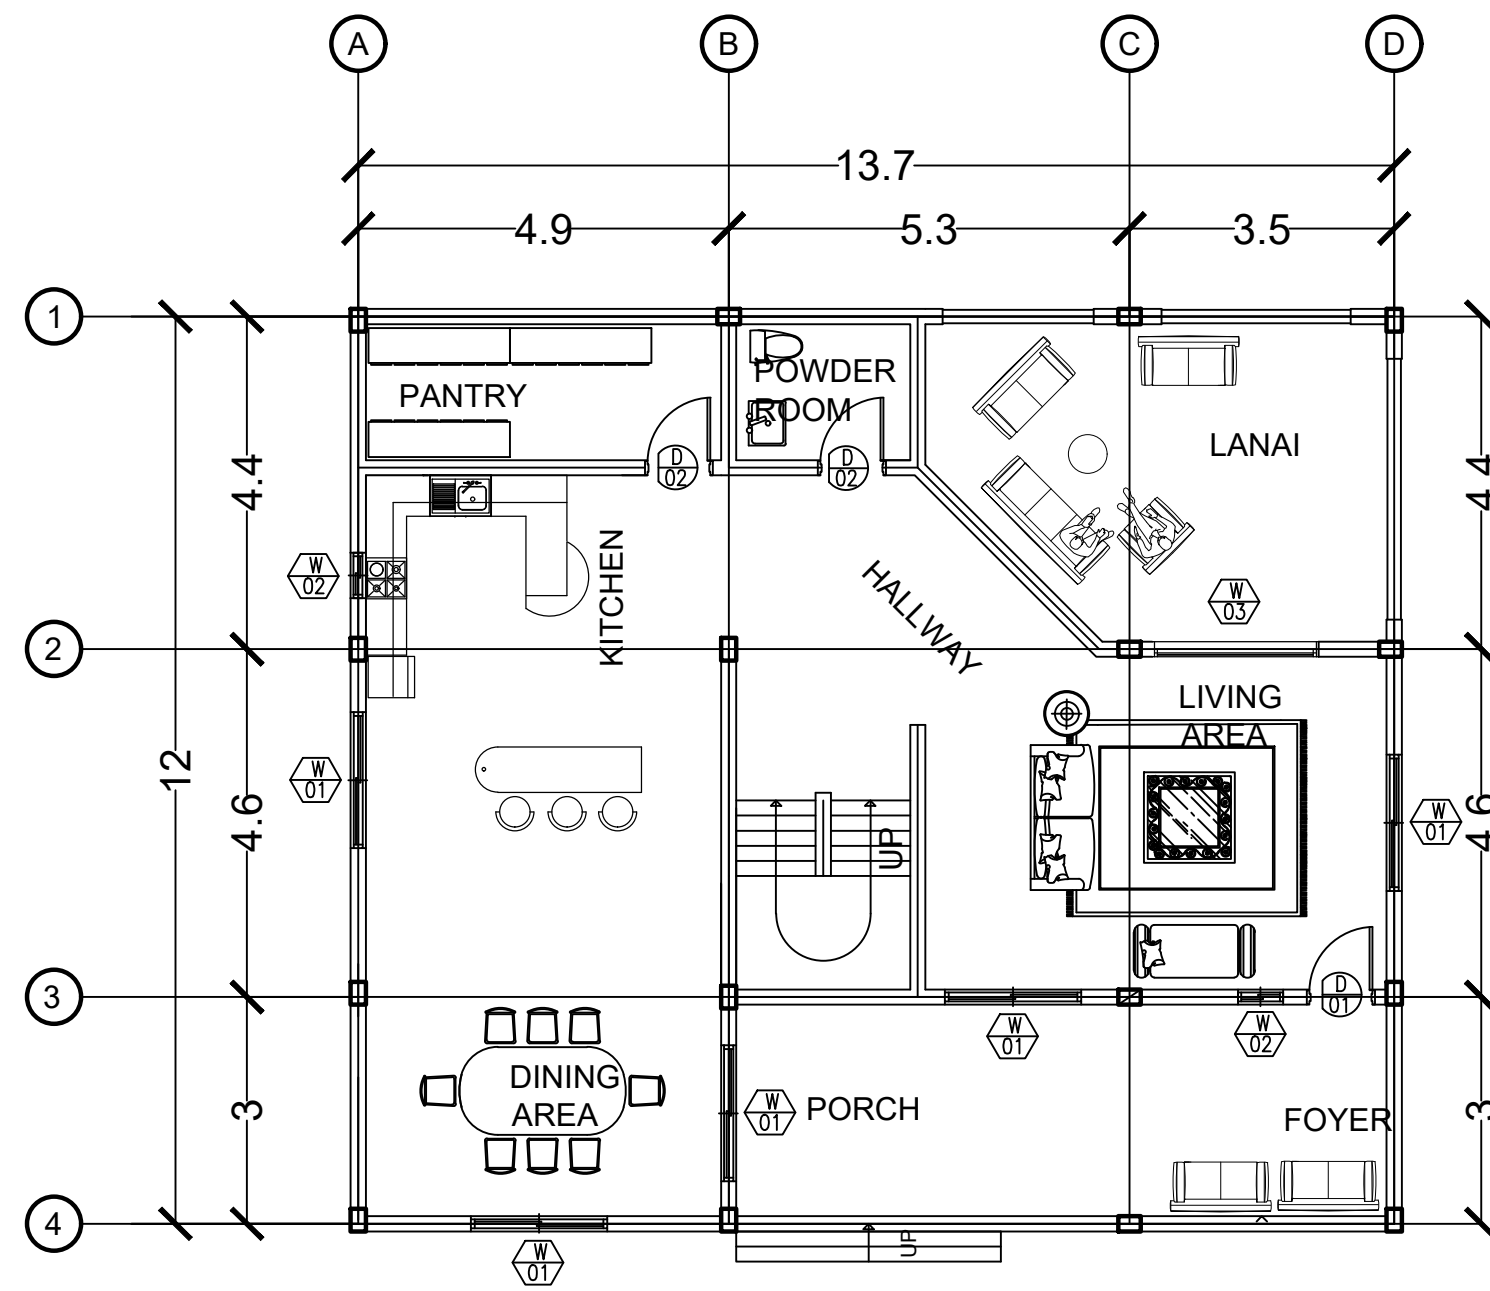


GROUND FLOOR PLAN
SCALE 1:100 MTRS.

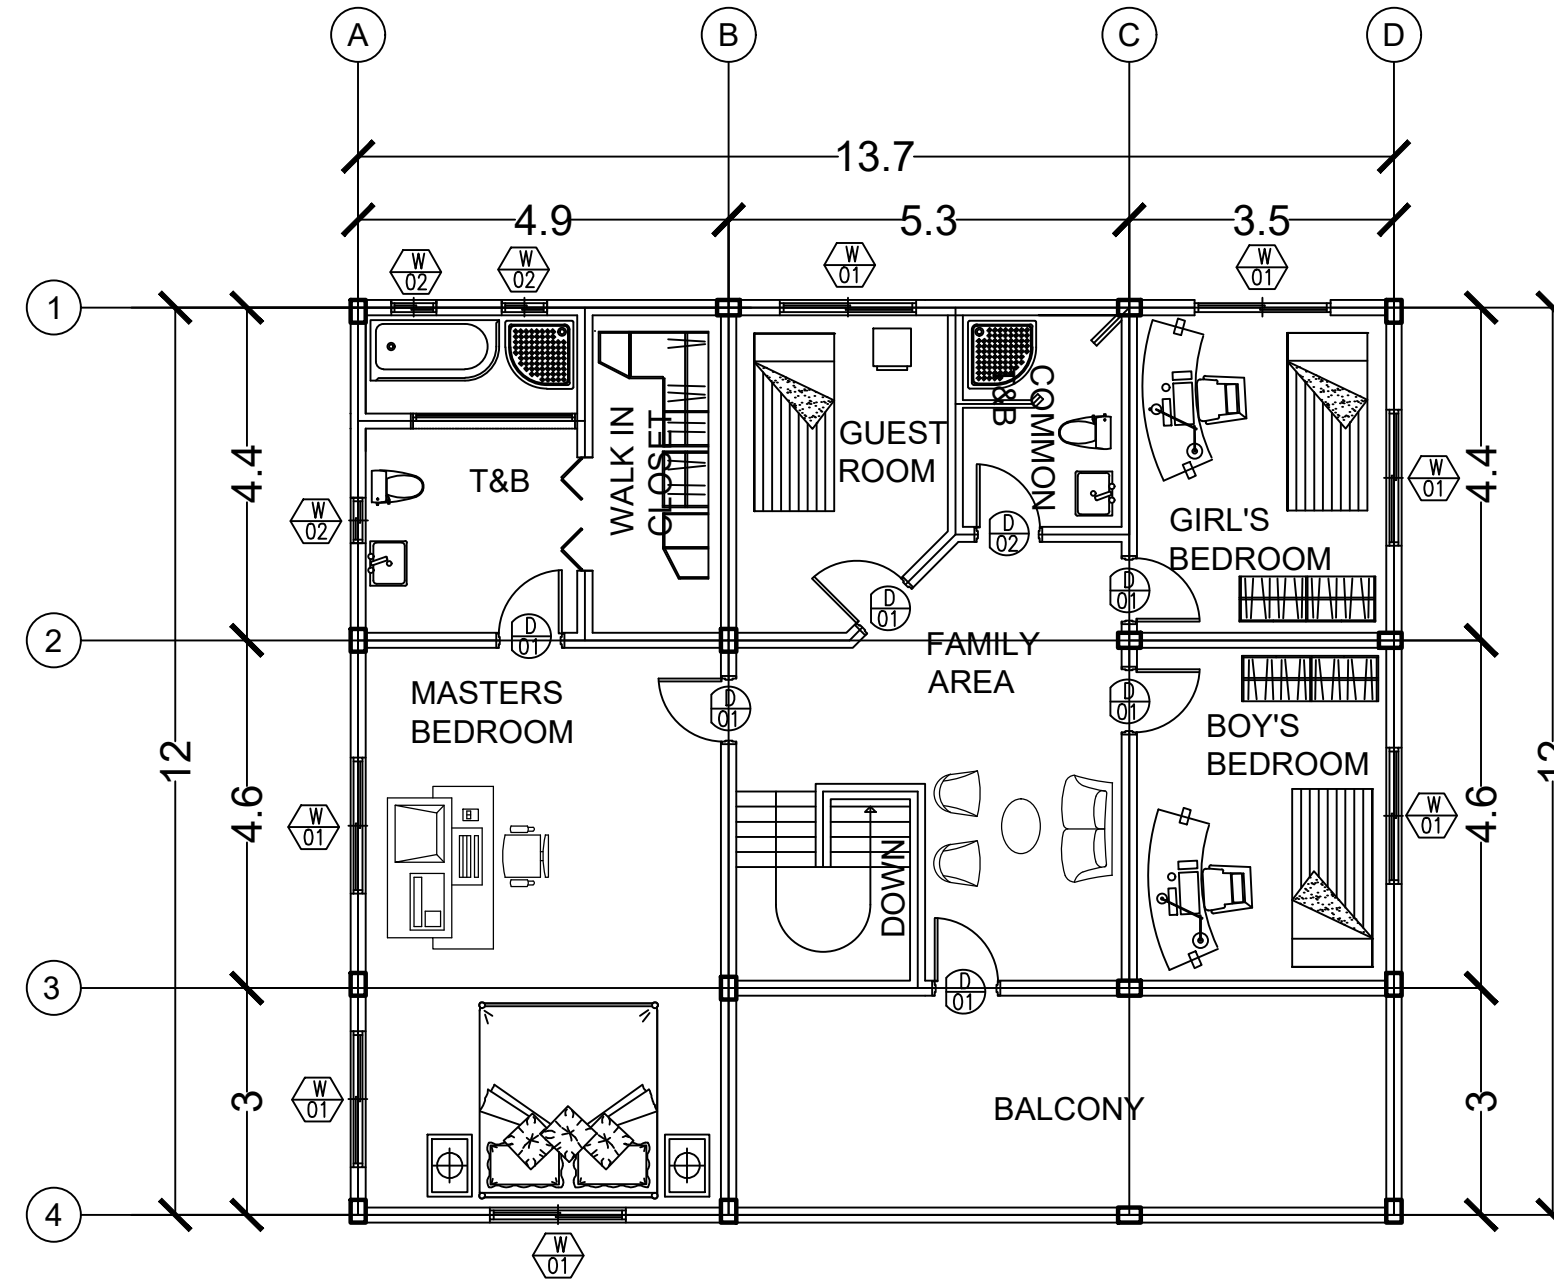


SECOND FLOOR PLAN
SCALE 1:100 MTRS.

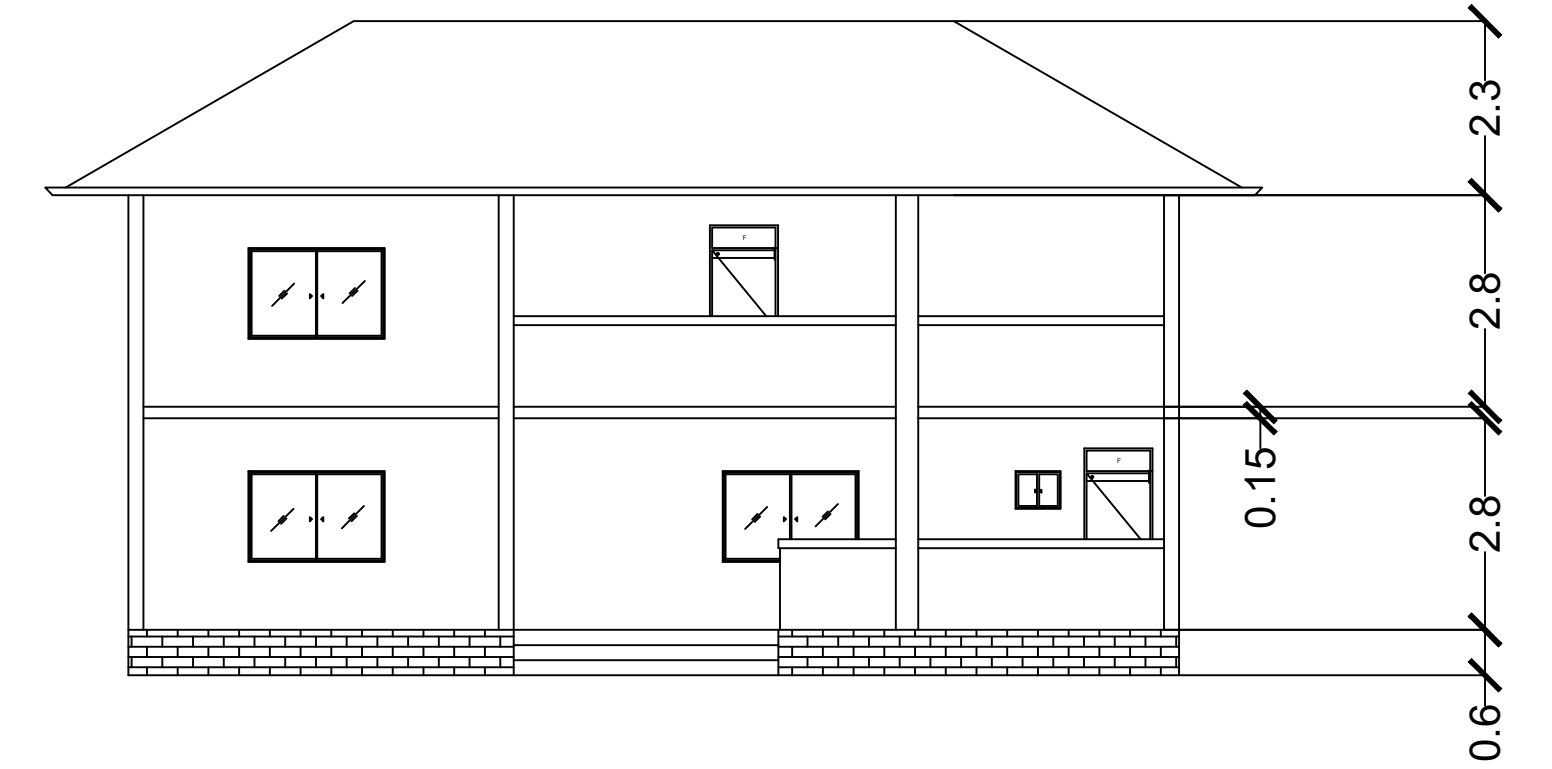


FRONT ELEVATION
SCALE 1:100 MTRS.

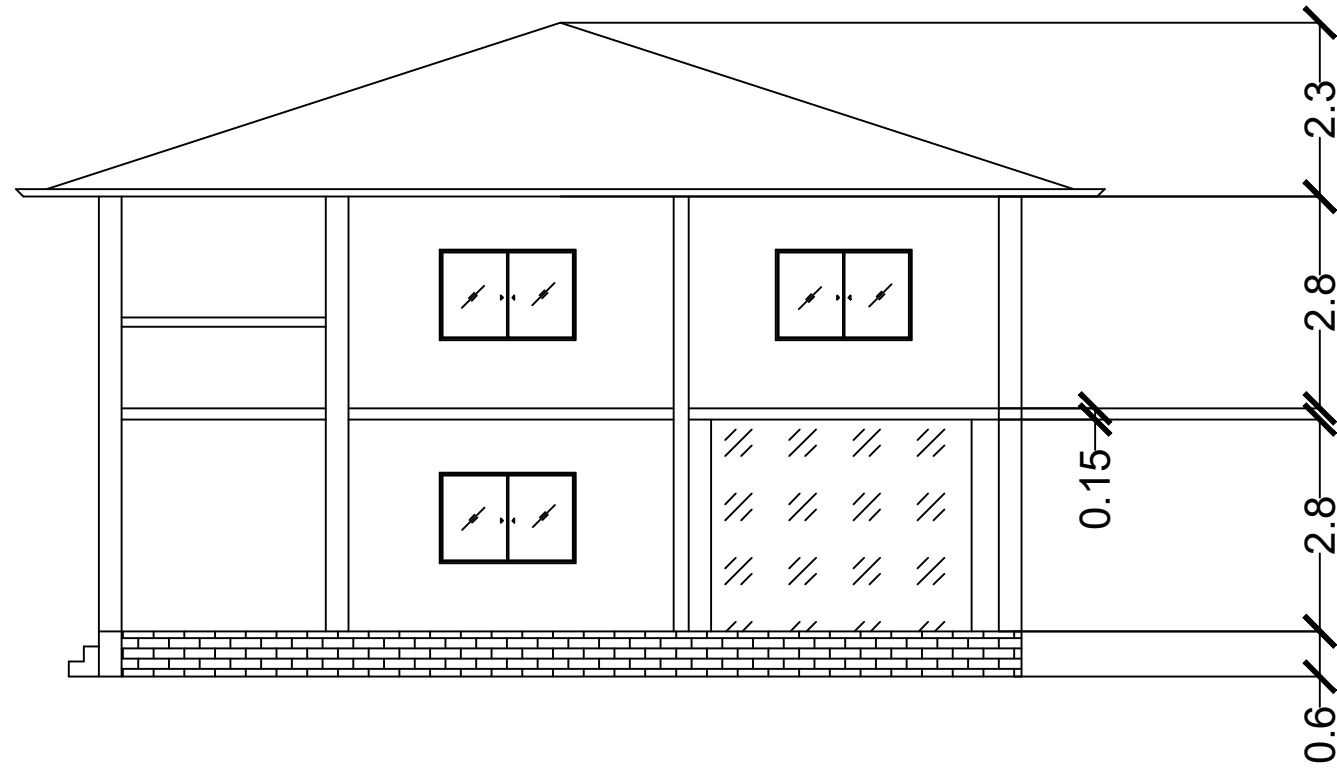

RIGHT SIDE ELEVATION
SCALE 1:100 MTRS.

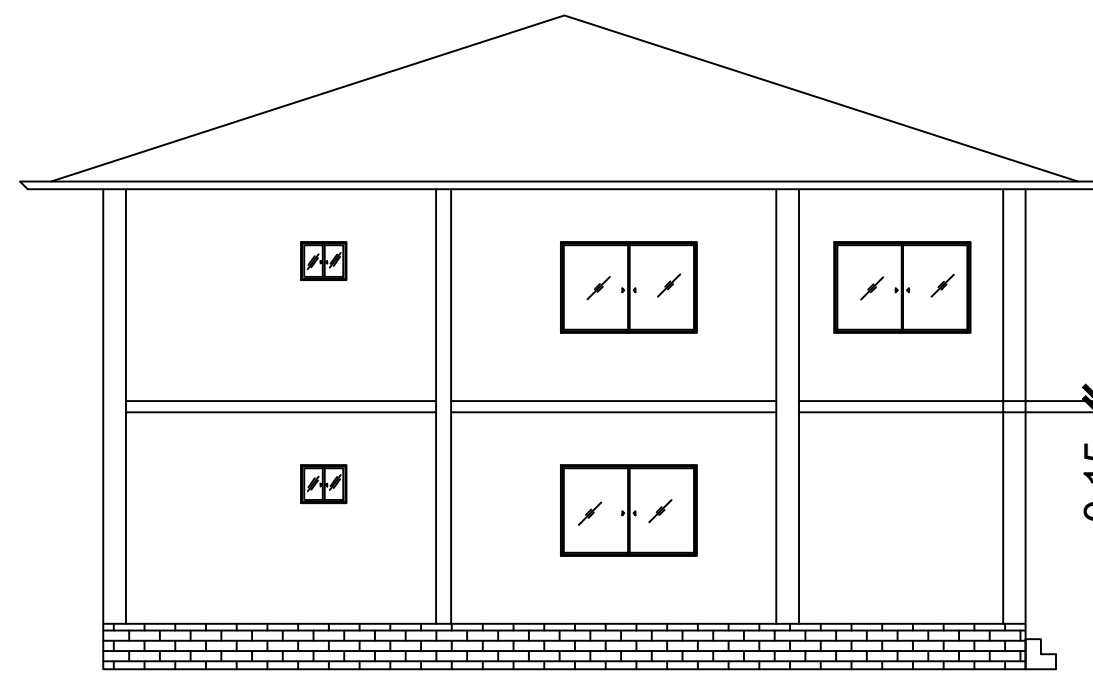


LEFT SIDE ELEVATION
SCALE 1:100 MTRS.

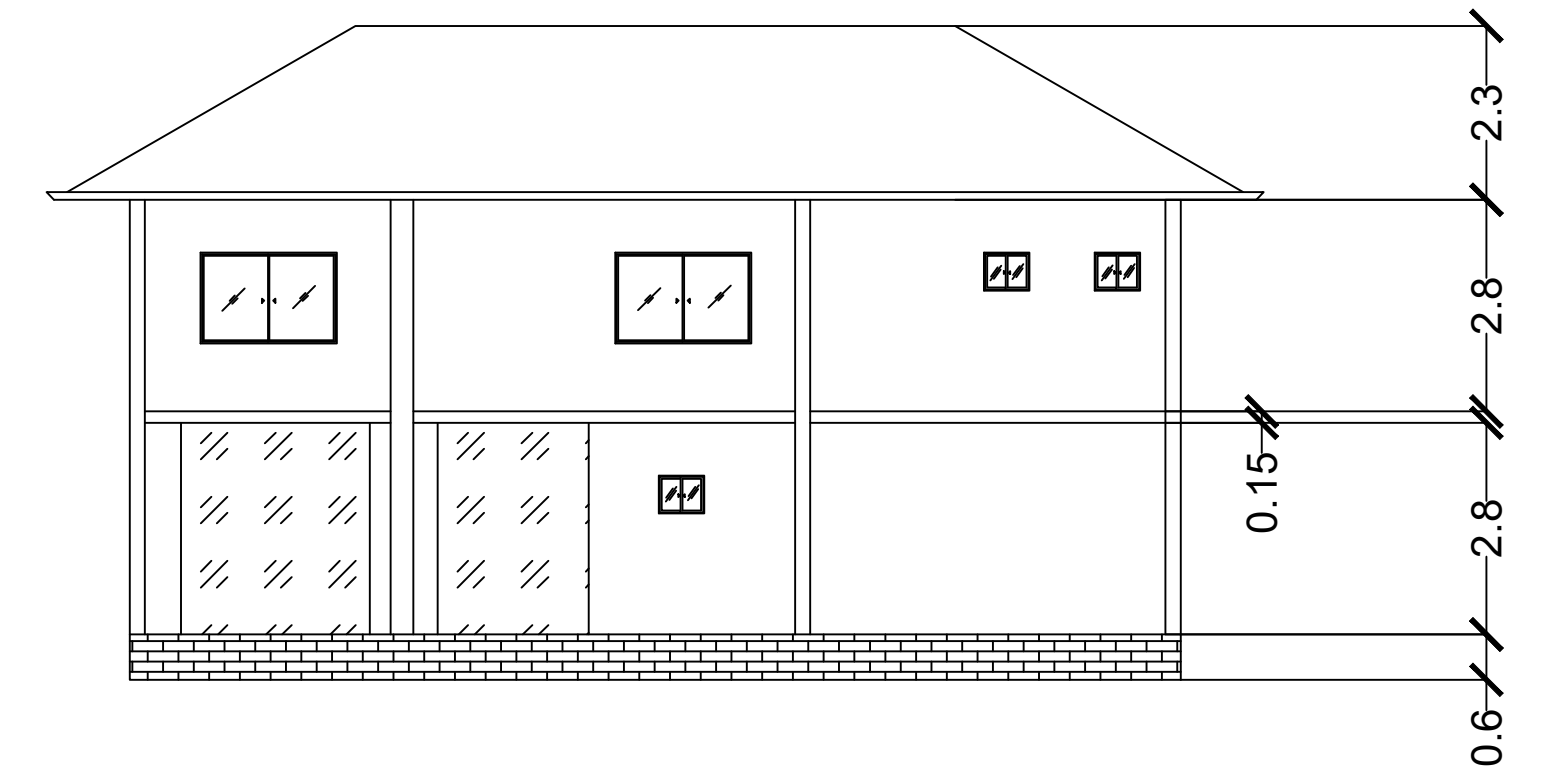


REAR ELEVATION
SCALE 1:100 MTRS.

LOGO:				PROJECT TITLE:		CONFORME:		ISSUE NO:		SHEET CONTENTS:		SHEET NO:	
				PROPOSED: TWO STOREY RESIDENTIAL BLDG.		SEBASTIEN ANDREI SALUDEZ OWNER		DATE ISSUED:		GROUND FLOOR PLAN SECOND FLOOR PLAN FRONT ELEVATION RIGHT SIDE ELEVATION LEFT SIDE ELEVATION REAR ELEVATION		A 12	
		DRAWN BY:											
		CHECKED BY:											
		DESIGNED BY:											
PRC REG NO:		TIN:											
PTR:		ISSD ON:		AT:		LOCATION		ADDRESS:					

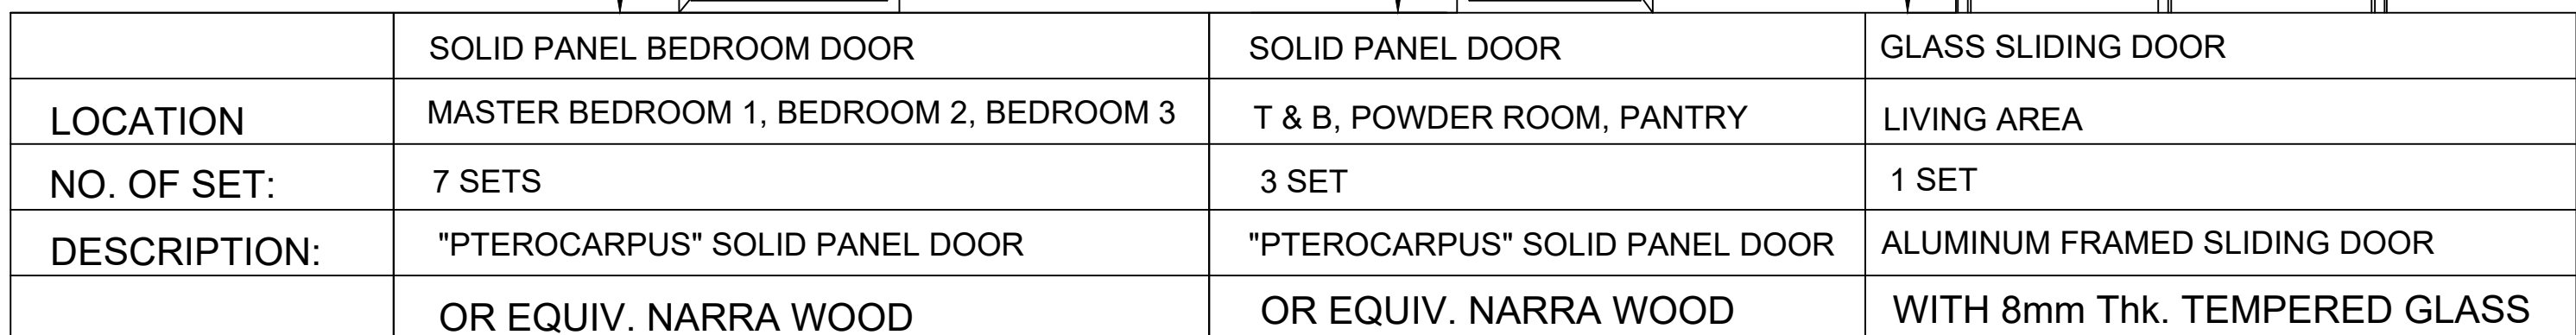


 SCHEDULE OF DOORS

SCALE 1:100 MTRS.

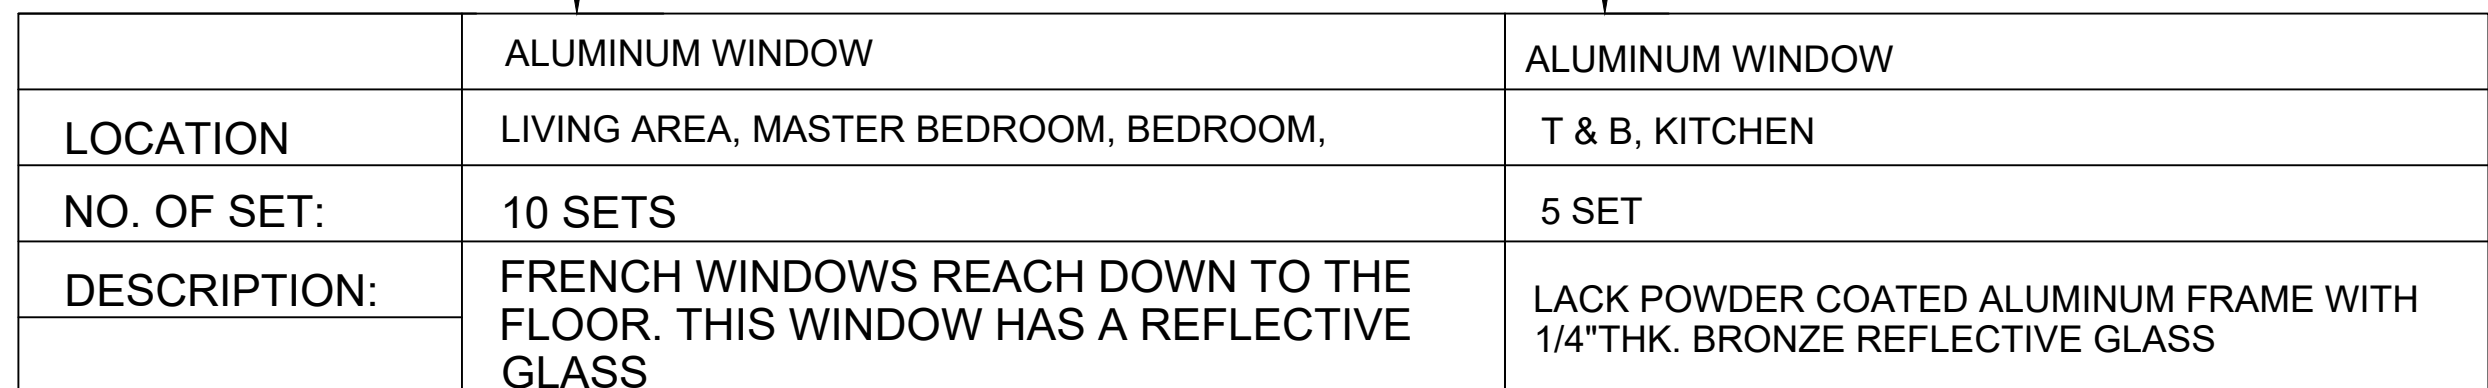

SCHEDULE OF WINDOWS
SCALE 1:100 MTRS.


LOGO:			PROJECT TITLE:	CONFORME:	ISSUE NO:	SHEET CONTENTS:	SHEET NO:
			PROPOSED: TWO STOREY RESIDENTIAL BLDG.	SEBASTIEN ANDREI SALUDEZ OWNER	DATE ISSUED:		
					DRAWN BY:		
					CHECKED BY:		
					DESIGNED BY:		
		PRC REG NO: PTR:	TIN: ISSD ON: AT:	LOCATION	ADDRESS:	ROOF PLAN SCHEDULE OF DOORS SCHEDULE OF WINDOWS	

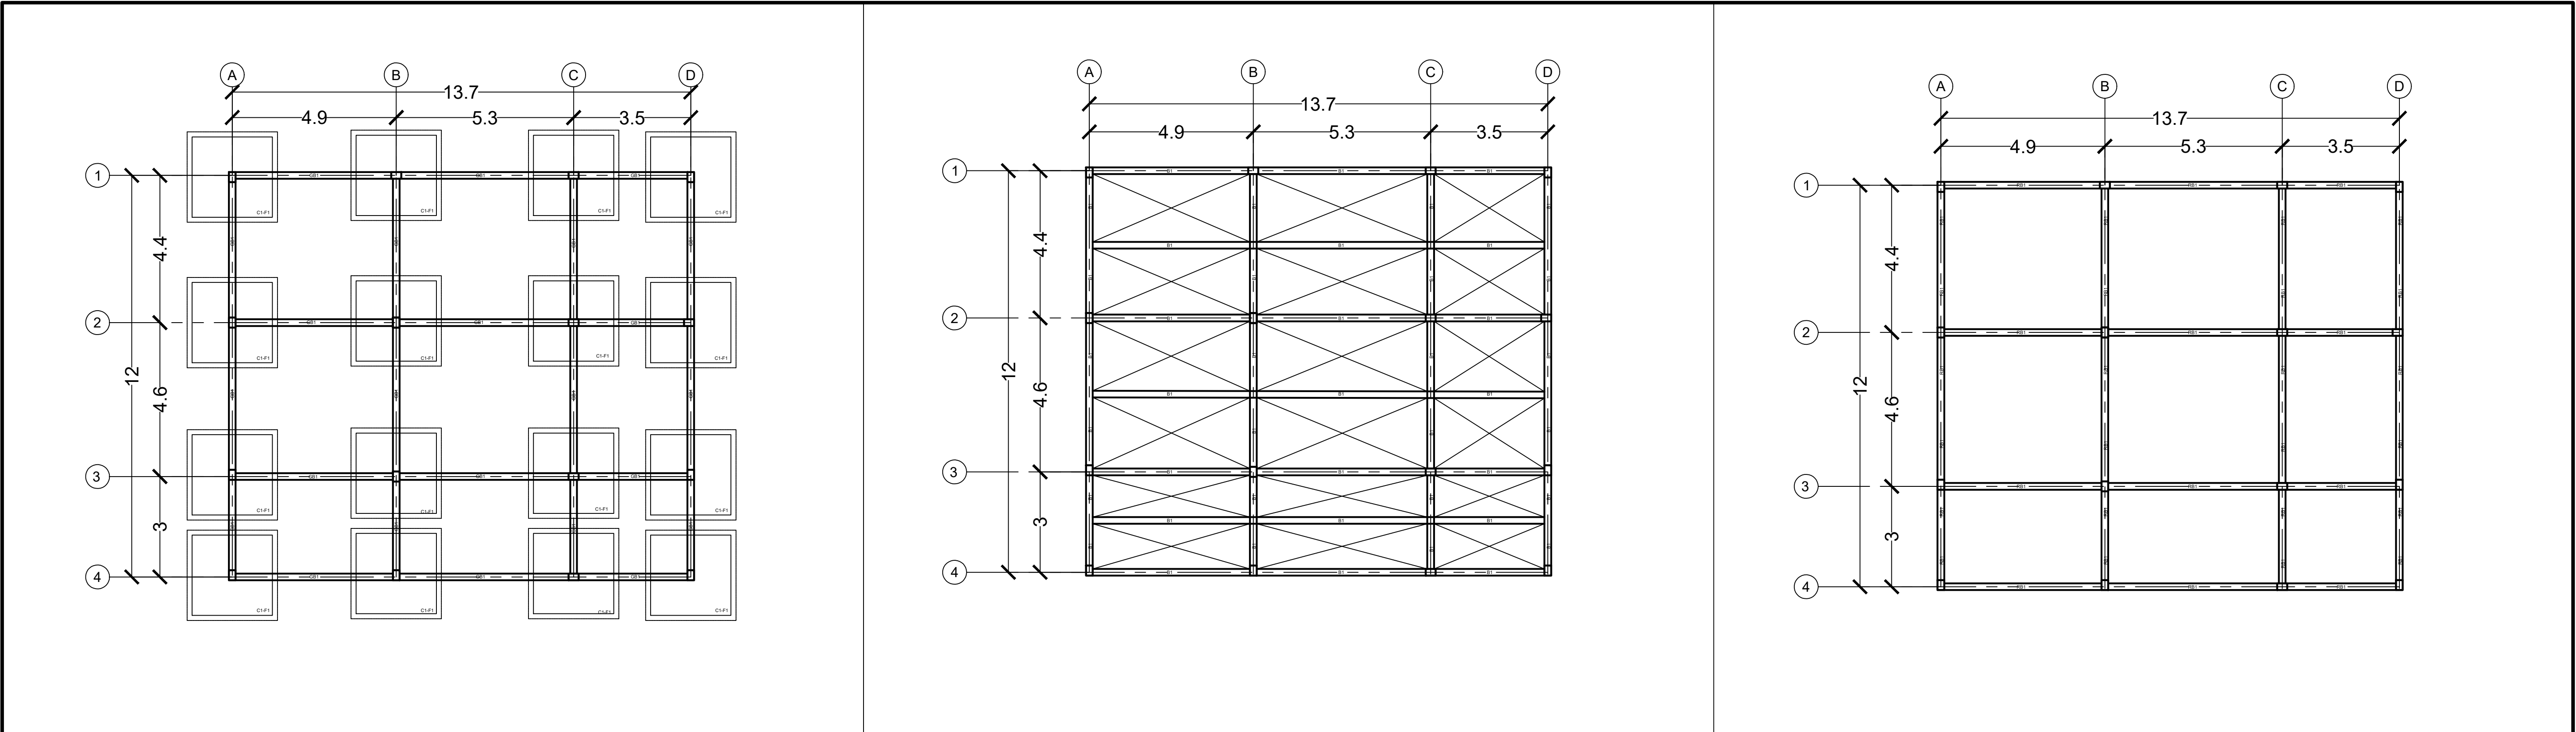


FOUNDATION PLAN
SCALE 1:100 MTRS.

SECOND FLOOR FRAMING PLAN
SCALE 1:100 MTRS.

ROOF BEAM LAYOUT
SCALE 1:100 MTRS.


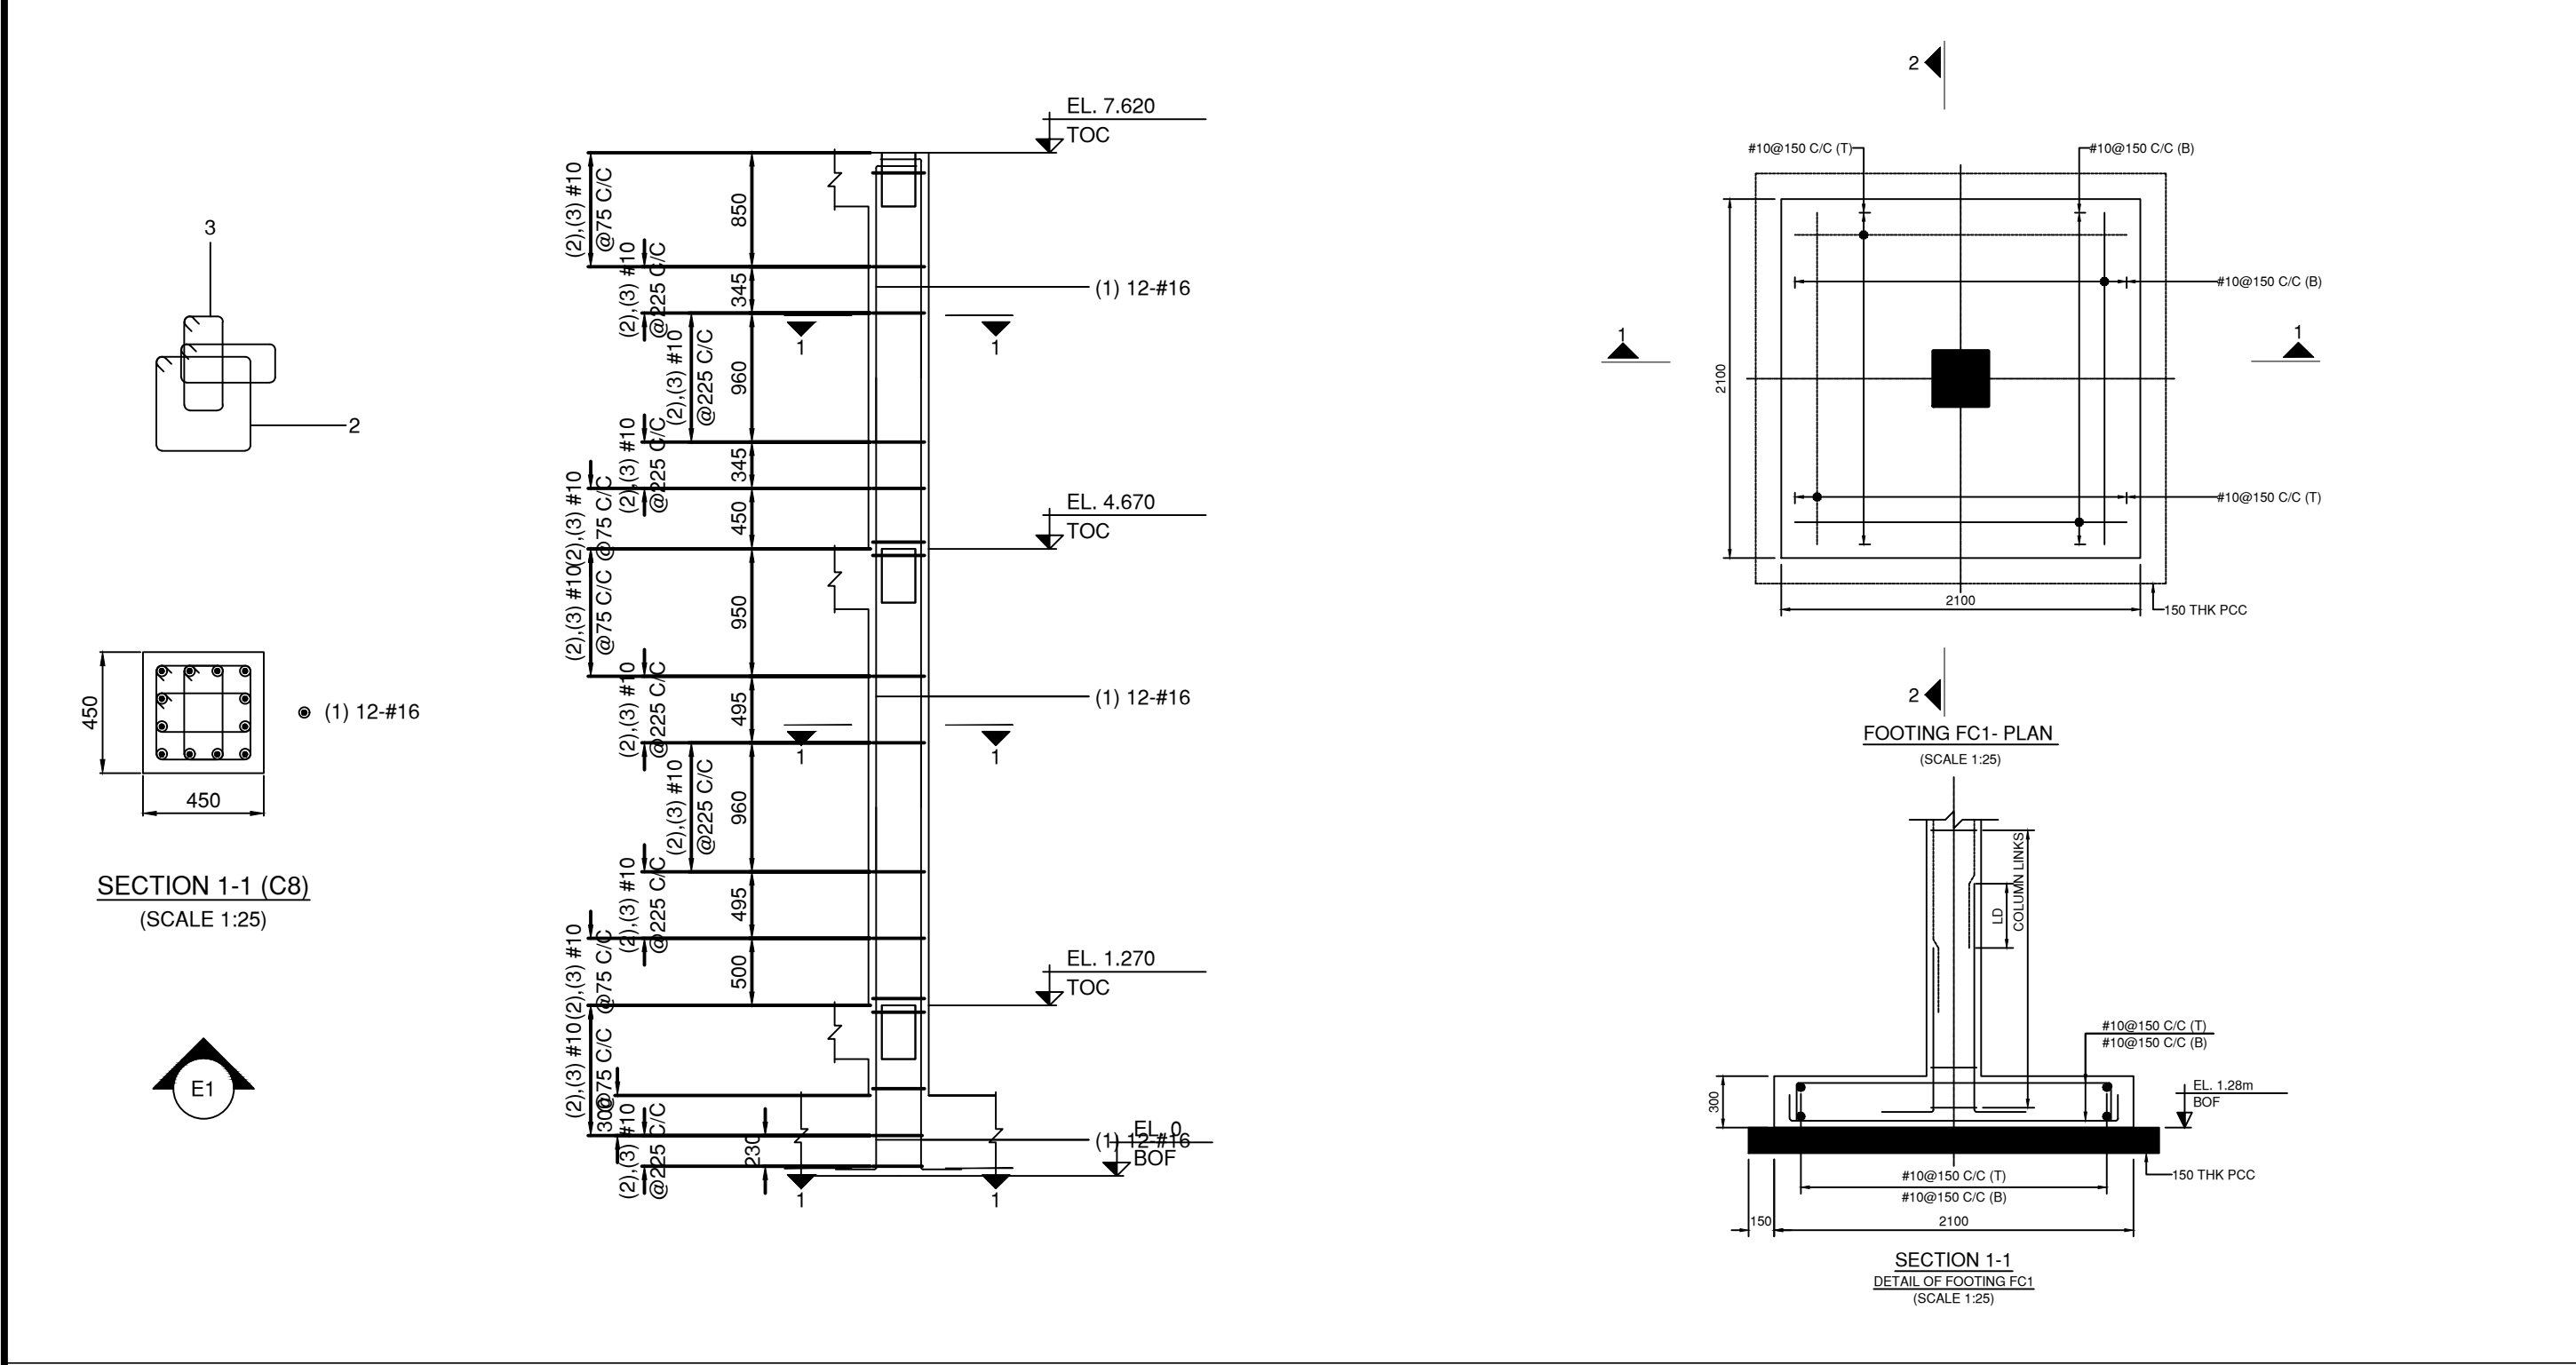


DETAILS OF C1F1
SCALE 1:100 MTRS.

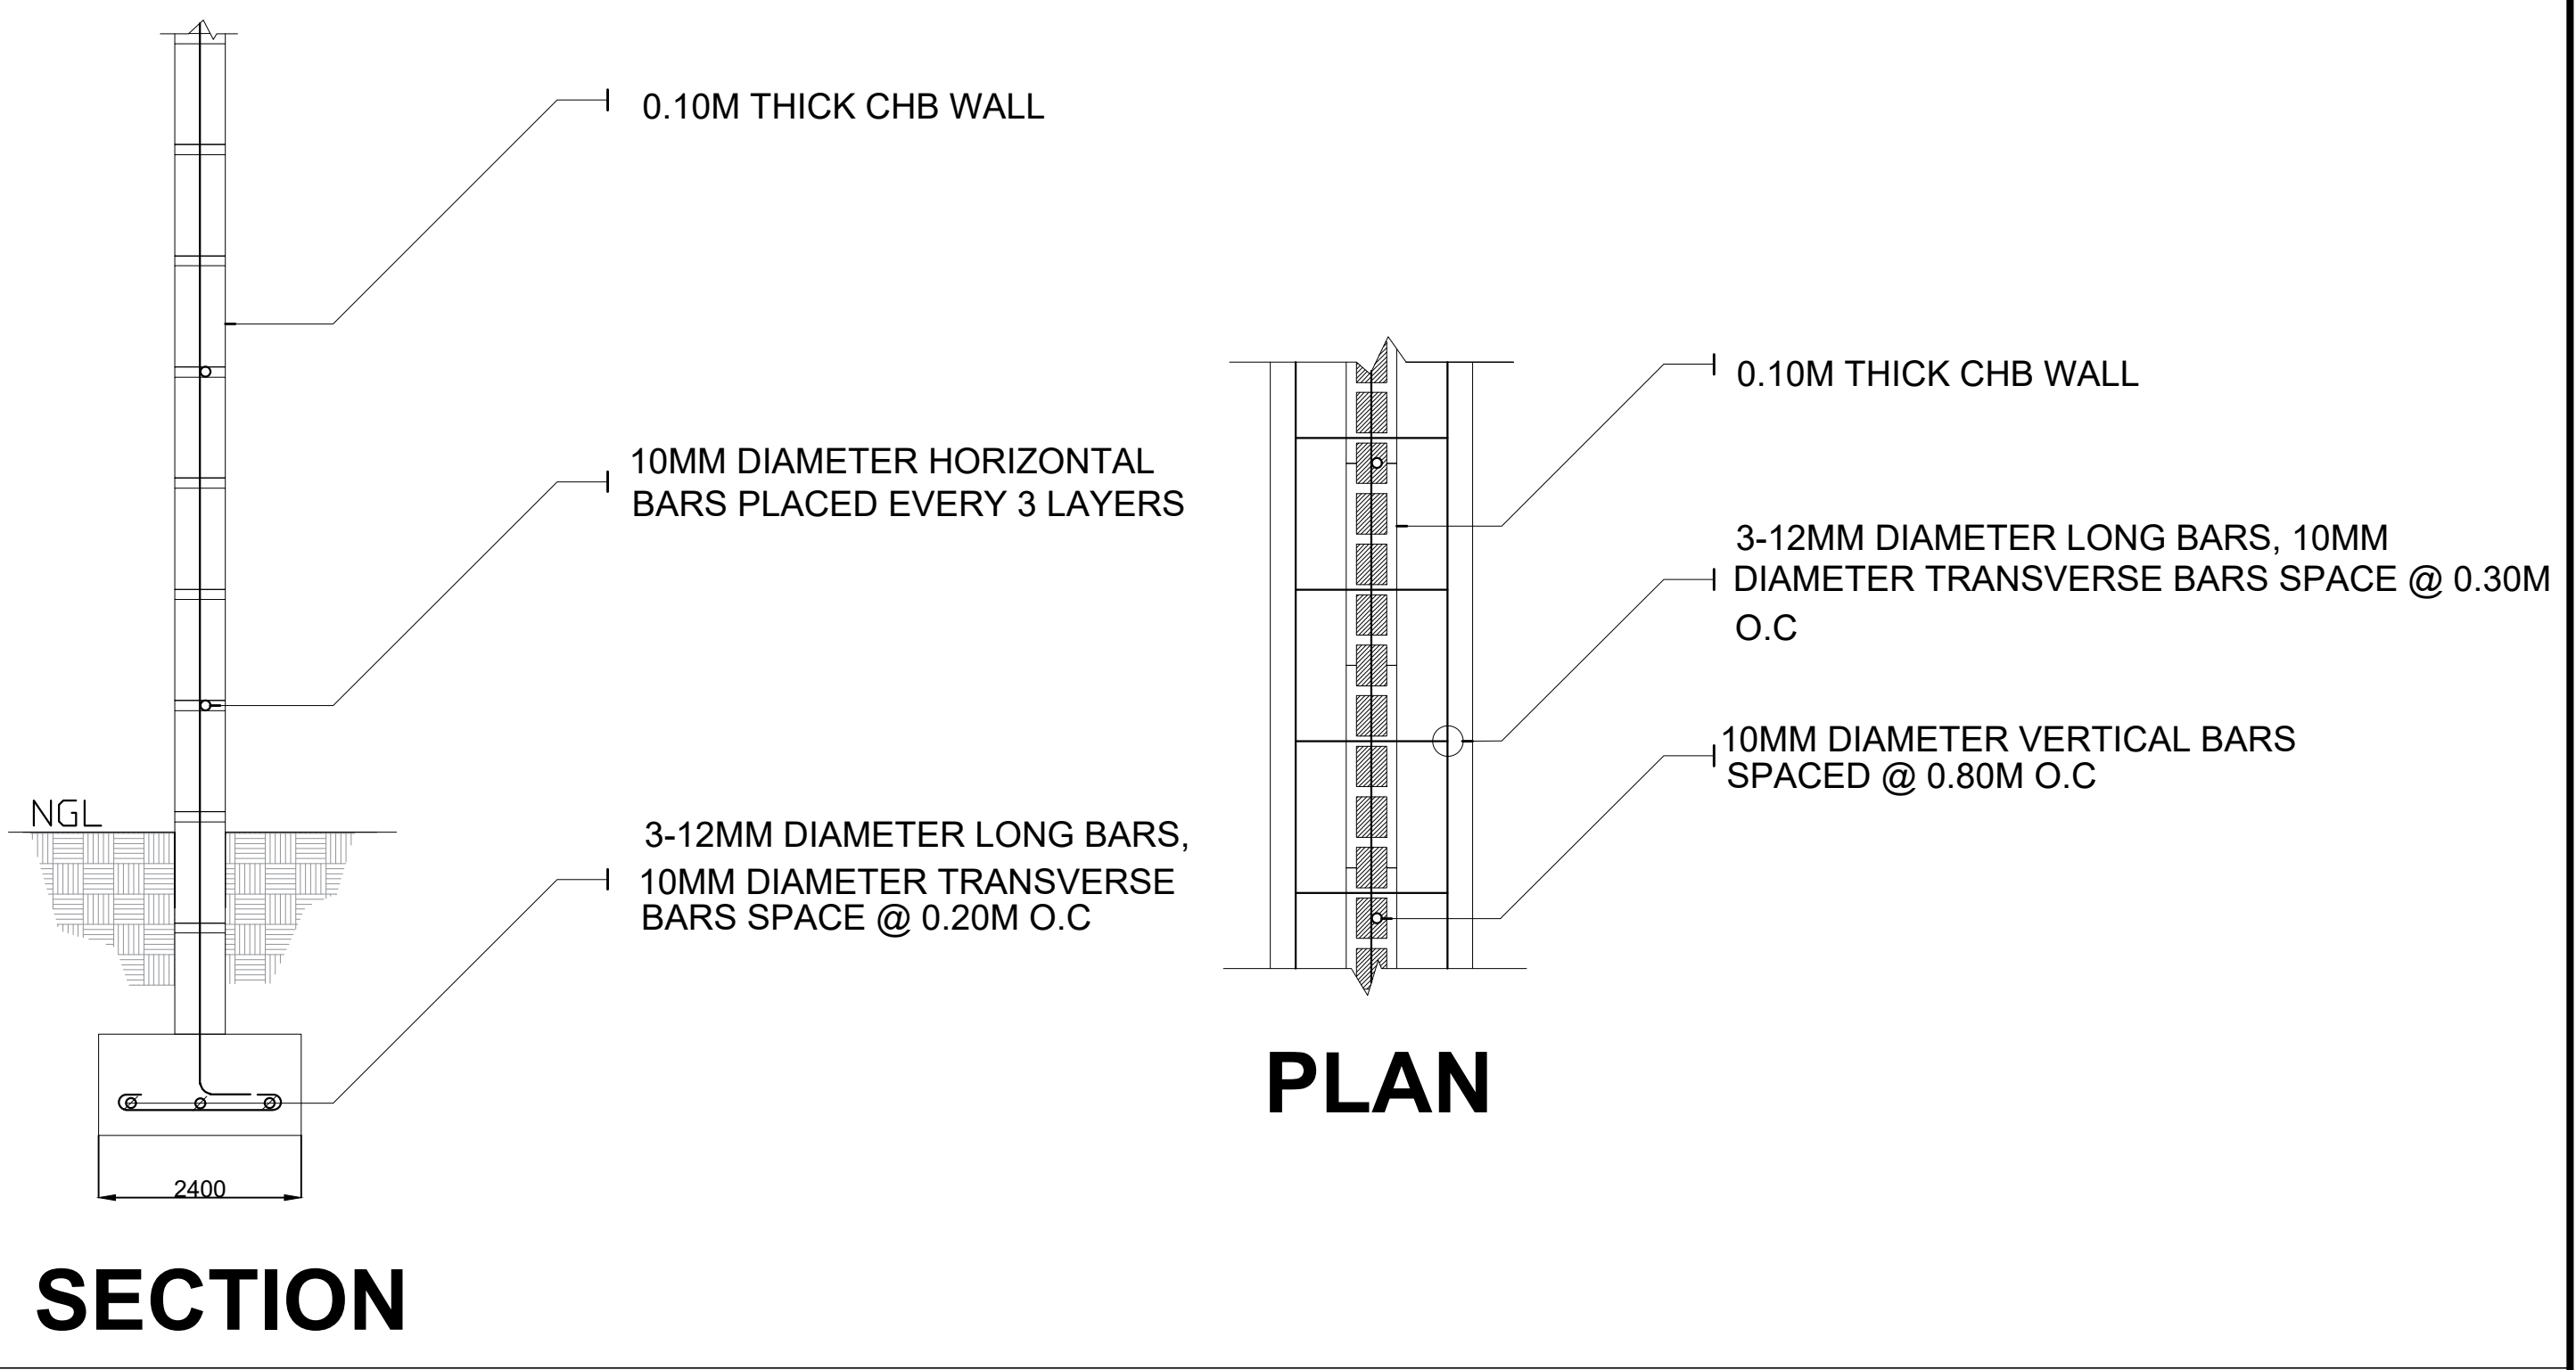



DETAILS OF W1F1
SCALE 1:100 MTRS.

LOGO:				PROJECT TITLE:		CONFORME:		ISSUE NO:		SHEET CONTENTS:		SHEET NO:	
				PROPOSED: TWO STOREY RESIDENTIAL BLDG.		SEBASTIEN ANDREI SALUDEZ OWNER		DATE ISSUED:		FOUNDATION PLAN SECOND FLOOR PLAN ROOF BEAM LAYOUT DETAILS OF C1F1 DETAILS OF W1F1		S 12	
		DRAWN BY:											
		CHECKED BY:											
		DESIGNED BY:											
		PRC REG NO:		TIN:									
		PTR:		ISSD ON:		AT:		LOCATION		ADDRESS:			

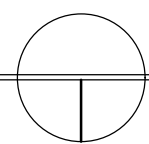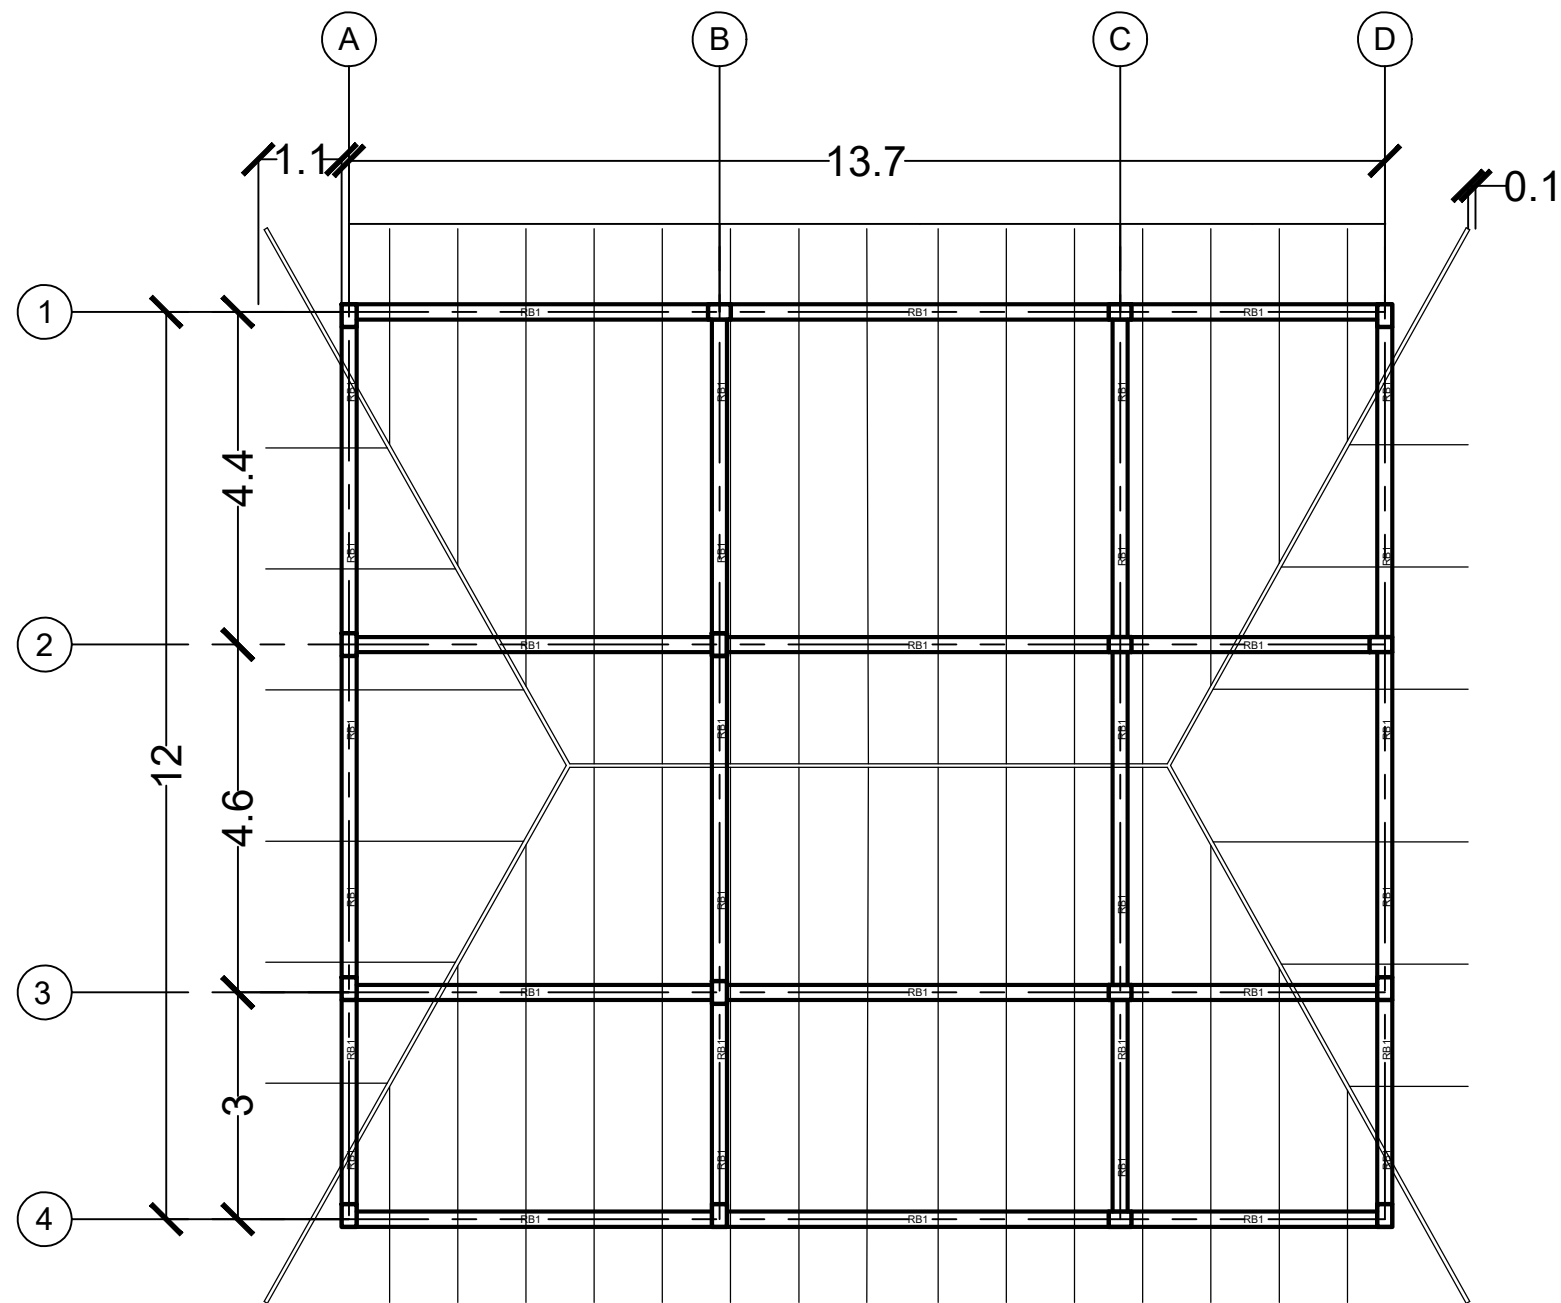


ROOF FRAMING PLAN

SCALE 1:100 MTRS.

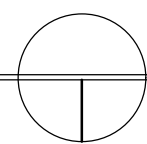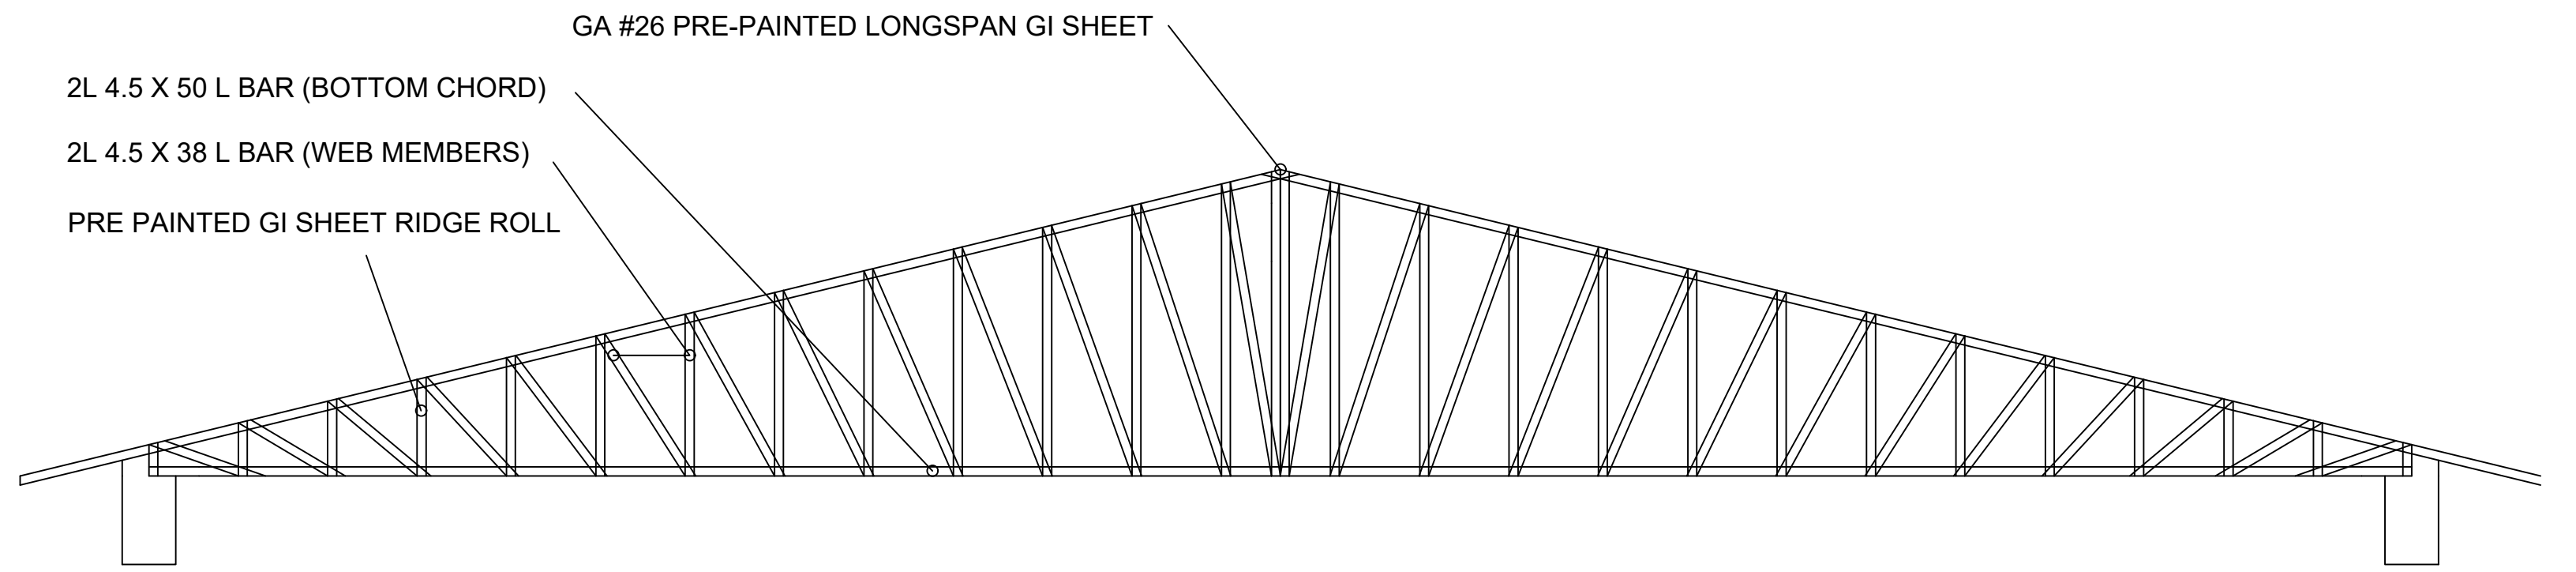








TRUSS DIAGRAM

SCALE 1:60 MTRS.

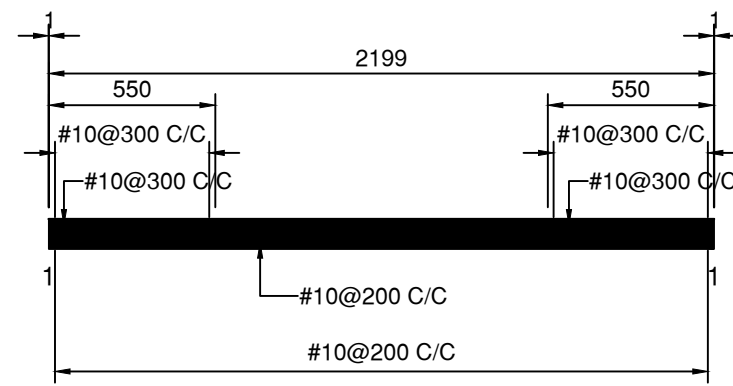


SLAB S2
(ONE WAY) (100 THK)

SECTION 2-2

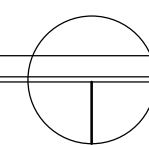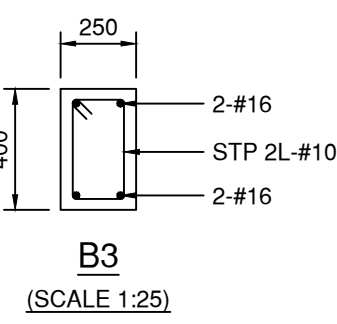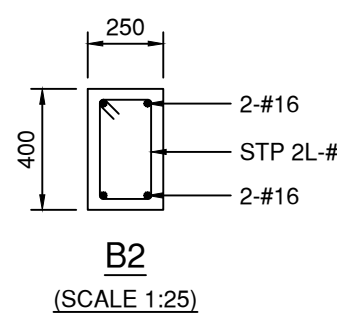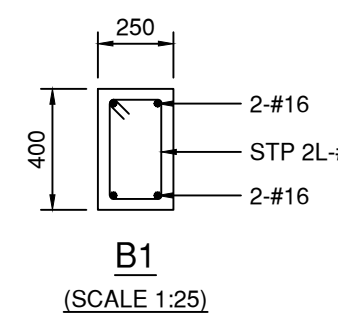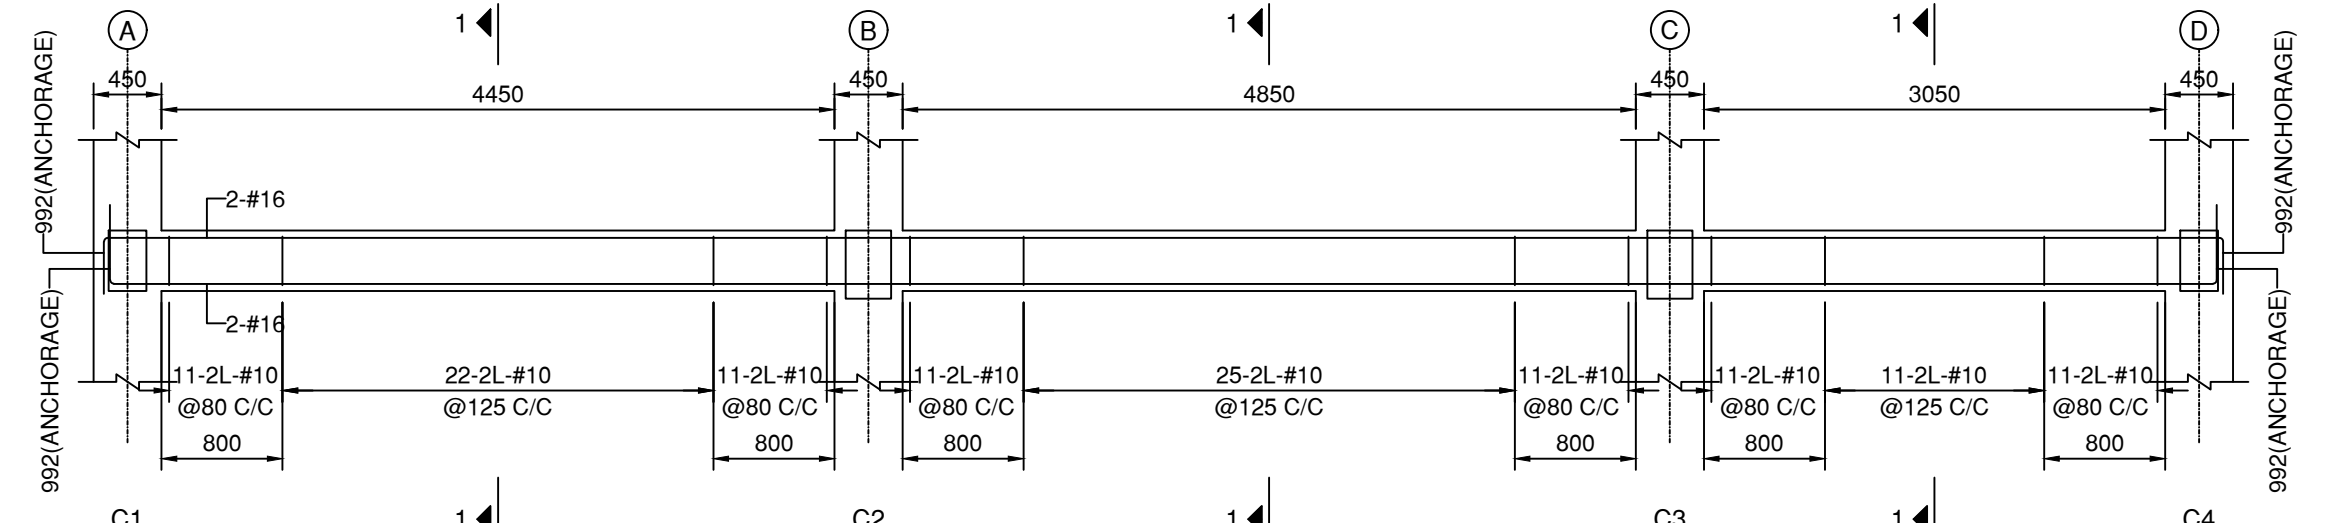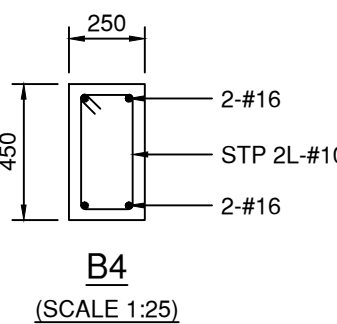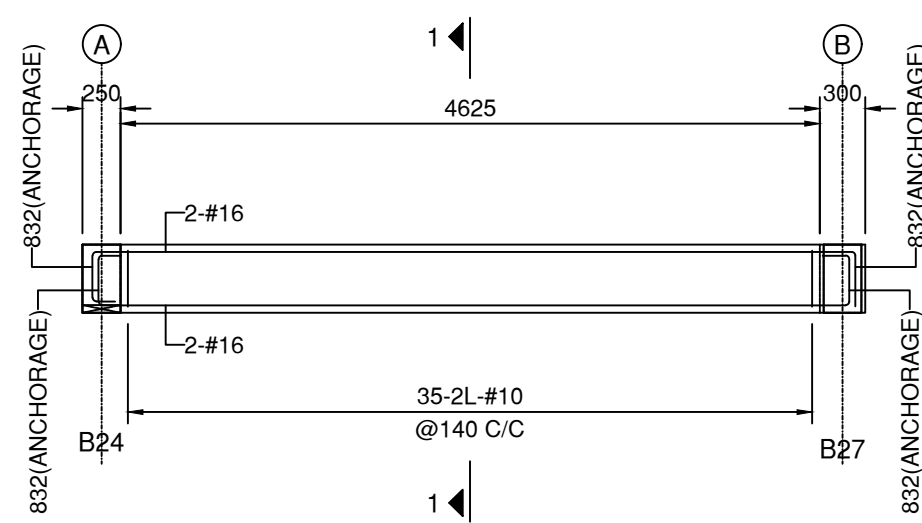

DETAIL OF SLAB

SCALE 1:60 MTRS.

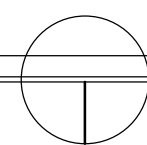

DETAIL OF BEAMS

SCALE 1:20 MTRS.

LOGO:	IMPORTANT	PROJECT TITLE:	CONFORME:	ISSUE NO:	SHEET CONTENTS:	SHEET NO:
		PROPOSED: TWO STOREY RESIDENTIAL BLDG.	SEBASTIEN ANDREI SALUDEZ OWNER	DATE ISSUED: DRAWN BY: CHECKED BY: DESIGNED BY:	ROOF FRAMING PLAN DETAIL OF SLAB TRUSS DIAGRAM DETAIL OF BEAMS	S 22
PRC REG NO:	TIN:	LOCATION	ADDRESS:			
PTR:	ISSD ON:	AT:				