




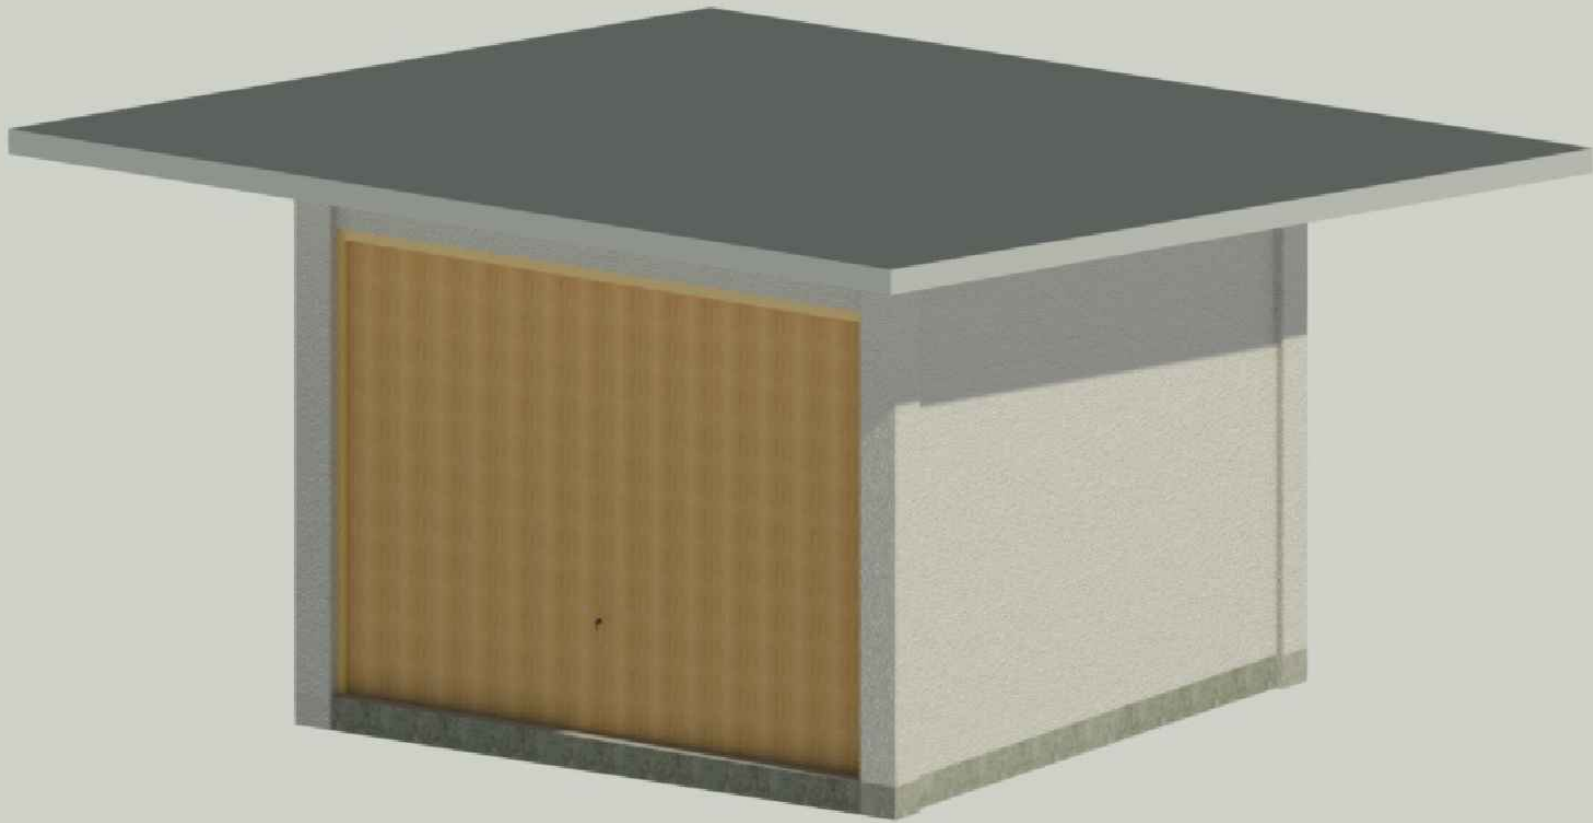



PERSPECTIVE

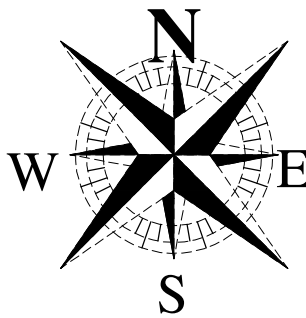

TECHNICAL DESCRIPTION		
LINES	BEARINGS	DISTANCES
LOT 31039-A		
1-2	N.04°35'W.	83.98 M.
2-3	S.76°39'E.	28.18 M.
3-4	S.85°06'E.	33.97 M.
4-5	N.43°55'E.	35.23 M.
5-6	S.06°18'E.	15.46 M.
6-7	S.32°11'E.	5.17 M.
7-8	S.50°24'E.	6.98 M.
8-9	S.66°37'E.	7.39 M.
9-10	S.60°57'E.	5.80 M.
10-11	S.51°45'E.	13.66 M.
11-12	S.74°03'W.	15.05 M.
12-13	S.45°06'W.	38.44 M.
13-14	S.70°50'W.	52.67 M.
14-1	S.57°29'W.	23.68 M.





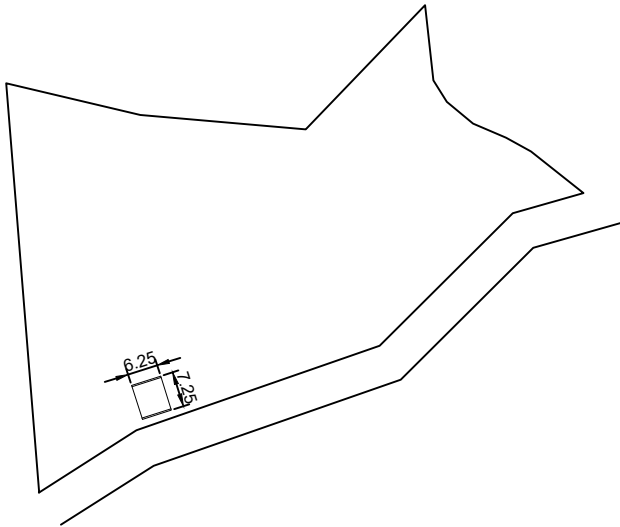


SITE DEVELOPMENT PLAN

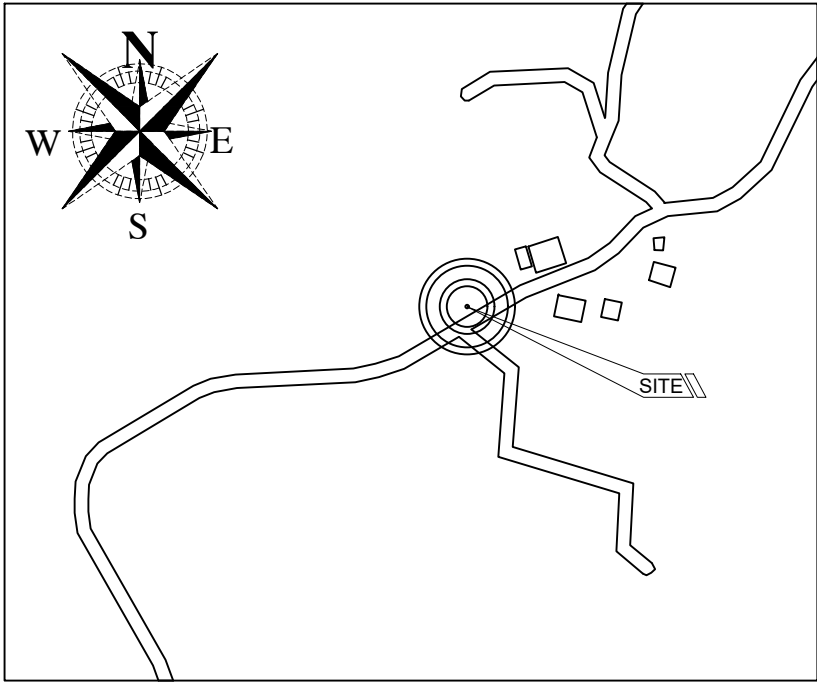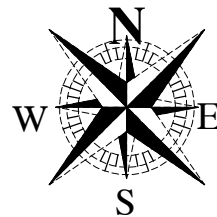


VICINITY MAP


	PROJECT TITLE:	CONFORME:	SHEET CONTENT:	PROJECT NO.:	
	PROPOSED: CONSTRUCTION OF PORTABLE GASOLINE STATION			DRAWN BY:	
	PROJECT LOCATION:			DESIGN BY:	
				CHECKED BY:	
				DATE	

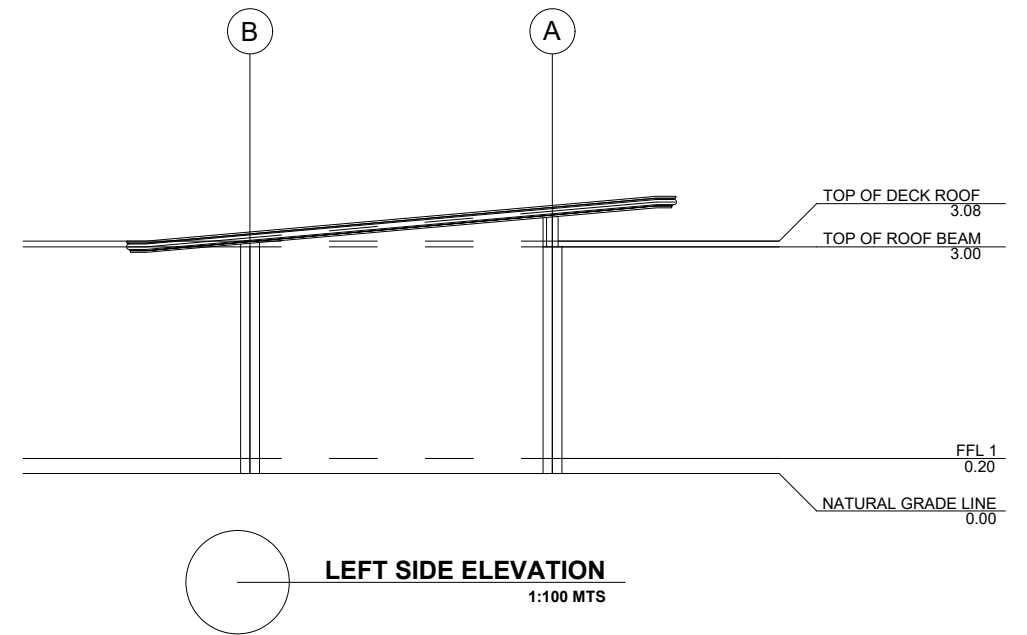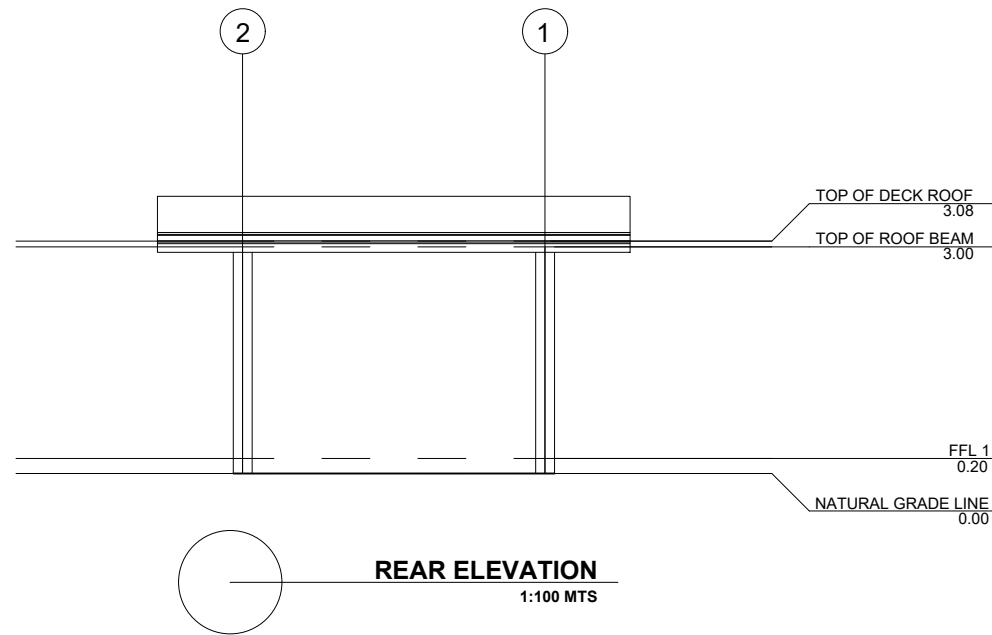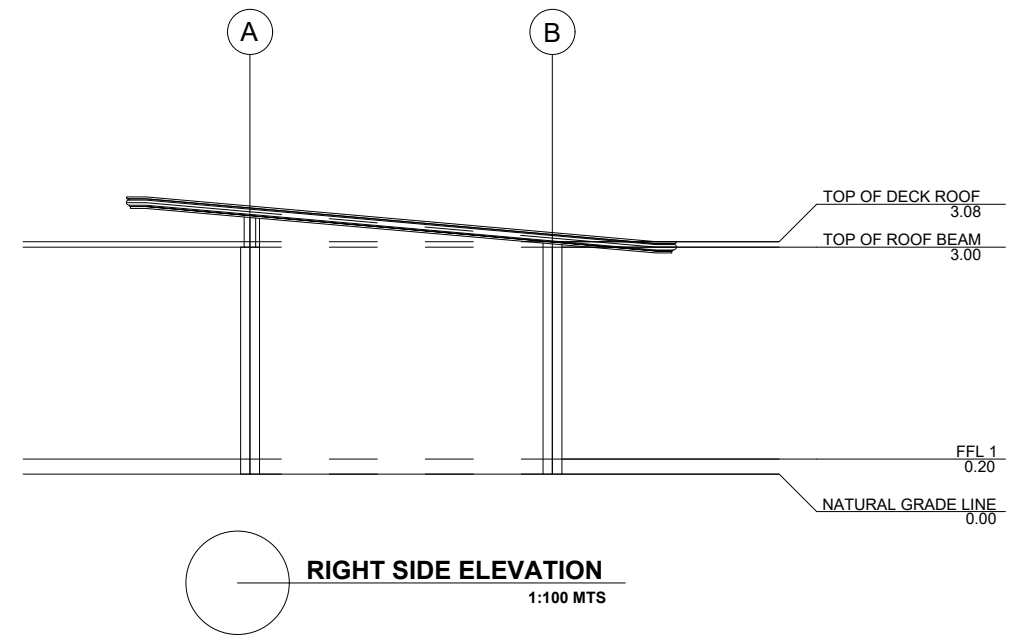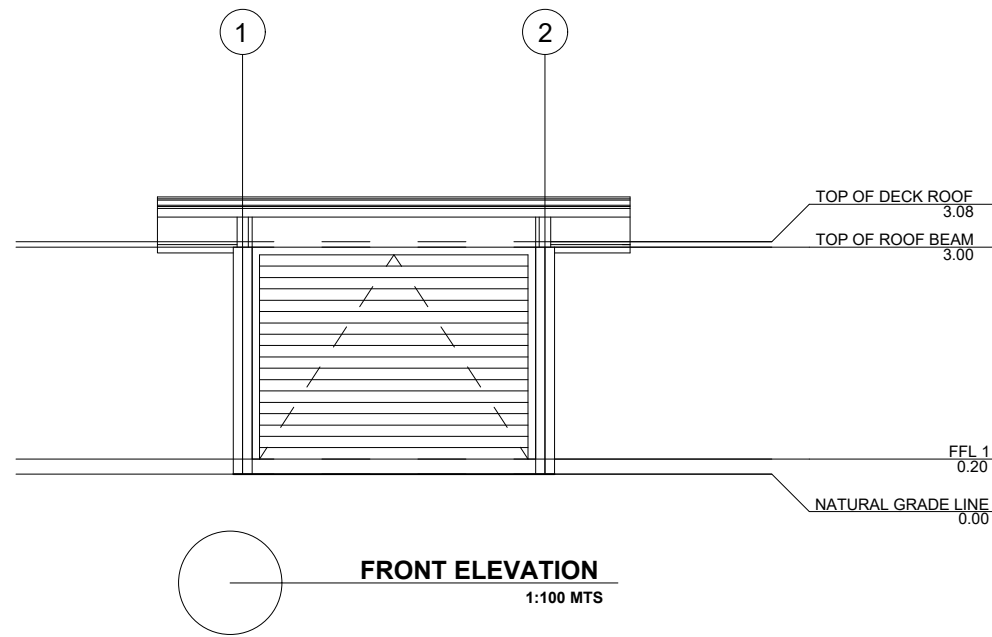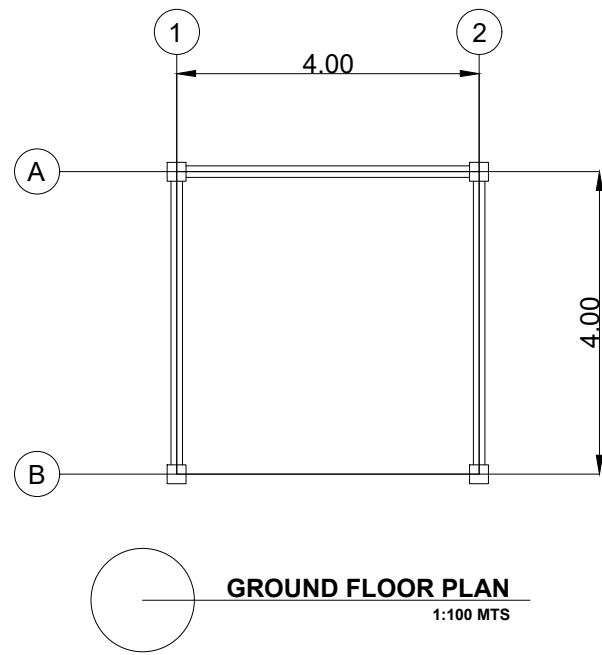



		PROJECT TITLE:	CONFORME:	SHEET CONTENT:	PROJECT NO.:	SHEET NO.
		PROPOSED: CONSTRUCTION OF PORTABLE GASOLINE STATION	_____ OWNER		DRAWN BY:	
					DESIGN BY:	
					CHECKED BY:	
	PROJECT LOCATION:	DATE				

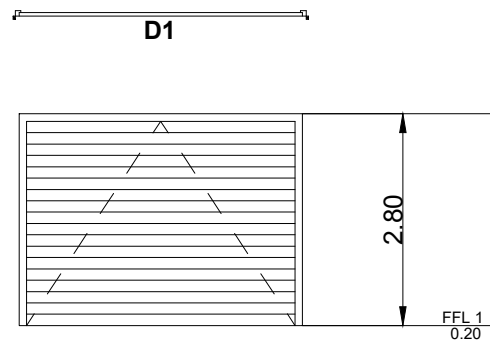

DOOR SCHEDULE
1:100 MTS

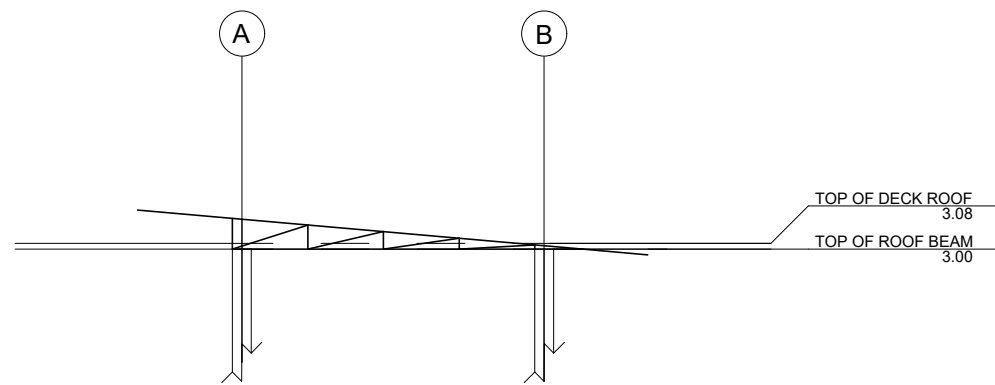


TRUSS DIAGRAM
1:100 MTS

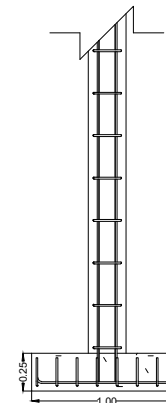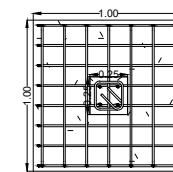


BEAM DETAILS
1:50 MTS


COLUMN FOOTING DETAIL
1:50 MTS

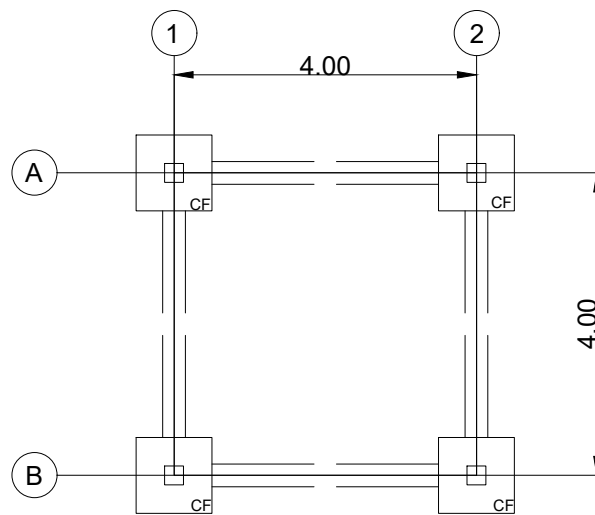

FOUNDATION PLAN
1:100 MTS

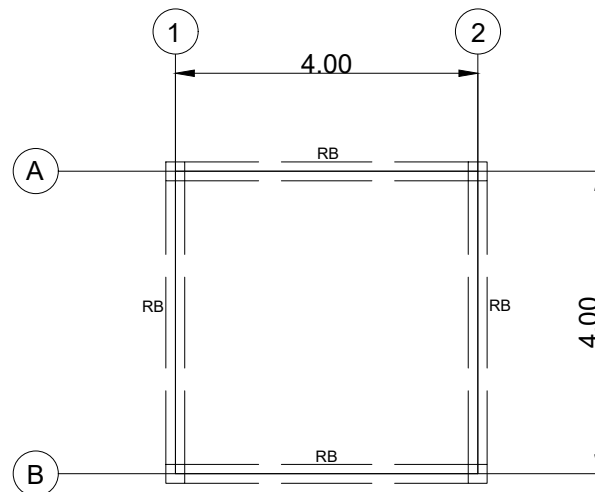

ROOF BEAM PLAN
1:100 MTS

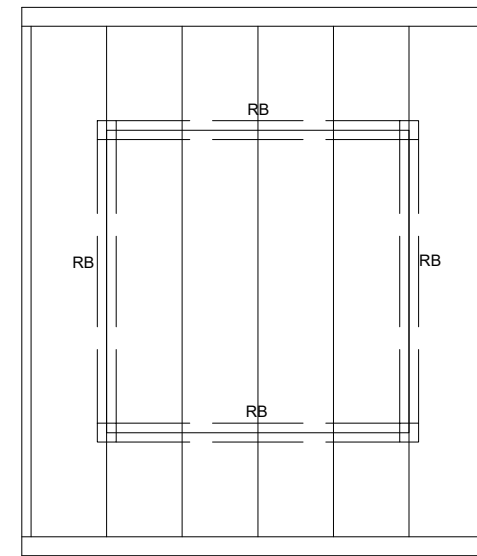

ROOF FRAMING PLAN
1:100 MTS

		PROJECT TITLE:	CONFORME:	SHEET CONTENT:	PROJECT NO.:	SHEET NO.
		PROPOSED: CONSTRUCTION OF PORTABLE GASOLINE STATION	_____ OWNER		DRAWN BY:	
		DESIGN BY:				
		CHECKED BY:				
		DATE				
		PROJECT LOCATION:				