






	PROJECT:	PREPARED BY:	OWNER:	SHEET
	PROPOSED 6-STOREY MUNICIPAL BUILDING	Ricki Lei D. Dela Rosa	ENGR. ARBIE MARIZ A. REVILLA	A-1 1
	LOCATION:	BSCE IV-A		
	171 LAOAG - PAOAY RD, 2900 LAOG CITY, ILOCOS NORTE	21-050147	ARCHITECTURAL DRAWING	

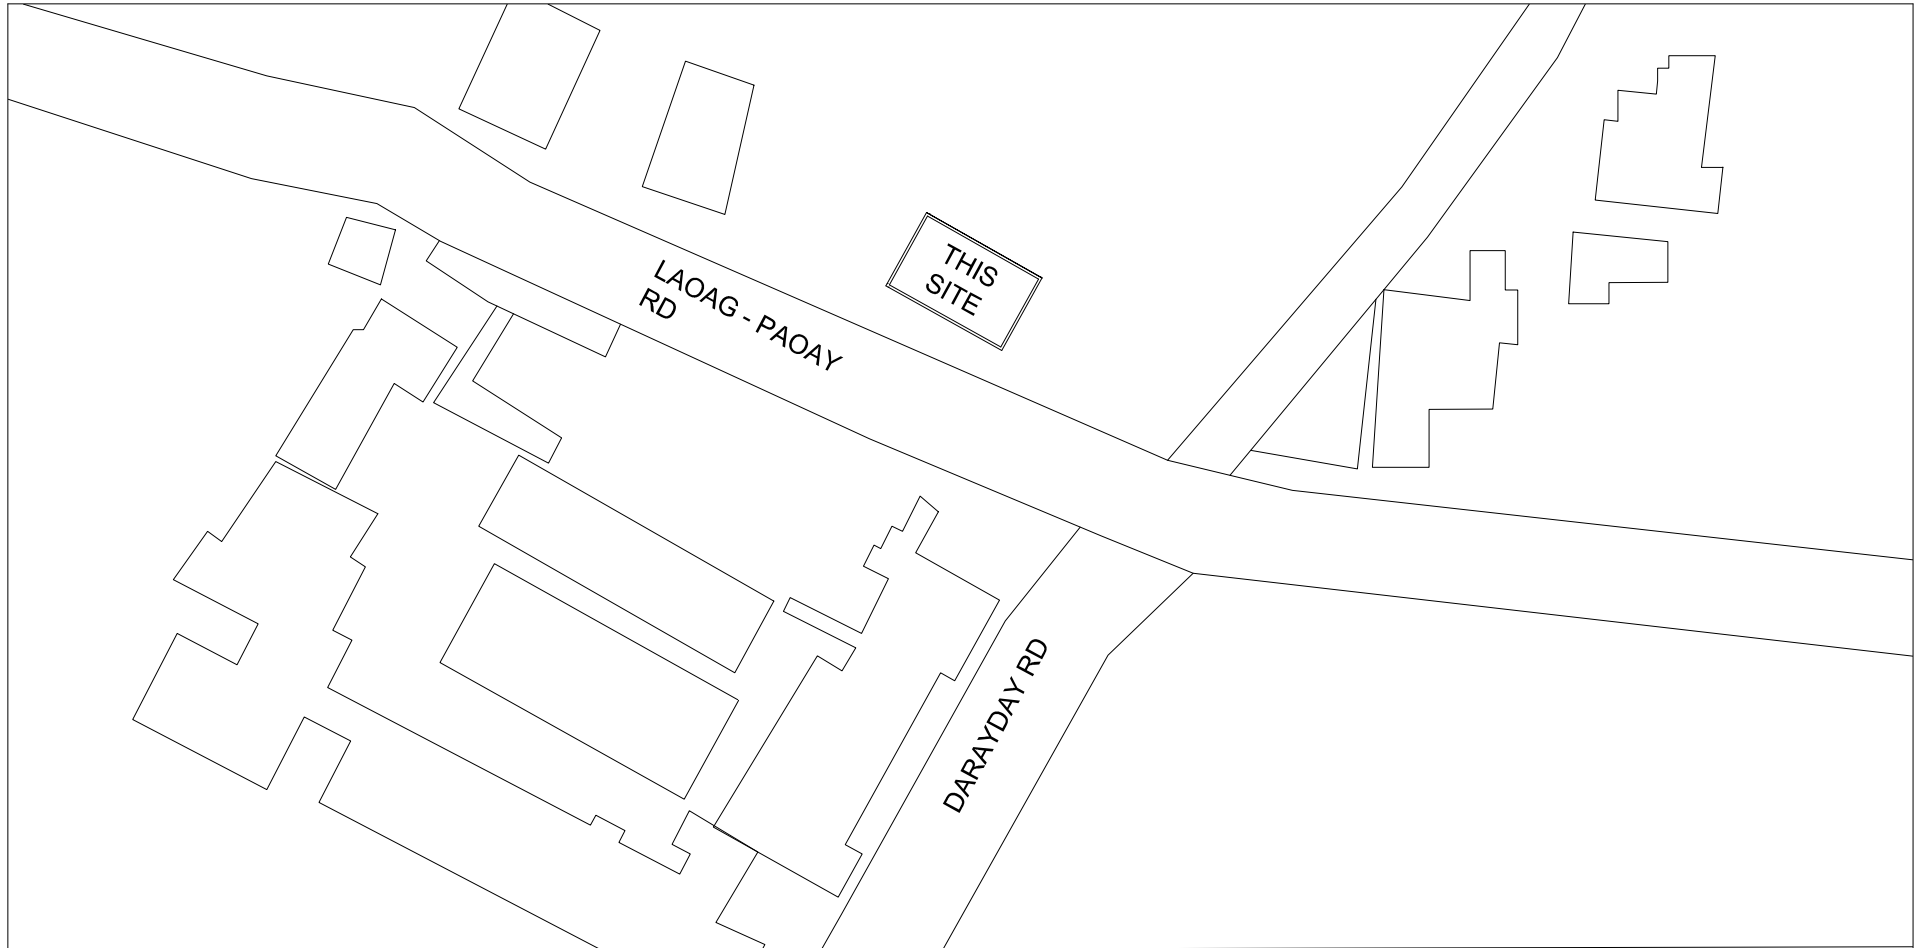

VICINITY MAP
NTS



	PROJECT:	PREPARED BY:	OWNER:	SHEET A-1 2
	PROPOSED 6-STOREY MUNICIPAL BUILDING	Ricki Lei D. Dela Rosa	ENGR. ARBIE MARIZ A. REVILLA	
	LOCATION:	BSCE IV-A		
	171 LAOAG - PAOAY RD, 2900 LAOG CITY, ILOCOS NORTE	21-050147	ARCHITECTURAL DRAWING	

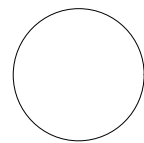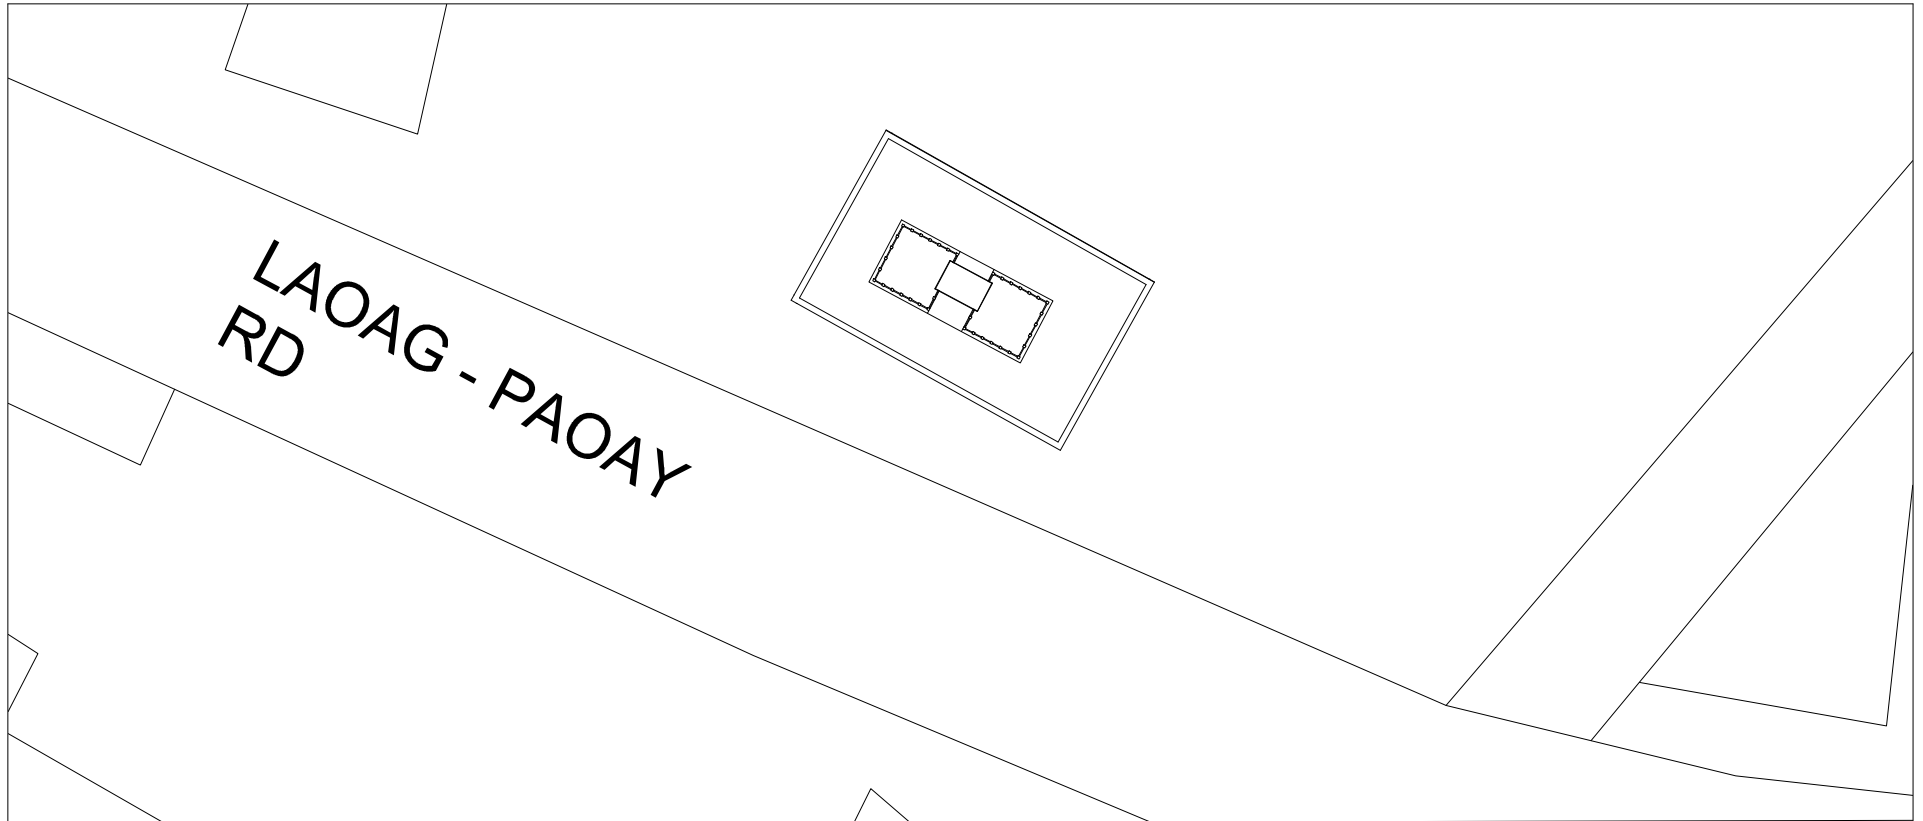

SITE DEVELOPMENT PLAN

NTS

	PROJECT:	PREPARED BY:	OWNER:	SHEET
	PROPOSED 6-STOREY MUNICIPAL BUILDING	Ricki Lei D. Dela Rosa	ENGR. ARBIE MARIZ A. REVILLA	A-1 3
	LOCATION:	BSCE IV-A		
	171 LAOAG - PAOAY RD, 2900 LAOG CITY, ILOCOS NORTE	21-050147	ARCHITECTURAL DRAWING	

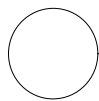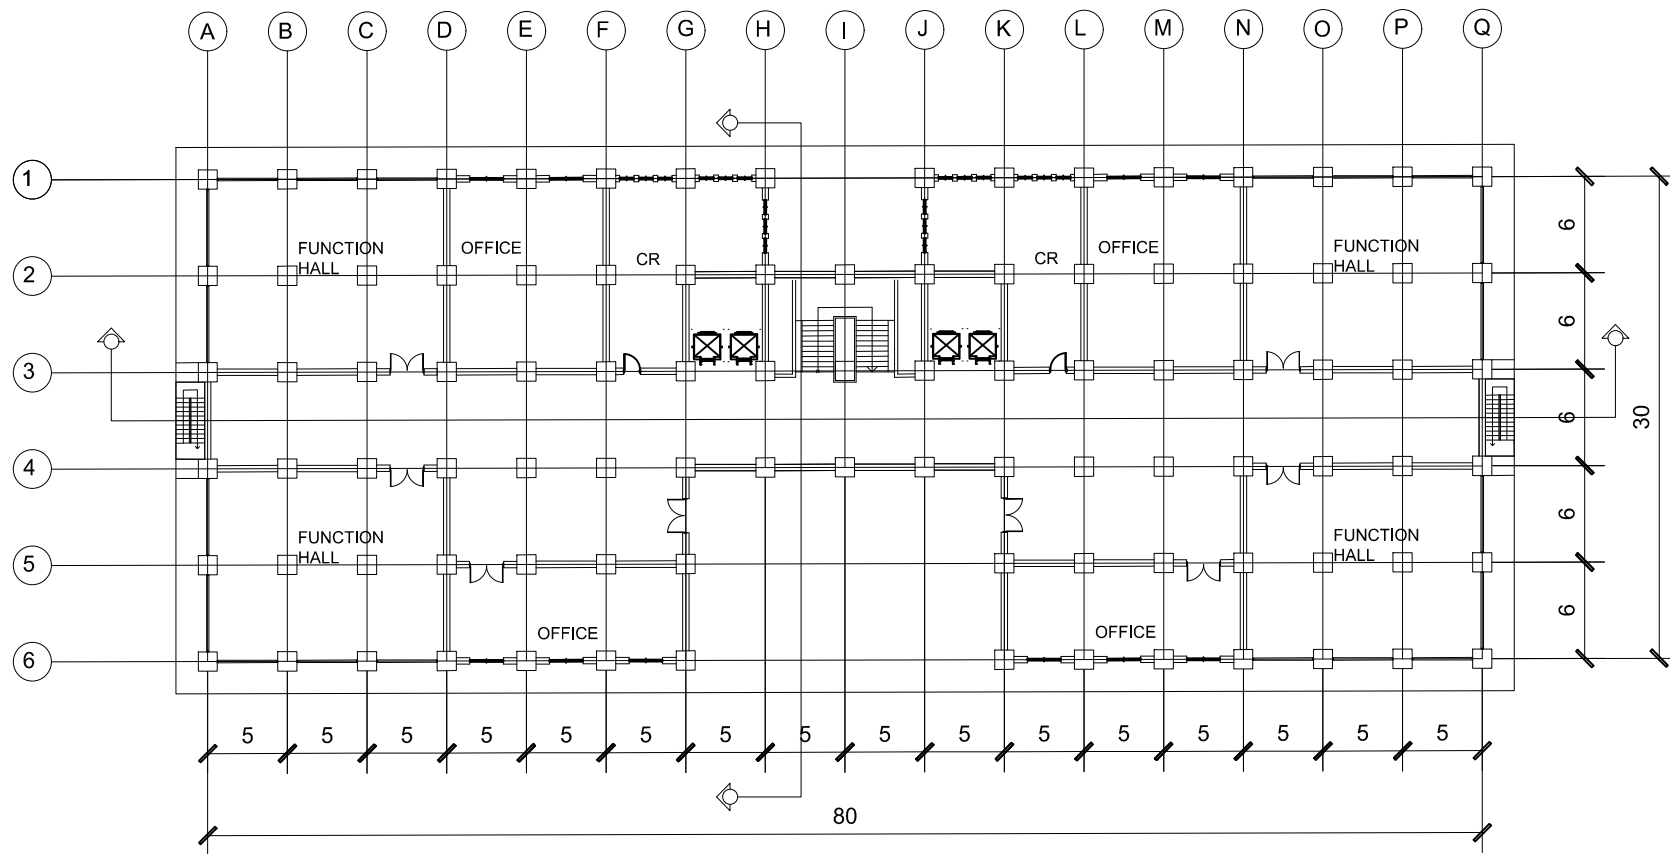

GROUND FLOOR PLAN

1:100



PROJECT:

PROPOSED 6-STOREY
MUNICIPAL BUILDING

LOCATION:

171 LAOAG - PAOAY RD, 2900
LAOG CITY, ILOCOS NORTE

PREPARED BY:

Ricki Lei D. Dela Rosa

BSCE IV-A

21-050147

OWNER:


ENGR. ARBIE MARIZ A. REVILLA


ARCHITECTURAL DRAWING

SHEET

A-2

4

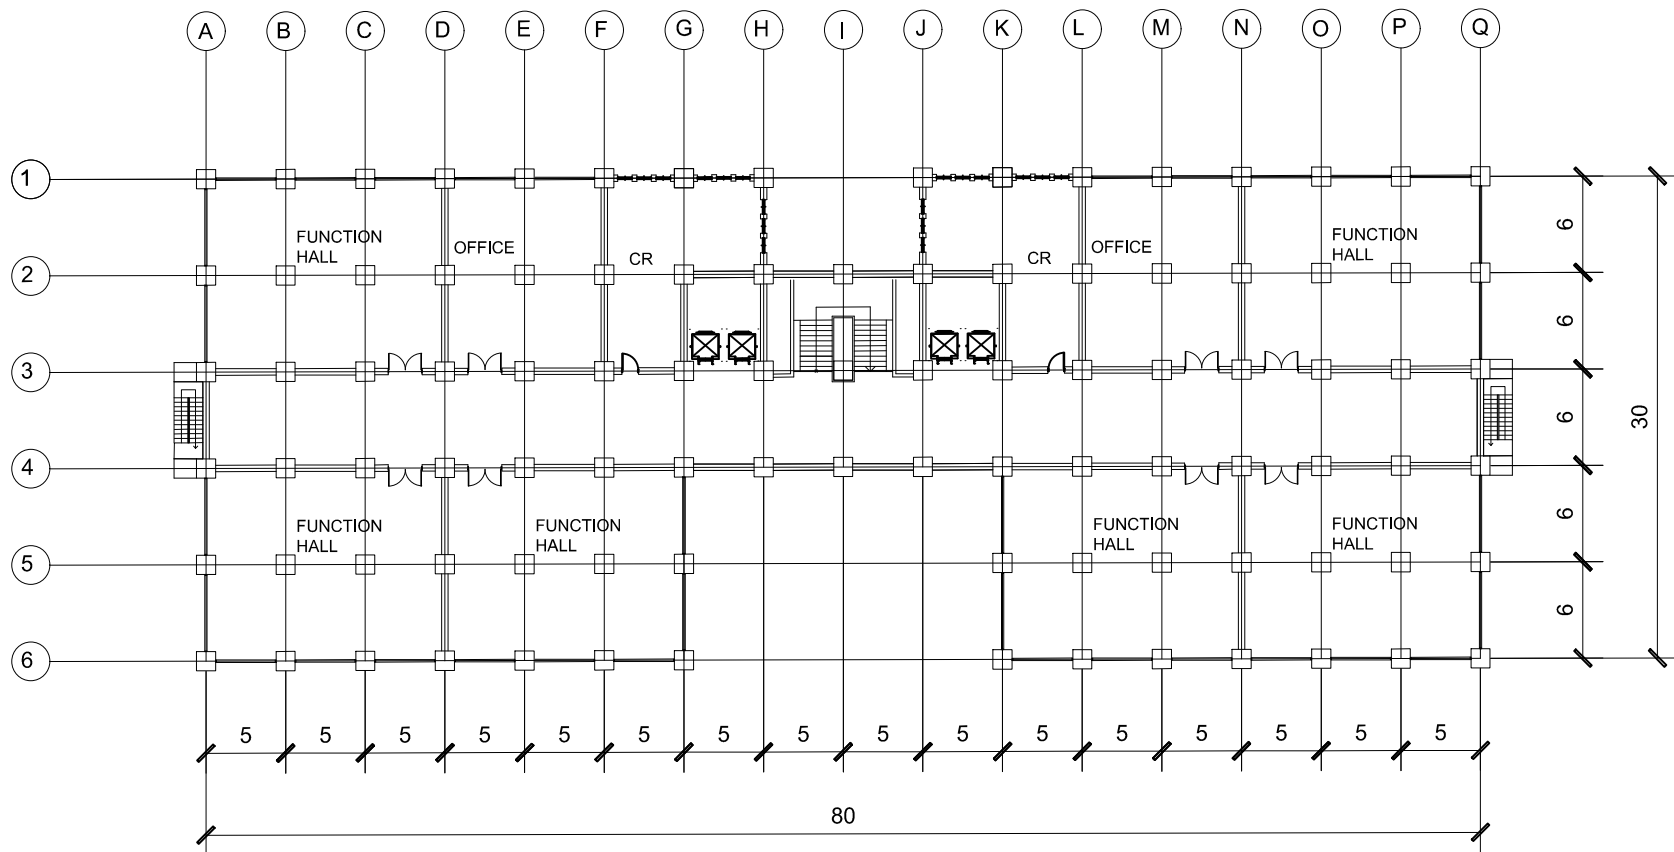

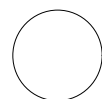 **SECOND FLOOR PLAN**
1:100



PROJECT:

PROPOSED 6-STOREY
MUNICIPAL BUILDING

LOCATION:

171 LAOAG - PAOAY RD, 2900
LAOG CITY, ILOCOS NORTE

PREPARED BY:

Ricki Lei D. Dela Rosa

BSCE IV-A

21-050147

OWNER:


ENGR. ARBIE MARIZ A. REVILLA

ARCHITECTURAL DRAWING

SHEET

A-2

5

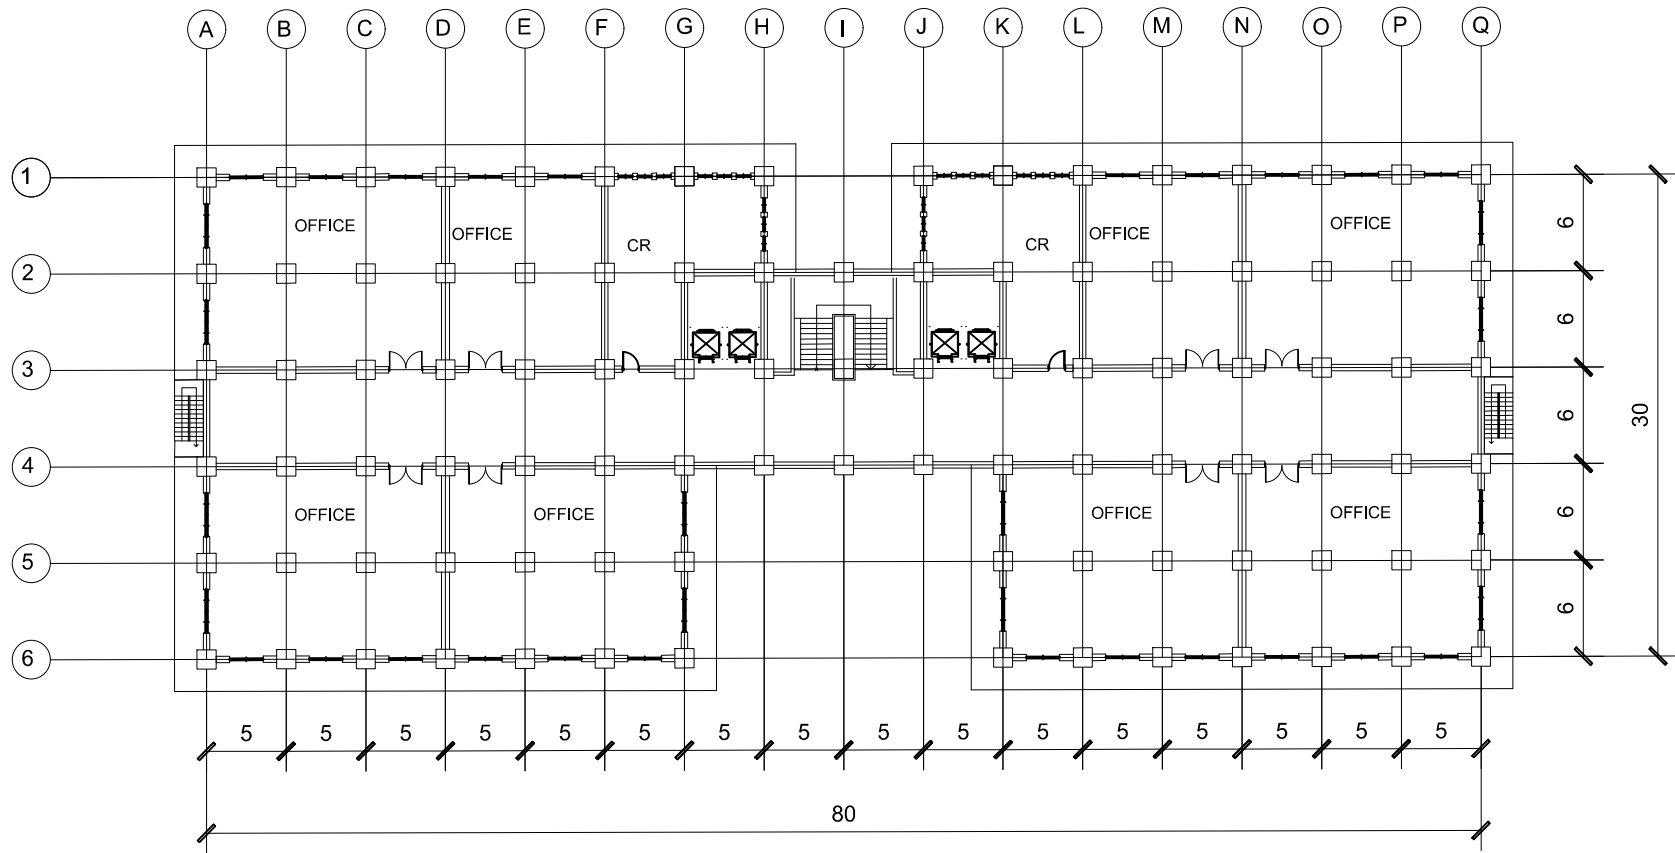

THIRD FLOOR PLAN

1:100



PROJECT:

PROPOSED 6-STOREY
MUNICIPAL BUILDING

LOCATION:

171 LAOAG - PAOAY RD, 2900
LAOG CITY, ILOCOS NORTE

PREPARED BY:

Ricki Lei D. Dela Rosa

BSCE IV-A

21-050147

OWNER:


ENGR. ARBIE MARIZ A. REVILLA

ARCHITECTURAL DRAWING

SHEET

A-2

6

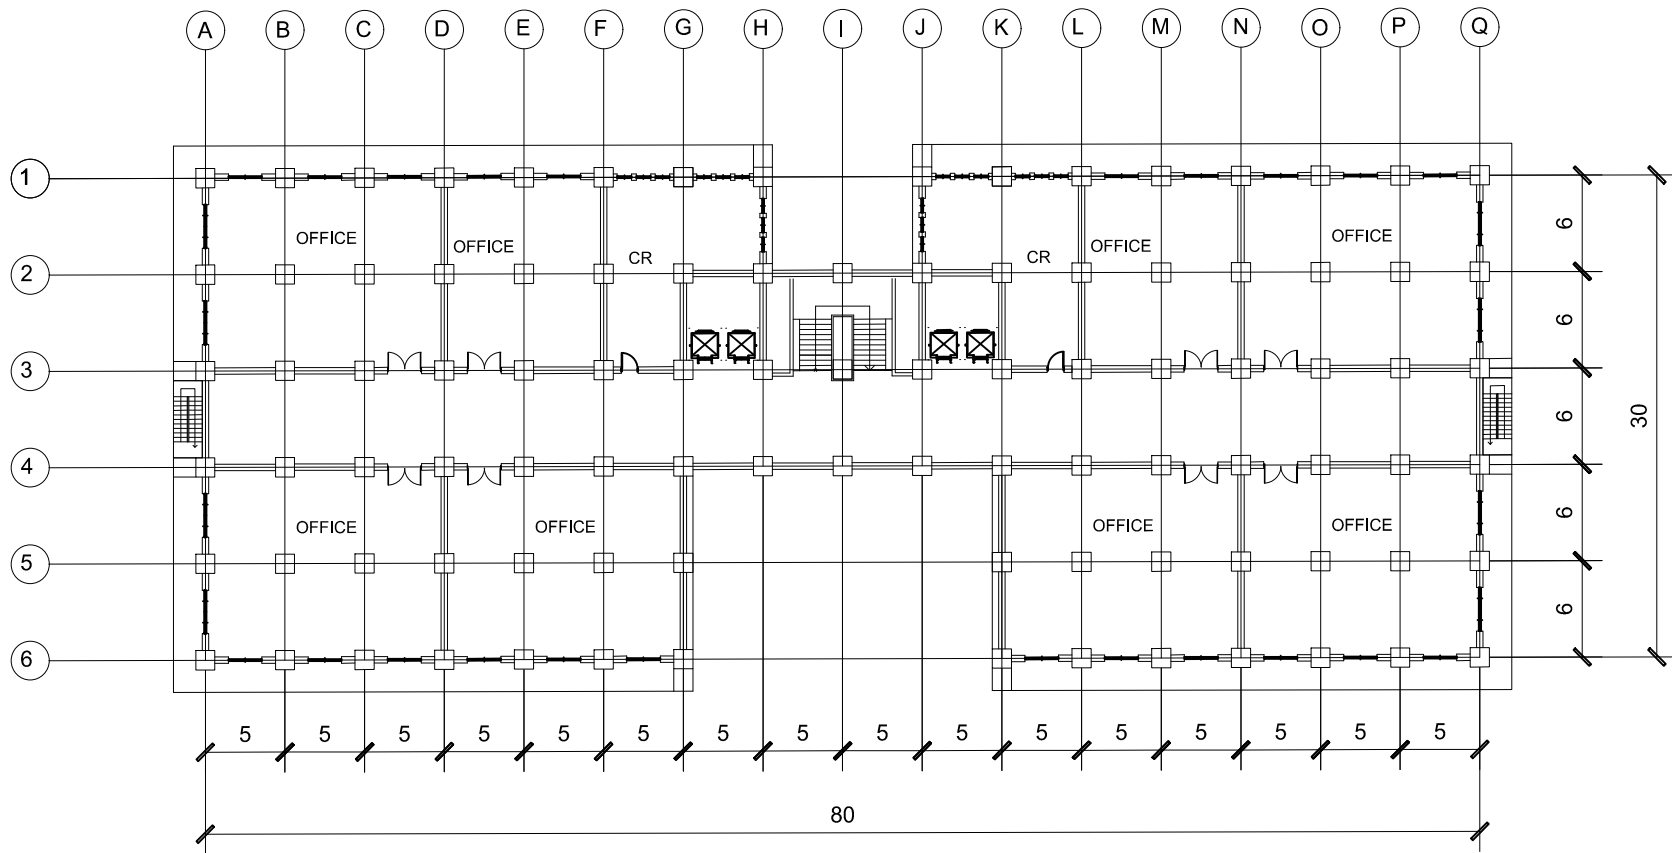

FOURTH FLOOR PLAN
1:100



PROJECT:

PROPOSED 6-STOREY
MUNICIPAL BUILDING

LOCATION:

171 LAOAG - PAOAY RD, 2900
LAOG CITY, ILOCOS NORTE

PREPARED BY:

Ricki Lei D. Dela Rosa

BSCE IV-A

21-050147

OWNER:


ENGR. ARBIE MARIZ A. REVILLA

ARCHITECTURAL DRAWING

SHEET

A-2

7

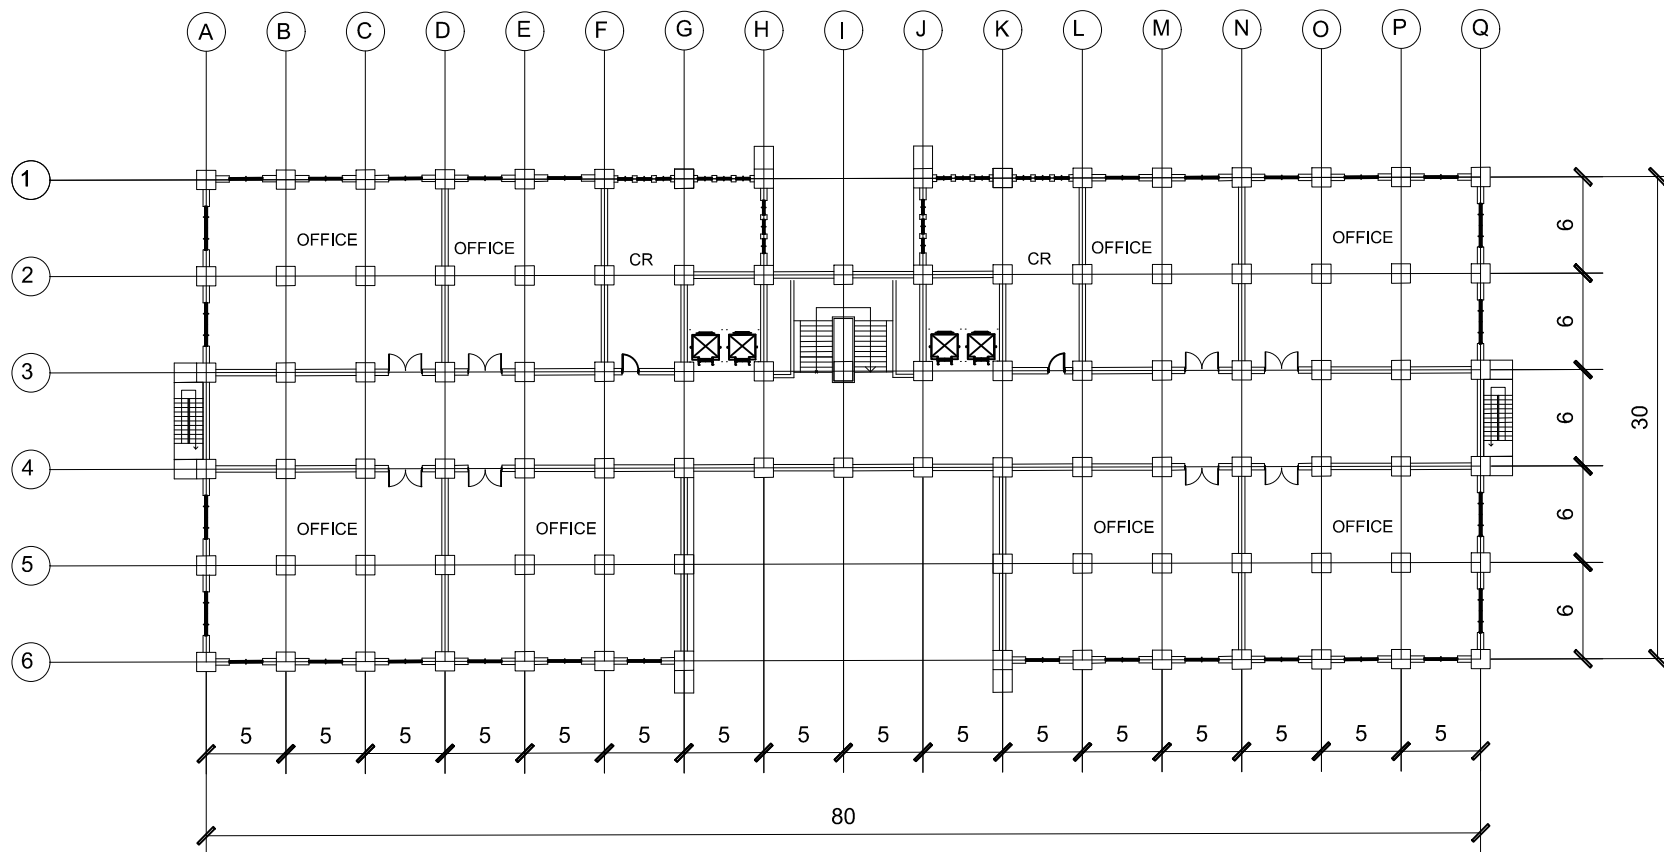

FIFTH FLOOR PLAN
1:100



PROJECT:

PROPOSED 6-STOREY
MUNICIPAL BUILDING

LOCATION:

171 LAOAG - PAOAY RD, 2900
LAOG CITY, ILOCOS NORTE

PREPARED BY:

Ricki Lei D. Dela Rosa

BSCE IV-A

21-050147

OWNER:

ENGR. ARBIE MARIZ A. REVILLA

ARCHITECTURAL DRAWING

SHEET

A-2

8



1:100



PROJECT:

PROPOSED 6-STOREY
MUNICIPAL BUILDING

LOCATION:

171 LAOAG - PAOAY RD, 2900
LAOG CITY, ILOCOS NORTE

PREPARED BY:

Ricki Lei D. Dela Rosa

BSCE IV-A

21-050147

OWNER:


ENGR. ARBIE MARIZ A. REVILLA

ARCHITECTURAL DRAWING

SHEET

A-2

9

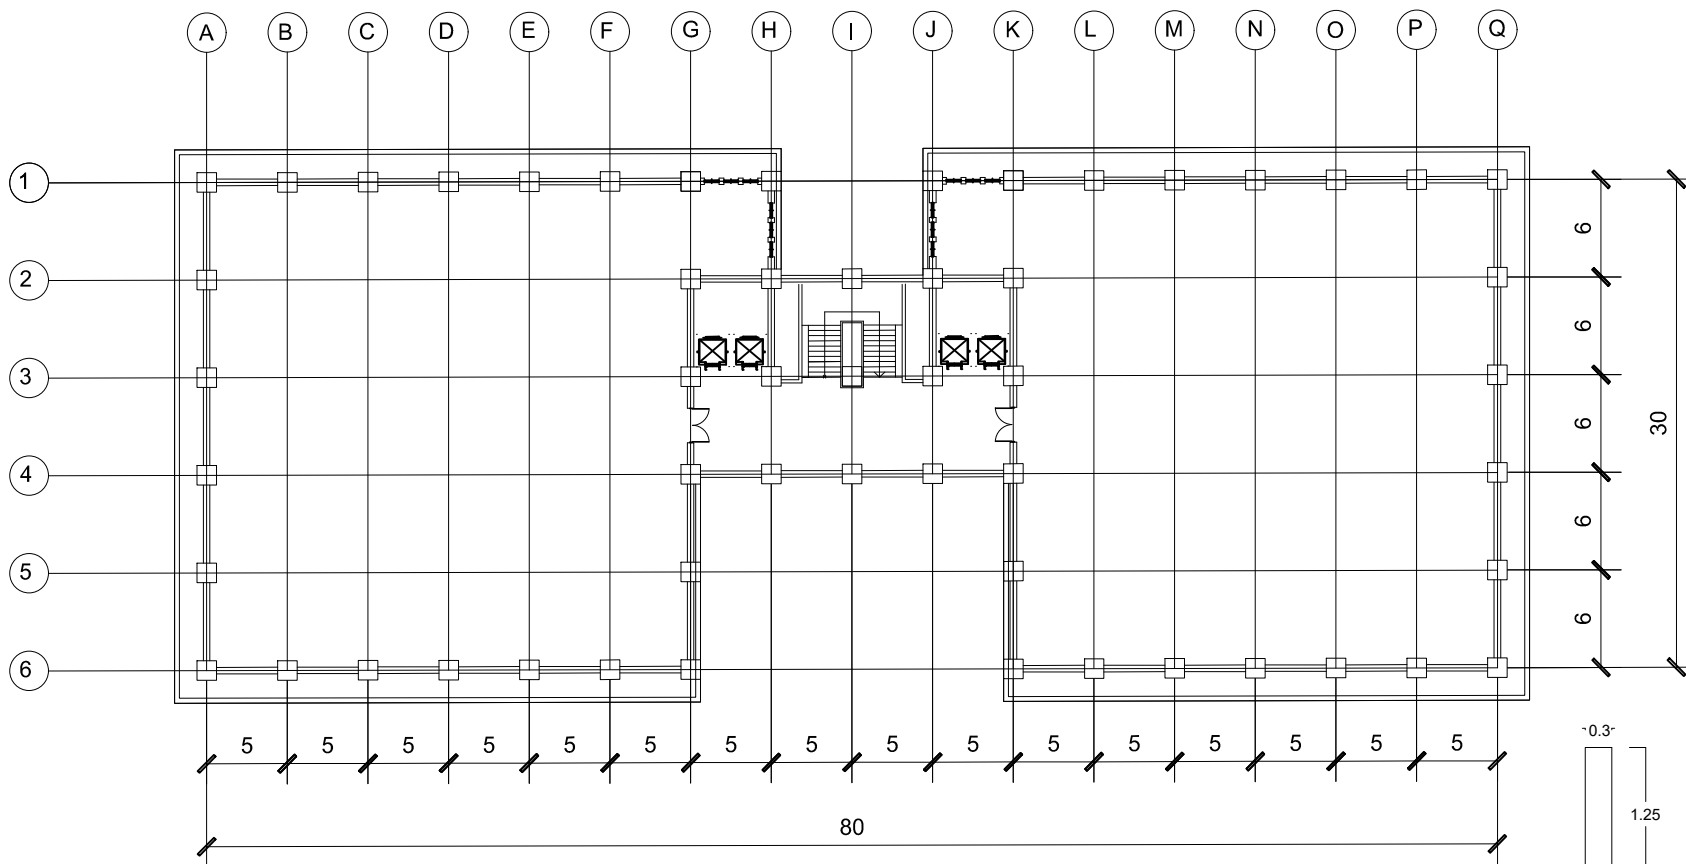

ROOF DECK PLAN

1:100

~0.3~	1.25
PARAPET WALL	SIZE (m)
	1.5m x 0.3m



PROJECT:

PROPOSED 6-STOREY
MUNICIPAL BUILDING

LOCATION:

171 LAOAG - PAOAY RD, 2900
LAOG CITY, ILOCOS NORTE

PREPARED BY:

Ricki Lei D. Dela Rosa

BSCE IV-A

21-050147

OWNER:

ENGR. ARBIE MARIZ A. REVILLA

ARCHITECTURAL DRAWING


SHEET

A-2

10



	PROJECT:	PREPARED BY:	OWNER:	A-3 11
	PROPOSED 6-STOREY MUNICIPAL BUILDING	Ricki Lei D. Dela Rosa	ENGR. ARBIE MARIZ A. REVILLA	
	LOCATION:	BSCE IV-A		
	171 LAOAG - PAOAY RD, 2900 LAOG CITY, ILOCOS NORTE	21-050147	ARCHITECTURAL DRAWING	

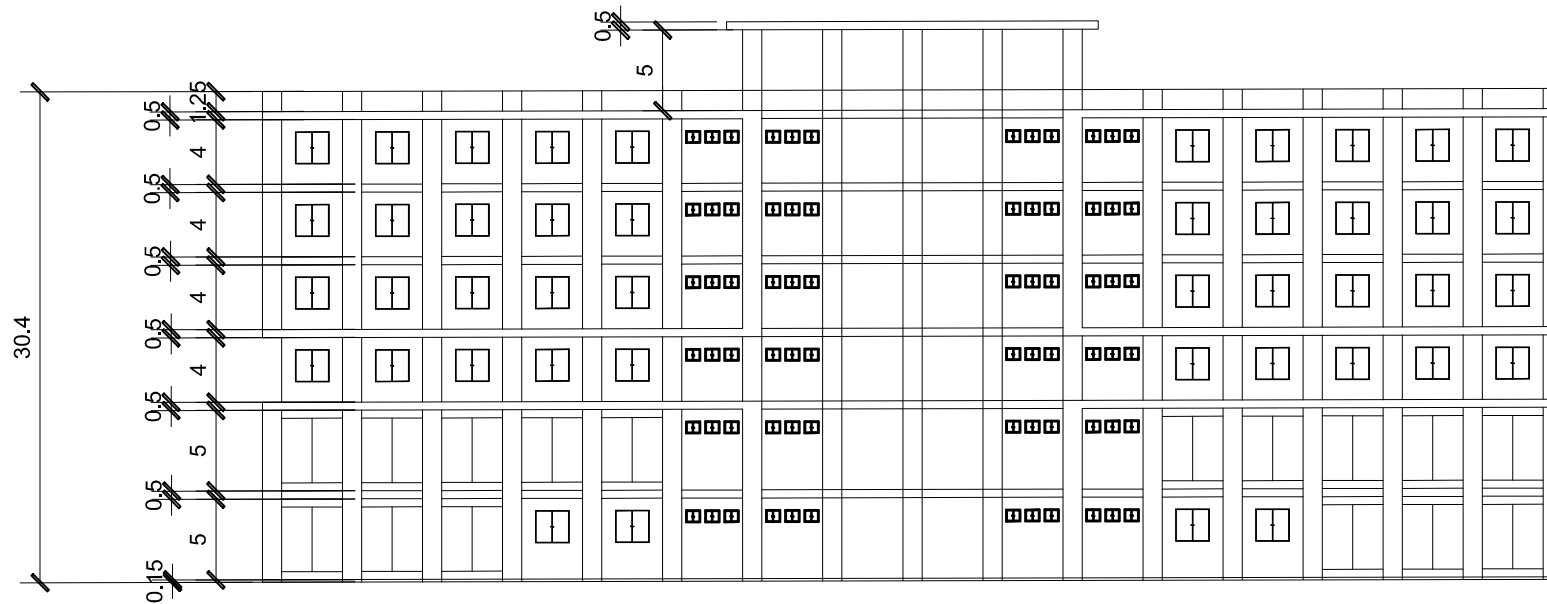

REAR ELEVATION

1:100



PROJECT:

PROPOSED 6-STOREY
MUNICIPAL BUILDING

LOCATION:

171 LAOAG - PAOAY RD, 2900
LAOG CITY, ILOCOS NORTE

PREPARED BY:

Ricki Lei D. Dela Rosa

BSCE IV-A

21-050147

OWNER:


ENGR. ARBIE MARIZ A. REVILLA

ARCHITECTURAL DRAWING

SHEET

A-3


12

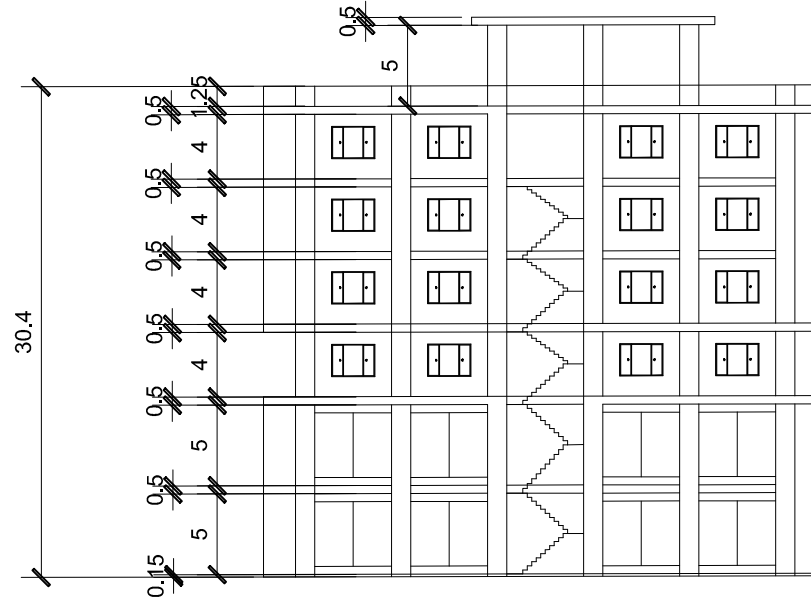

○ LEFT SIDE ELEVATION
1:100



PROJECT:	PREPARED BY:	OWNER:	SHEET
PROPOSED 6-STOREY MUNICIPAL BUILDING	Ricki Lei D. Dela Rosa	ENGR. ARBIE MARIZ A. REVILLA	A-3 13
LOCATION:	BSCE IV-A		
171 LAOAG - PAOAY RD, 2900 LAOG CITY, ILOCOS NORTE	21-050147	ARCHITECTURAL DRAWING	

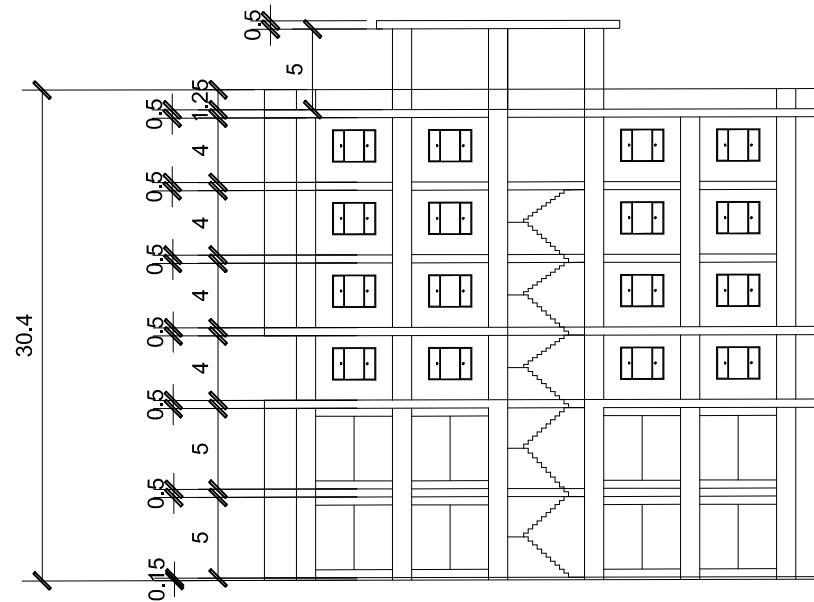

RIGHT SIDE ELEVATION
1:100



PROJECT:

PROPOSED 6-STOREY
MUNICIPAL BUILDING

LOCATION:

171 LAOAG - PAOAY RD, 2900
LAOG CITY, ILOCOS NORTE

PREPARED BY:

Ricki Lei D. Dela Rosa

BSCE IV-A

21-050147

OWNER:


ENGR. ARBIE MARIZ A. REVILLA

ARCHITECTURAL DRAWING

SHEET

A-3

14

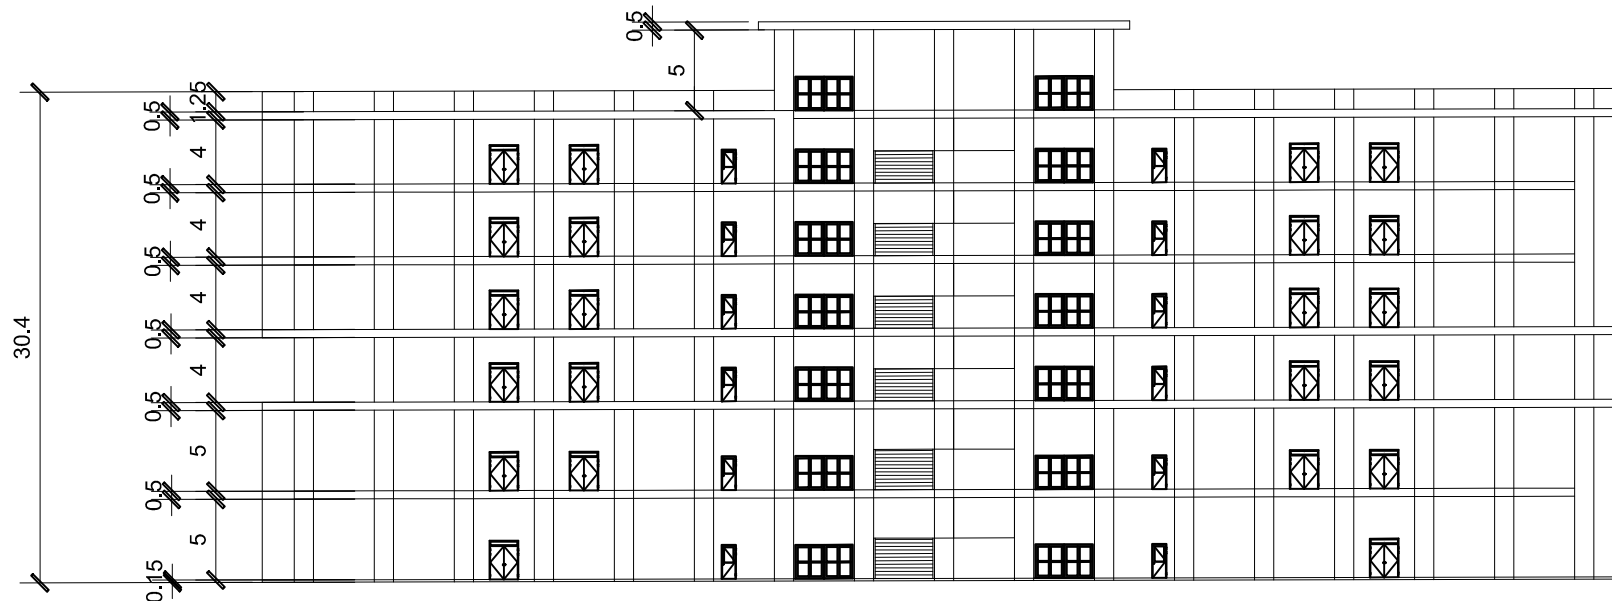

LONGITUDINAL CROSS SECTION

1:100



PROJECT:

PROPOSED 6-STOREY
MUNICIPAL BUILDING

LOCATION:

171 LAOAG - PAOAY RD, 2900
LAOG CITY, ILOCOS NORTE

PREPARED BY:

Ricki Lei D. Dela Rosa

BSCE IV-A

21-050147

OWNER:


ENGR. ARBIE MARIZ A. REVILLA

ARCHITECTURAL DRAWING

SHEET

A-3

15

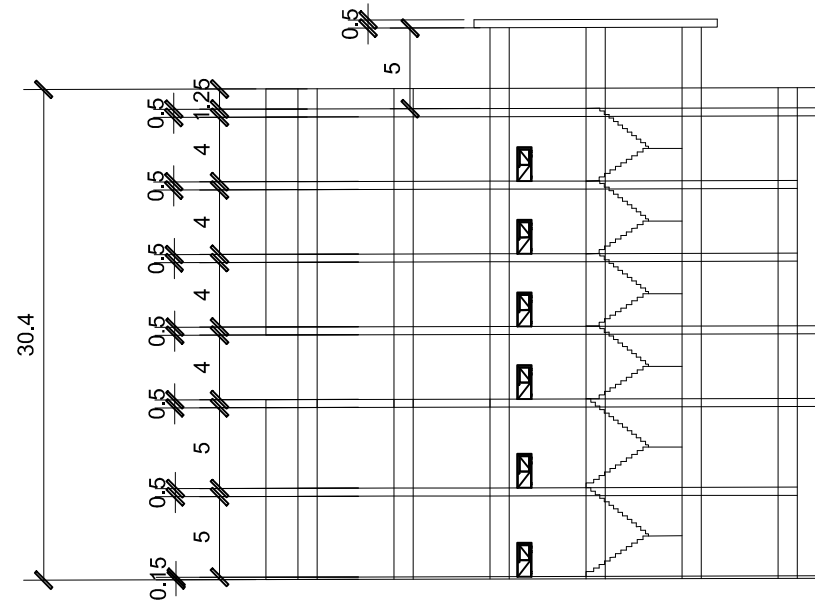

CROSS SECTION

1:100



PROJECT:

PROPOSED 6-STOREY
MUNICIPAL BUILDING

LOCATION:

171 LAOAG - PAOAY RD, 2900
LAOG CITY, ILOCOS NORTE

PREPARED BY:

Ricki Lei D. Dela Rosa

BSCE IV-A

21-050147

OWNER:


ENGR. ARBIE MARIZ A. REVILLA

ARCHITECTURAL DRAWING

SHEET

A-3

16

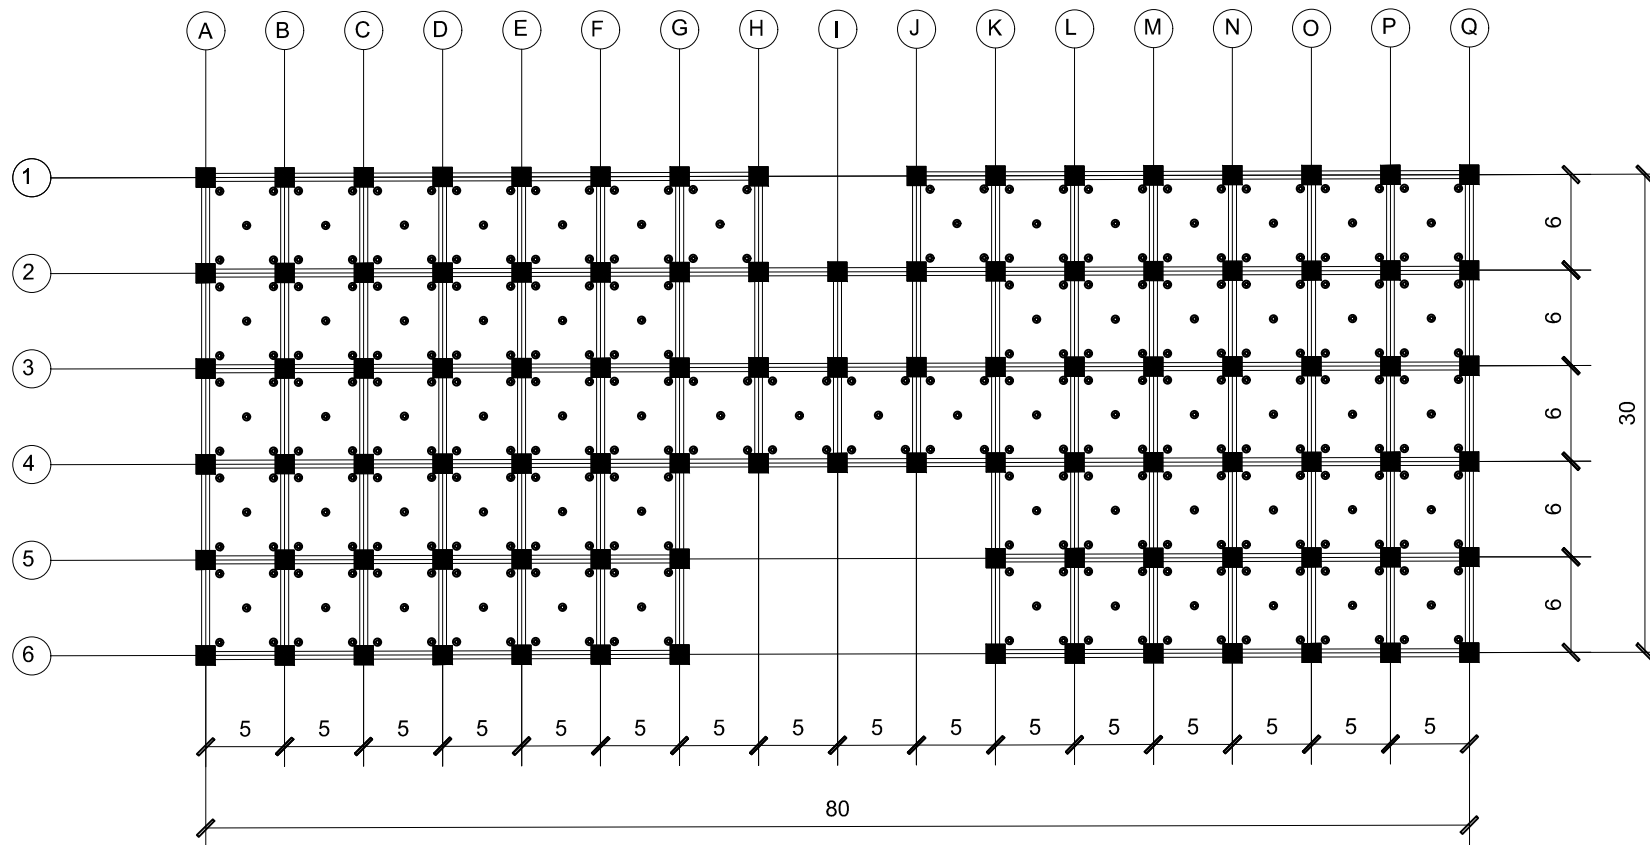

GROUND FLOOR CEILING PLAN
1:100



PROJECT:

PROPOSED 6-STOREY
MUNICIPAL BUILDING

LOCATION:

171 LAOAG - PAOAY RD, 2900
LAOG CITY, ILOCOS NORTE

PREPARED BY:

Ricki Lei D. Dela Rosa

BSCE IV-A

21-050147

OWNER:



ENGR. ARBIE MARIZ A. REVILLA

ARCHITECTURAL DRAWING

SHEET

A-4

17

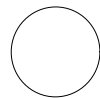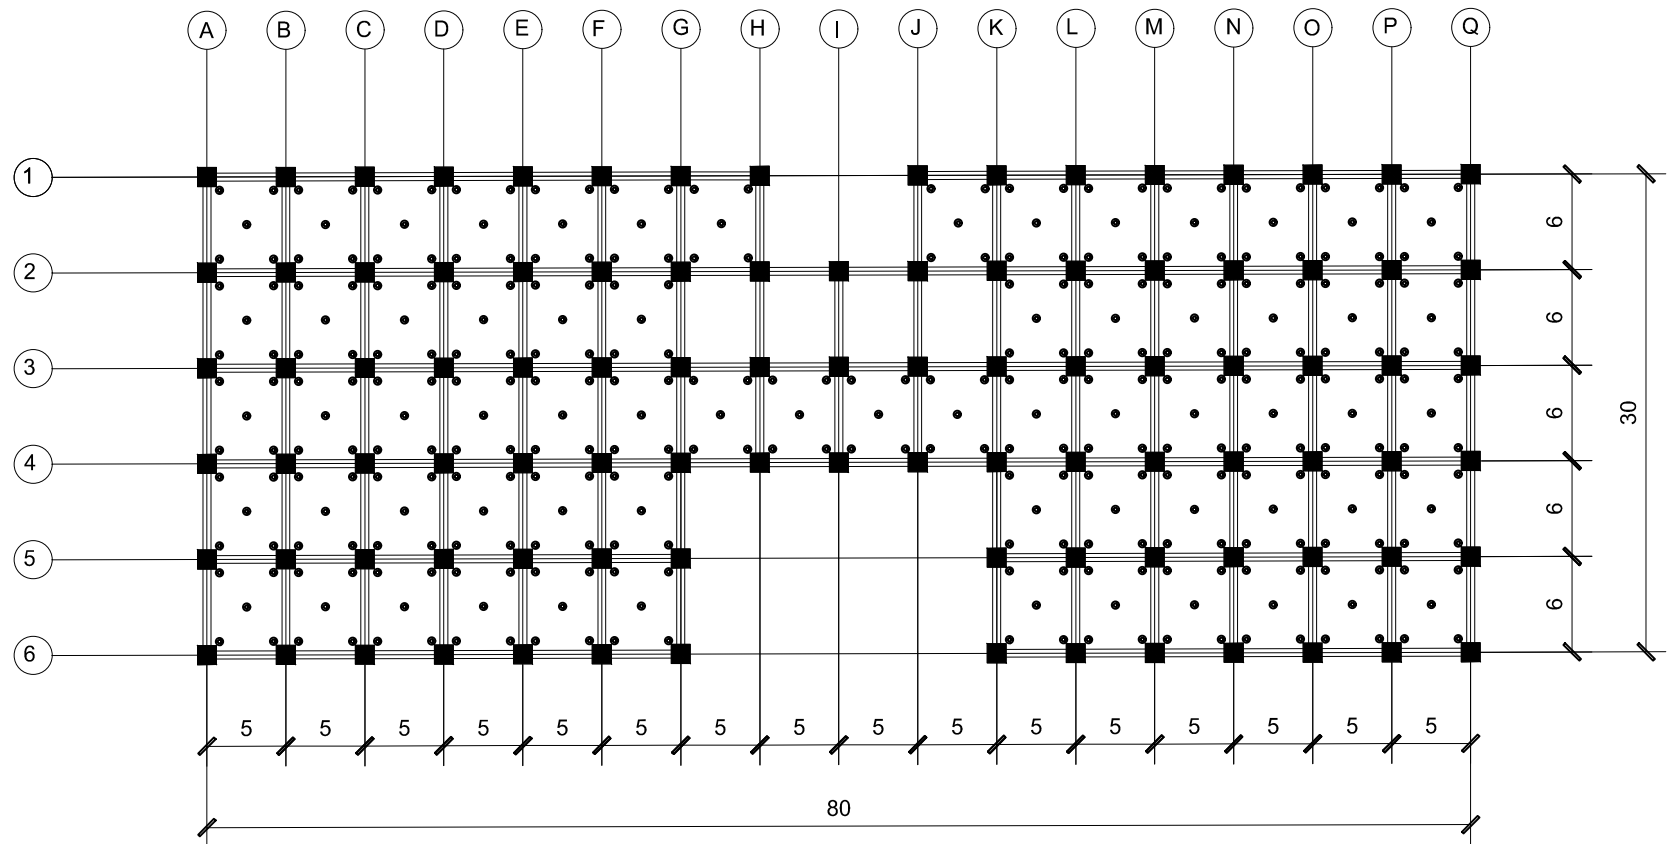

SECOND FLOOR CEILING PLAN

1:100



PROJECT:

PROPOSED 6-STOREY
MUNICIPAL BUILDING

LOCATION:

171 LAOAG - PAOAY RD, 2900
LAOG CITY, ILOCOS NORTE

PREPARED BY:

Ricki Lei D. Dela Rosa

BSCE IV-A

21-050147

OWNER:


ENGR. ARBIE MARIZ A. REVILLA

ARCHITECTURAL DRAWING

SHEET

A-4

18

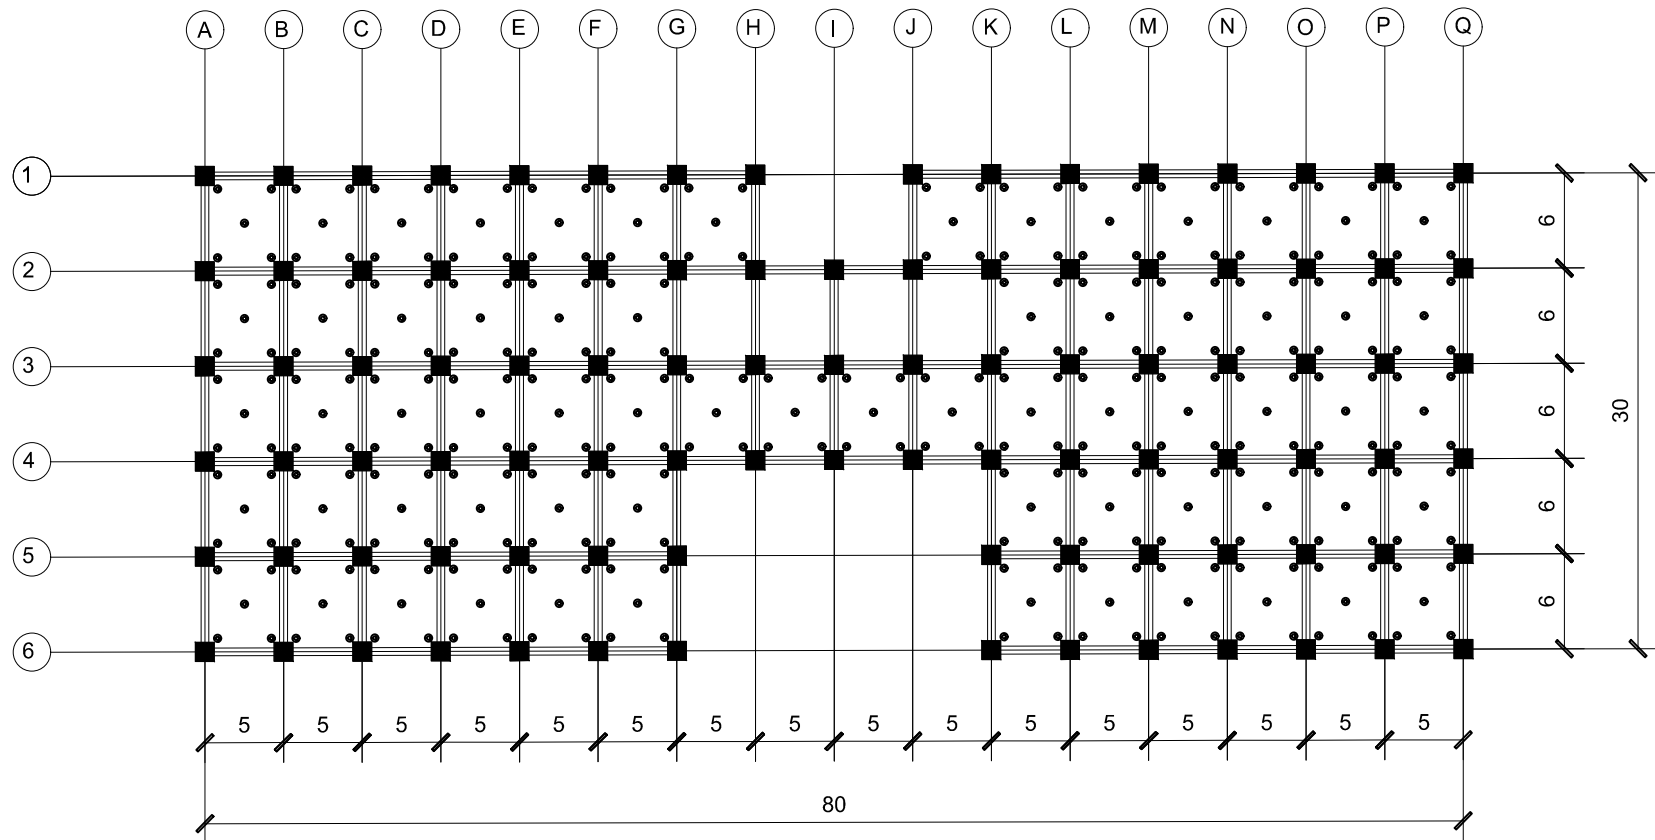

THIRD FLOOR CEILING PLAN

1:100



PROJECT:

PROPOSED 6-STOREY
MUNICIPAL BUILDING

LOCATION:

171 LAOAG - PAOAY RD, 2900
LAOG CITY, ILOCOS NORTE

PREPARED BY:

Ricki Lei D. Dela Rosa

BSCE IV-A

21-050147

OWNER:


ENGR. ARBIE MARIZ A. REVILLA

ARCHITECTURAL DRAWING

SHEET

A-4

19

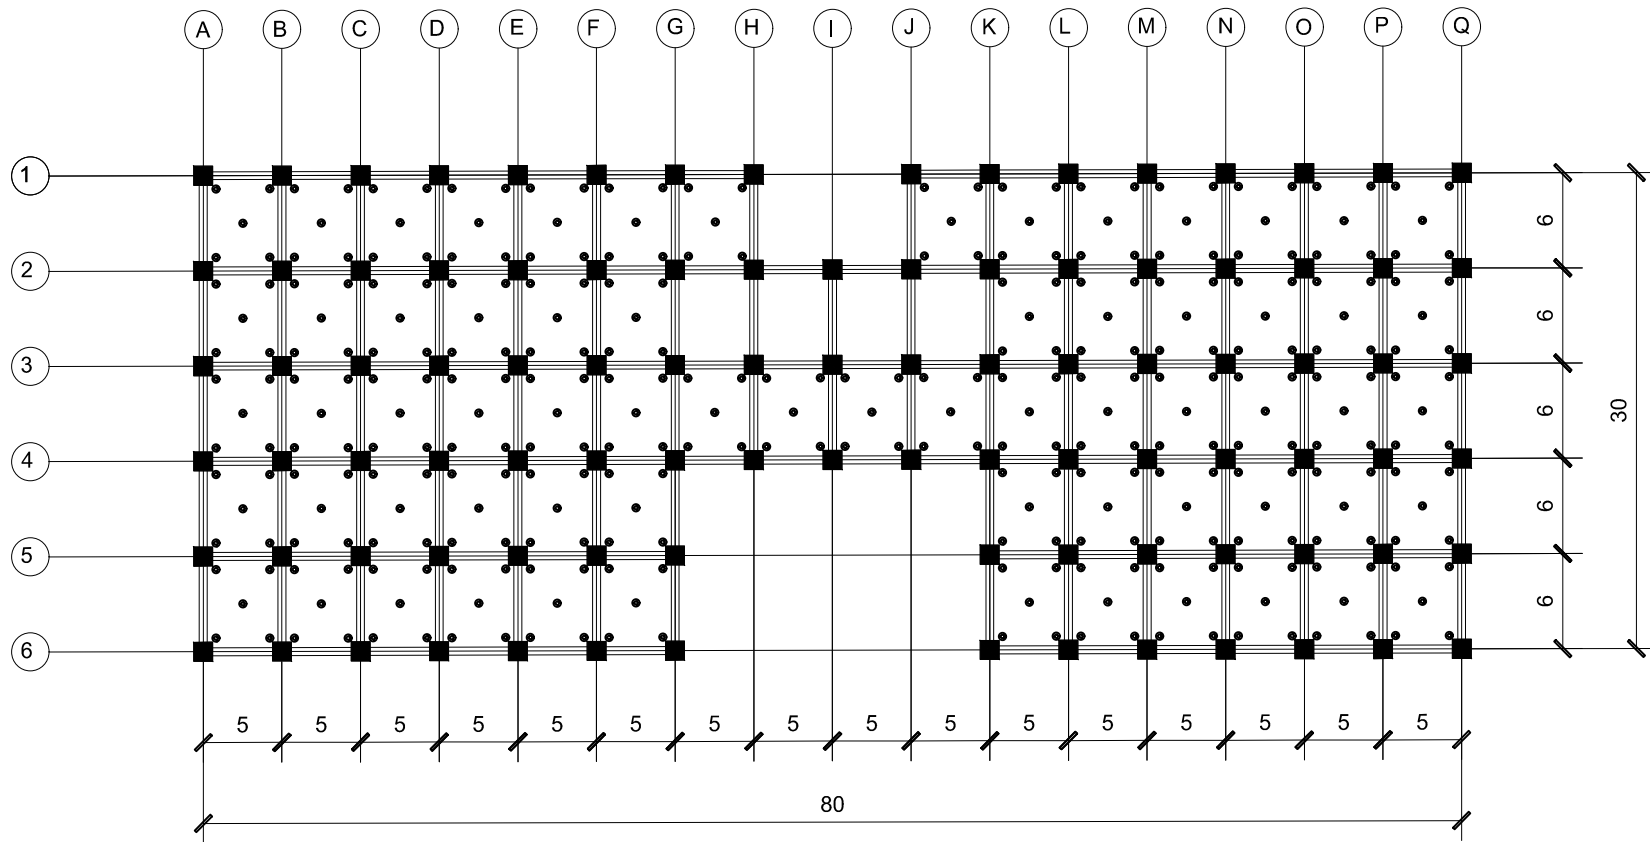

FOURTH FLOOR CEILING PLAN

1:100



PROJECT:

PROPOSED 6-STOREY
MUNICIPAL BUILDING

LOCATION:

171 LAOAG - PAOAY RD, 2900
LAOG CITY, ILOCOS NORTE

PREPARED BY:

Ricki Lei D. Dela Rosa

BSCE IV-A

21-050147

OWNER:


ENGR. ARBIE MARIZ A. REVILLA


ARCHITECTURAL DRAWING

SHEET

A-4

20

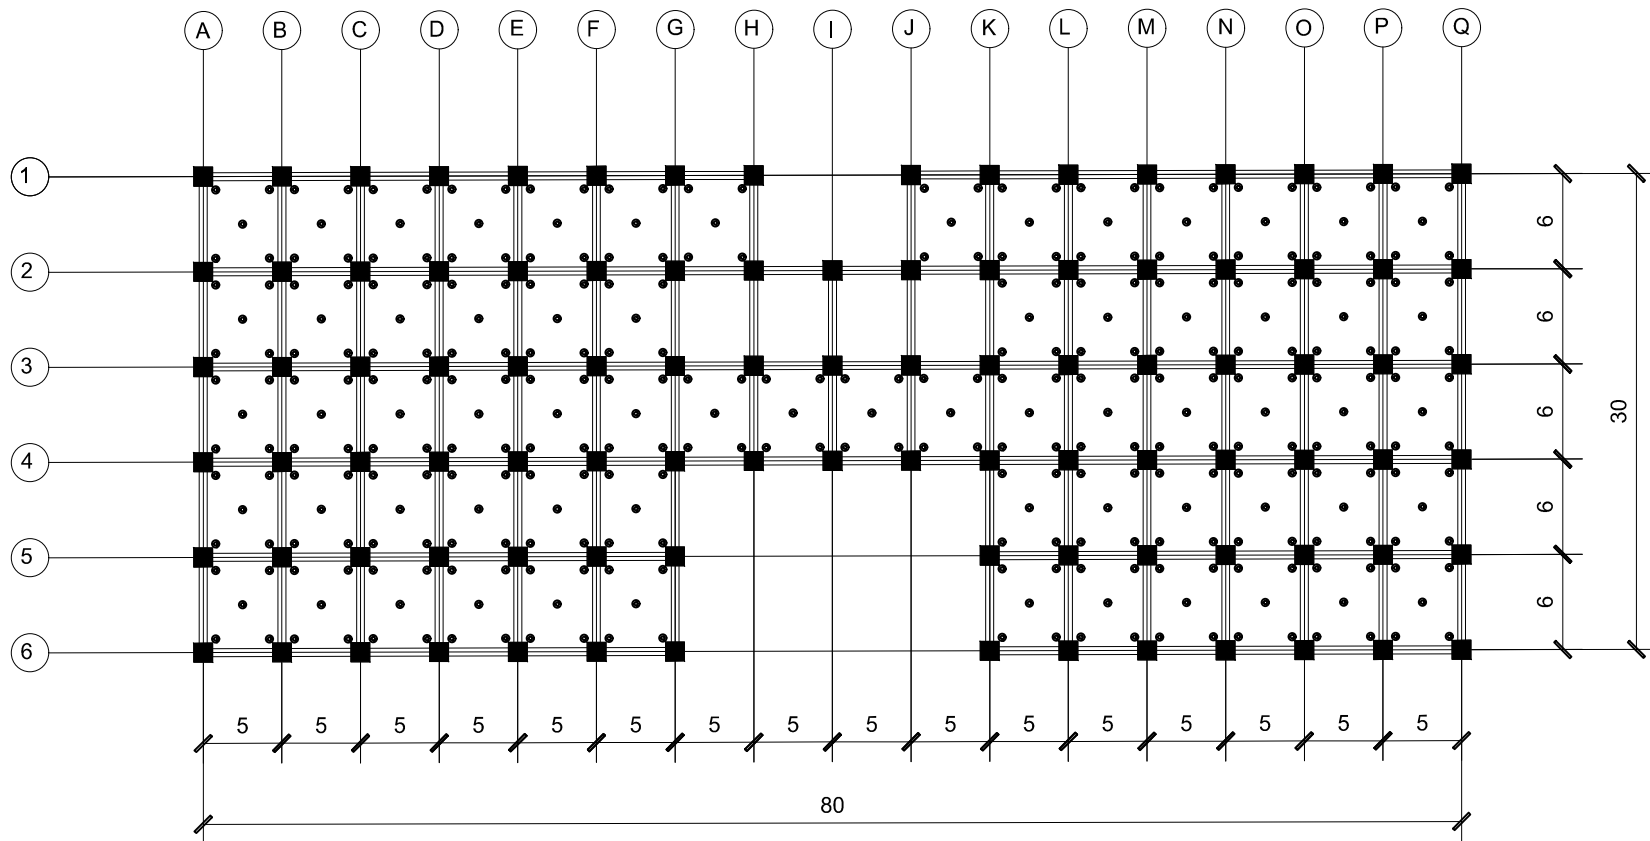

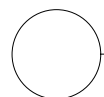 FIFTH FLOOR CEILING PLAN
1:100



PROJECT:

PROPOSED 6-STOREY
MUNICIPAL BUILDING

LOCATION:

171 LAOAG - PAOAY RD, 2900
LAOG CITY, ILOCOS NORTE

PREPARED BY:

Ricki Lei D. Dela Rosa

BSCE IV-A

21-050147

OWNER:


ENGR. ARBIE MARIZ A. REVILLA

ARCHITECTURAL DRAWING

SHEET

A-4

21

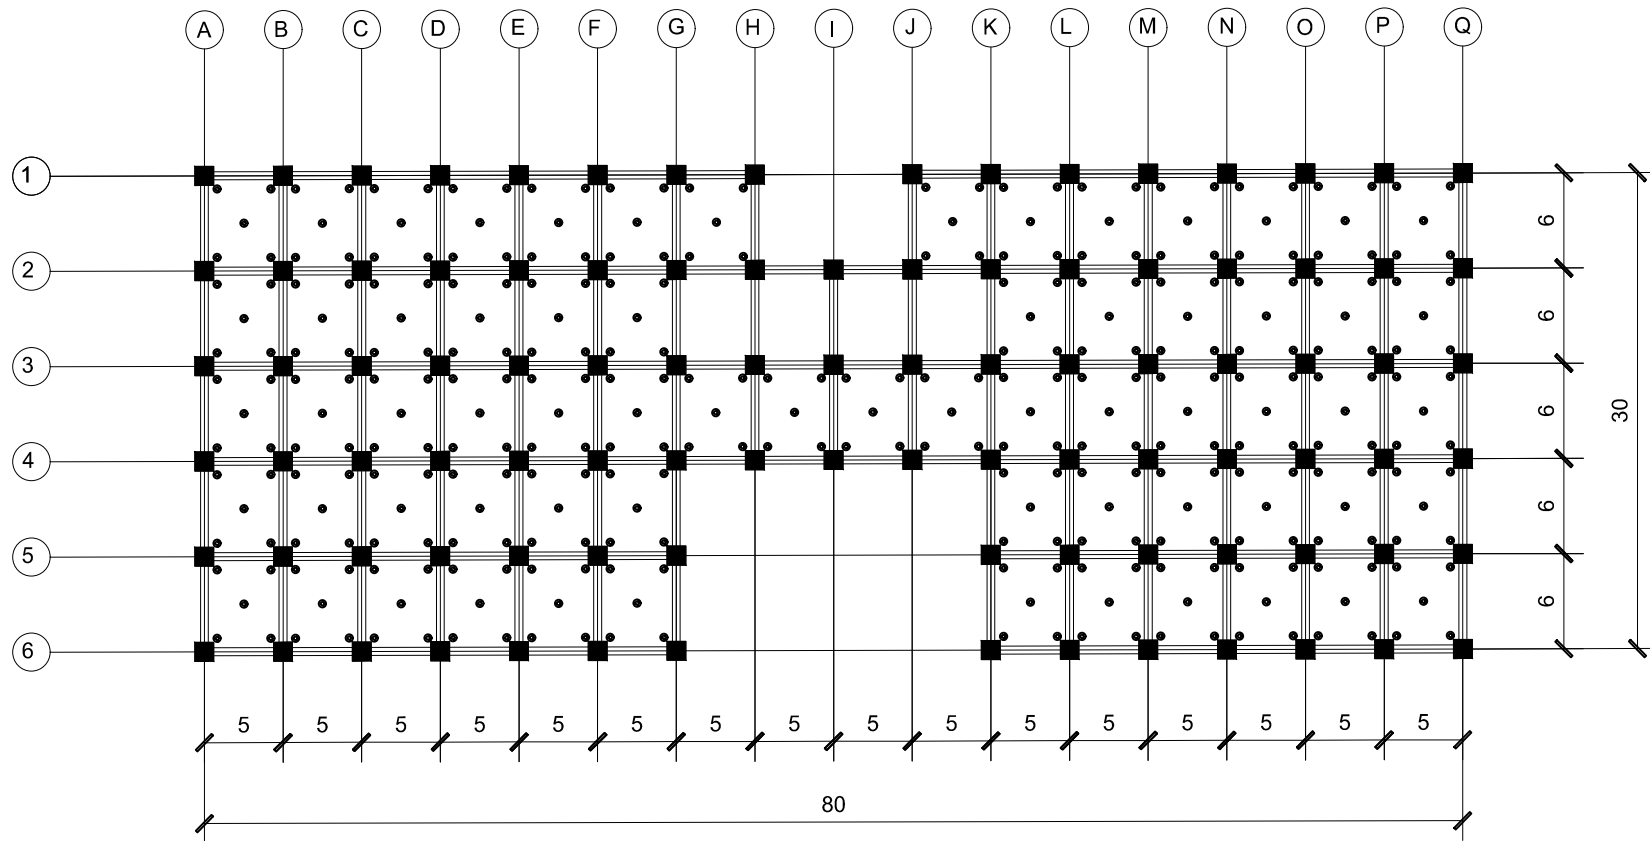

SIXTH FLOOR CEILING PLAN

1:100



PROJECT:

PROPOSED 6-STOREY
MUNICIPAL BUILDING

LOCATION:

171 LAOAG - PAOAY RD, 2900
LAOG CITY, ILOCOS NORTE

PREPARED BY:

Ricki Lei D. Dela Rosa

BSCE IV-A

21-050147

OWNER:




ENGR. ARBIE MARIZ A. REVILLA

ARCHITECTURAL DRAWING





SHEET

A-4

22

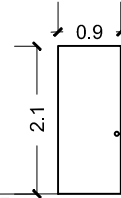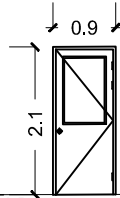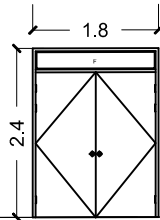



LOCATION	FRONT DOOR, OFFICE DOOR, FUNCTION HALL	T & B	FIRE EXIT
NO. OF SET:	50 SET	12 SET	12 SET
MATERIAL	NARRA WOOD	PVC	STEEL

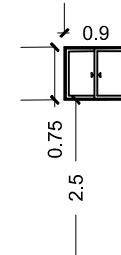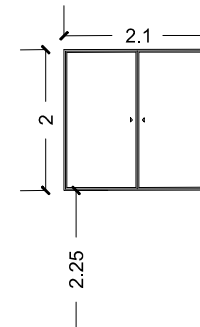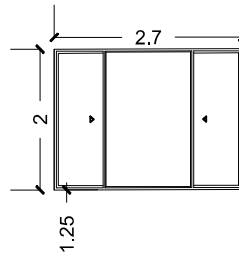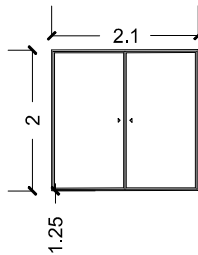

	ALUMINUM SLIDING WINDOW	ALUMINUM SLIDING WINDOW	ALUMINUM SLIDING WINDOW	ALUMINUM AWNING WINDOW
LOCATION	OFFICE, FUNCTION HALL	OFFICE, FUNCTION HALL	FIRST FLOOR OFFICE	T & B
NO. OF SET:	88 SET	32 SETS	10 SET	36 SET



PROJECT:	PREPARED BY:	OWNER:	SHEET
PROPOSED 6-STOREY MUNICIPAL BUILDING	Ricki Lei D. Dela Rosa	ENGR. ARBIE MARIZ A. REVILLA	A-4 23
LOCATION:	BSCE IV-A		
171 LAOAG - PAOAY RD, 2900 LAOG CITY, ILOCOS NORTE	21-050147	ARCHITECTURAL DRAWING	

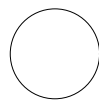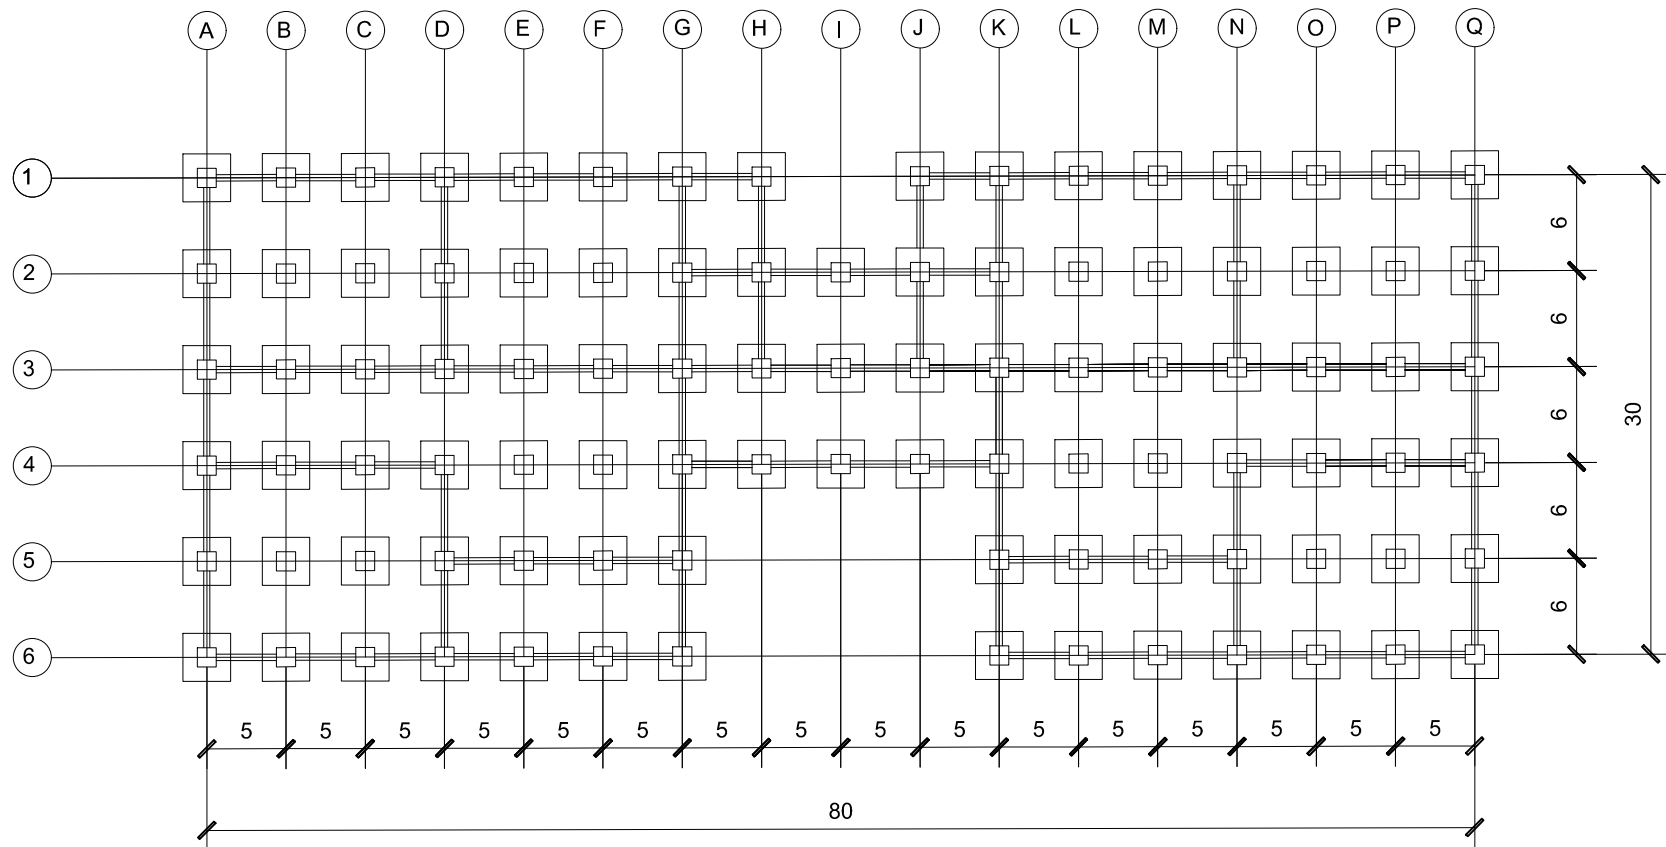

FOUNDATION PLAN

1:100



PROJECT:

**PROPOSED 6-STOREY
MUNICIPAL BUILDING**

LOCATION:

**171 LAOAG - PAOAY RD, 2900
LAOG CITY, ILOCOS NORTE**

PREPARED BY:

Ricki Lei D. Dela Rosa

BSCE IV-A

21-050147

OWNER:


ENGR. ARBIE MARIZ A. REVILLA

ARCHITECTURAL DRAWING

SHEET

S-1

24

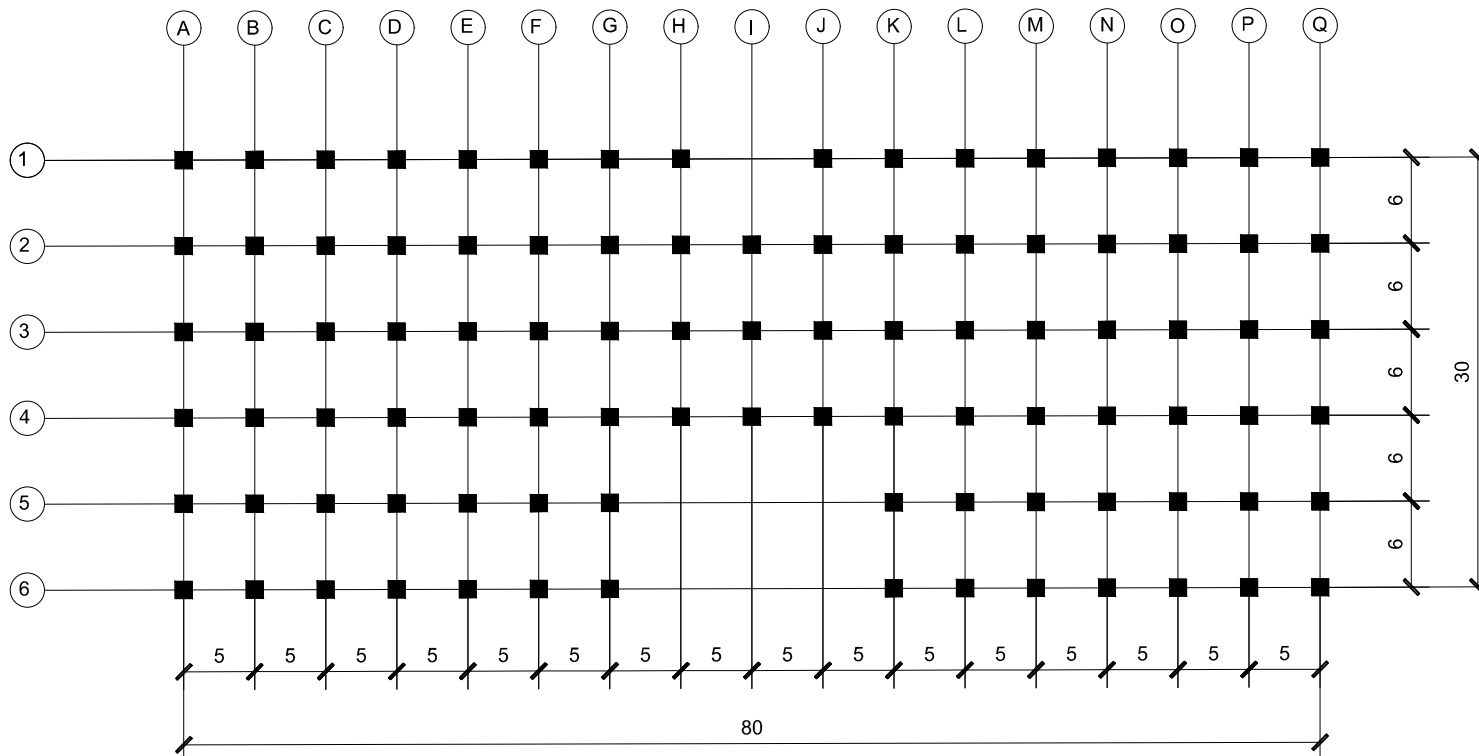

COLUMN TYPE	SIZE (m)
C1	1.2m X 1.2m

COLUMN LAYOUT AND SCHEDULE
1:100



PROJECT:

PROPOSED 6-STOREY
MUNICIPAL BUILDING

LOCATION:

171 LAOAG - PAOAY RD, 2900
LAOG CITY, ILOCOS NORTE

PREPARED BY:

Ricki Lei D. Dela Rosa

BSCE IV-A

21-050147

OWNER:


ENGR. ARBIE MARIZ A. REVILLA

ARCHITECTURAL DRAWING

SHEET

S-2

25

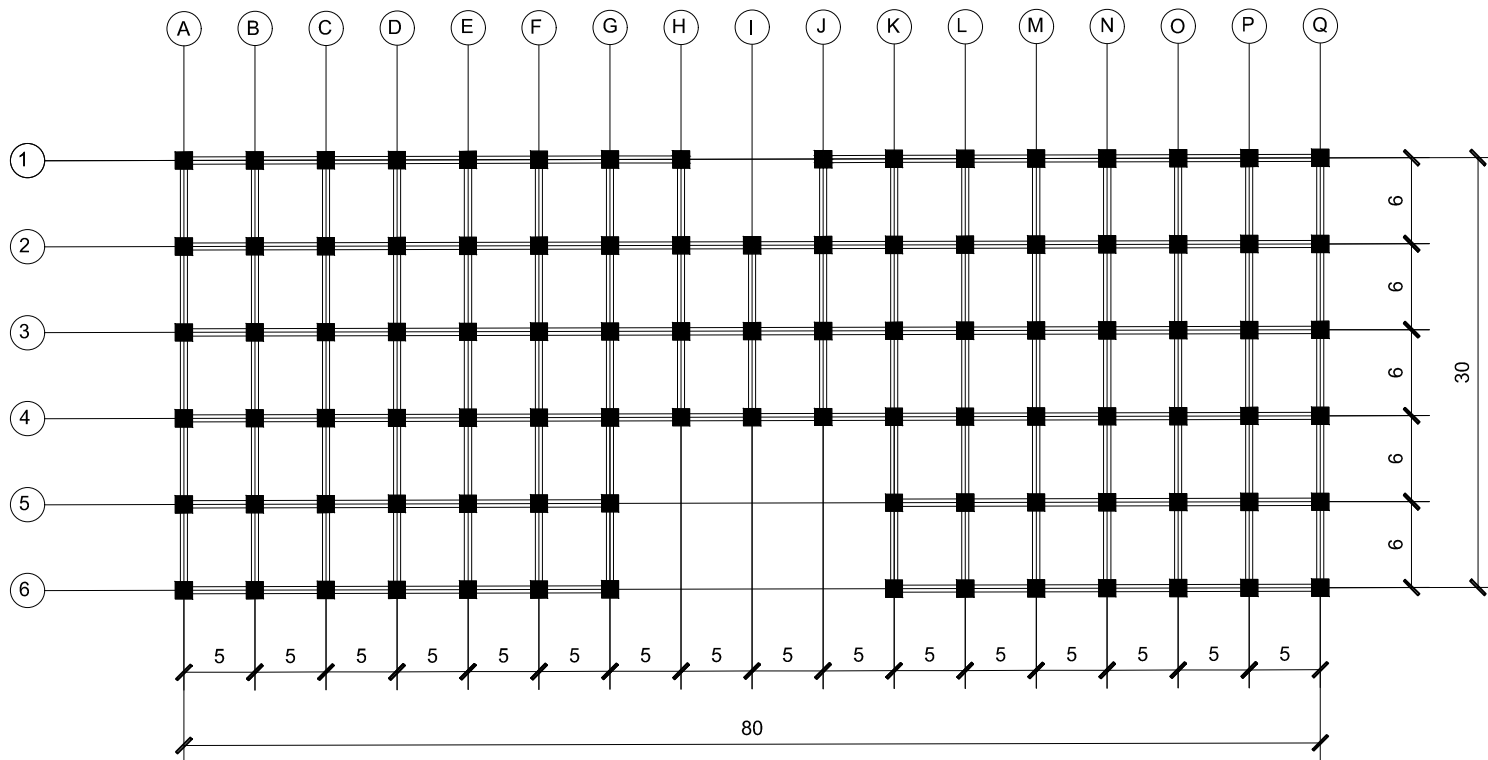

BEAM TYPE	SIZE (m)	LENGTH (m)
L1B1	0.5m X 0.6m	5m
L1B2	0.5m X 0.6m	6m
L2B1	0.5m X 0.6m	5m
L2B2	0.5m X 0.6m	6m
L3B1	0.5m X 0.6m	5m
L3B2	0.5m X 0.6m	6m
L4B1	0.5m X 0.6m	5m
L4B2	0.5m X 0.6m	6m
L5B1	0.5m X 0.6m	5m
L5B2	0.5m X 0.6m	6m
L6B1	0.5m X 0.6m	5m
L6B2	0.5m X 0.6m	6m

BEAM LAYOUT AND SCHEDULE

1:100



PROJECT:

PROPOSED 6-STOREY
MUNICIPAL BUILDING

LOCATION:

171 LAOAG - PAOAY RD, 2900
LAOG CITY, ILOCOS NORTE

PREPARED BY:

Ricki Lei D. Dela Rosa

BSCE IV-A

21-050147

OWNER:



ENGR. ARBIE MARIZ A. REVILLA

ARCHITECTURAL DRAWING

SHEET

S-3

26

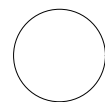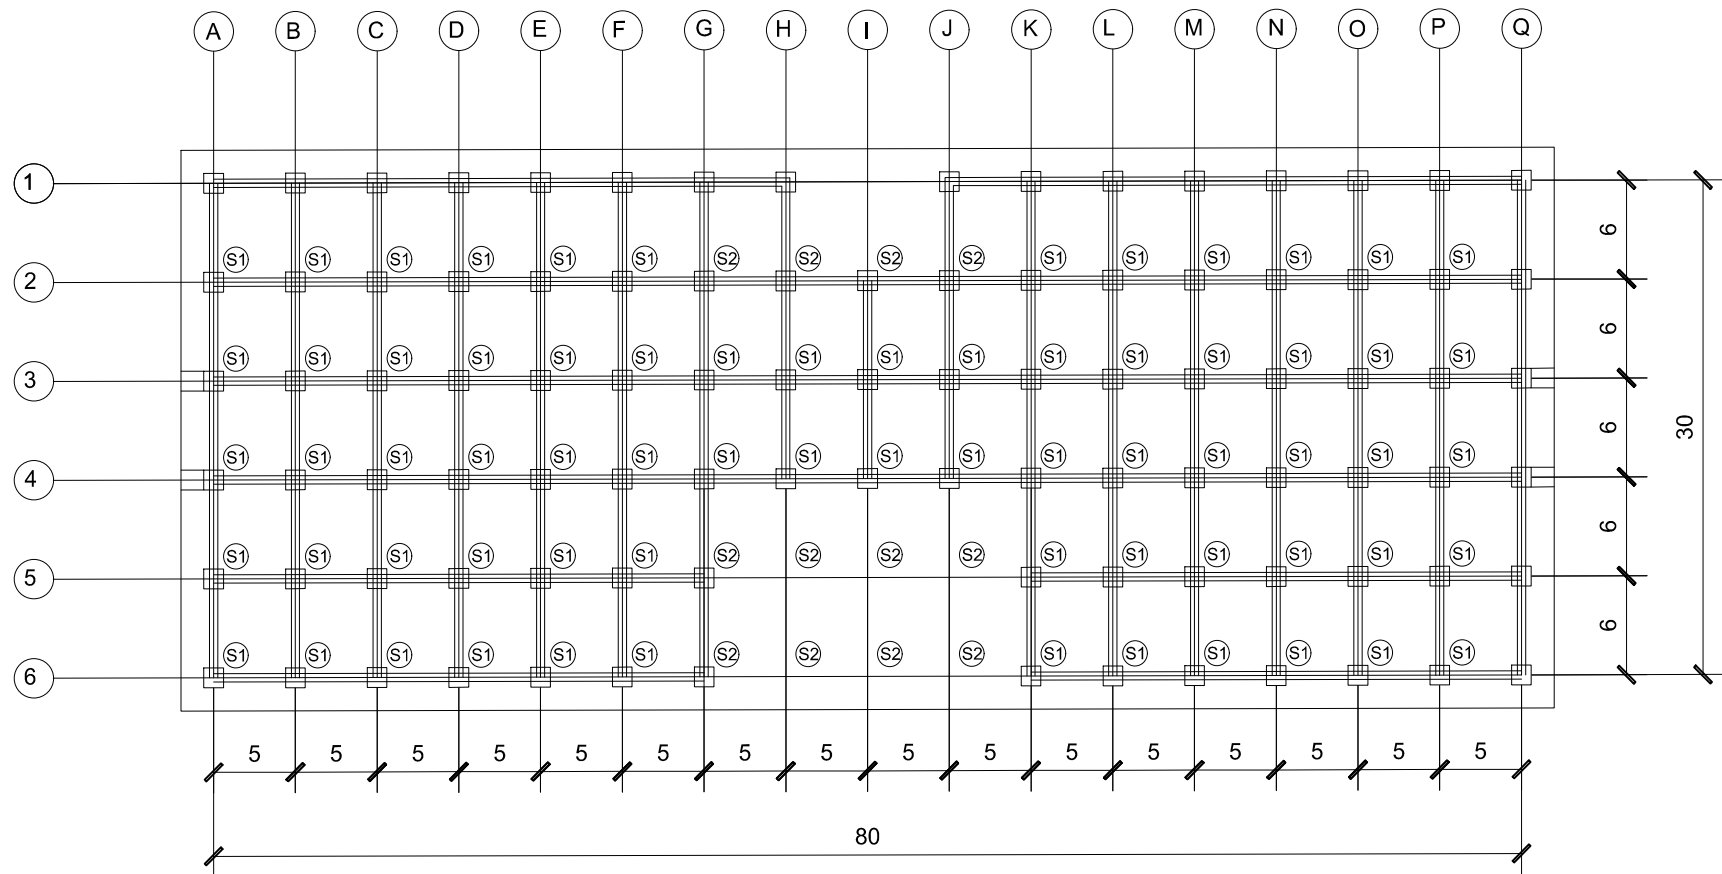

GROUND FLOOR SLAB LAYOUT

1:100

SLAB REINFORCEMENT DETAILS	
S1	10mm DIAMETER
S2	10mm DIAMETER



PROJECT:

PROPOSED 6-STOREY
MUNICIPAL BUILDING

LOCATION:

171 LAOAG - PAOAY RD, 2900
LAOG CITY, ILOCOS NORTE

PREPARED BY:

Ricki Lei D. Dela Rosa

BSCE IV-A

21-050147

OWNER:


ENGR. ARBIE MARIZ A. REVILLA

ARCHITECTURAL DRAWING

SHEET

S-4

27

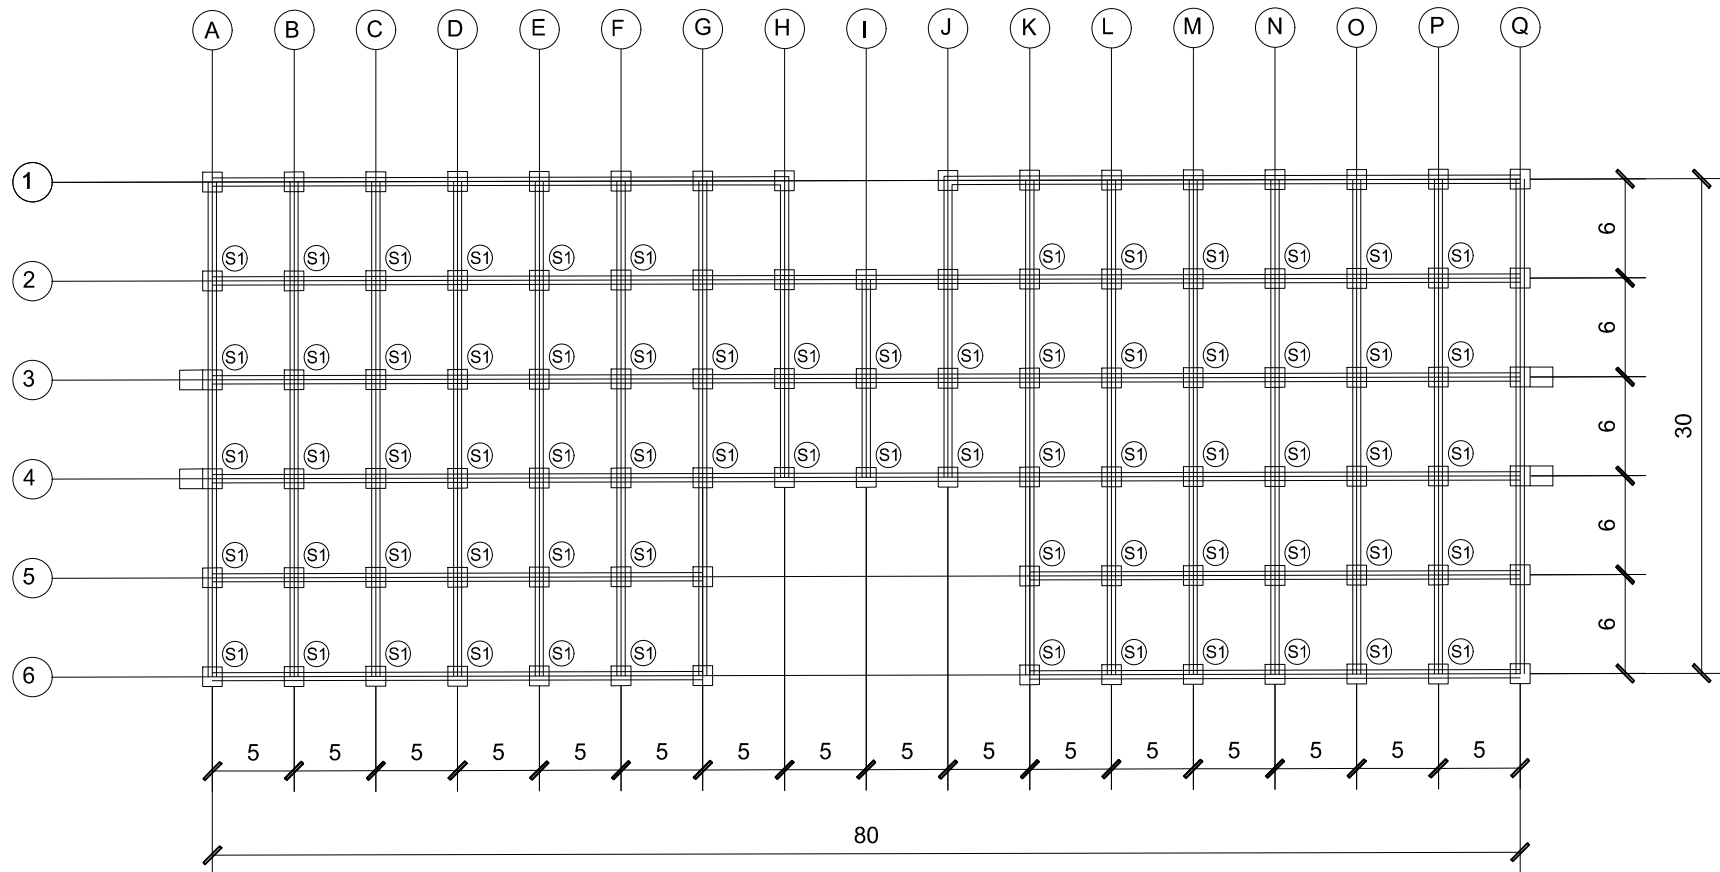

SECOND FLOOR SLAB LAYOUT

1:100

SLAB REINFORCEMENT DETAILS	
S1	10mm DIAMETER
S2	10mm DIAMETER



PROJECT:

PROPOSED 6-STOREY
MUNICIPAL BUILDING

LOCATION:

171 LAOAG - PAOAY RD, 2900
LAOG CITY, ILOCOS NORTE

PREPARED BY:

Ricki Lei D. Dela Rosa

BSCE IV-A

21-050147

OWNER:



ENGR. ARBIE MARIZ A. REVILLA

ARCHITECTURAL DRAWING

SHEET

S-4

28

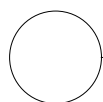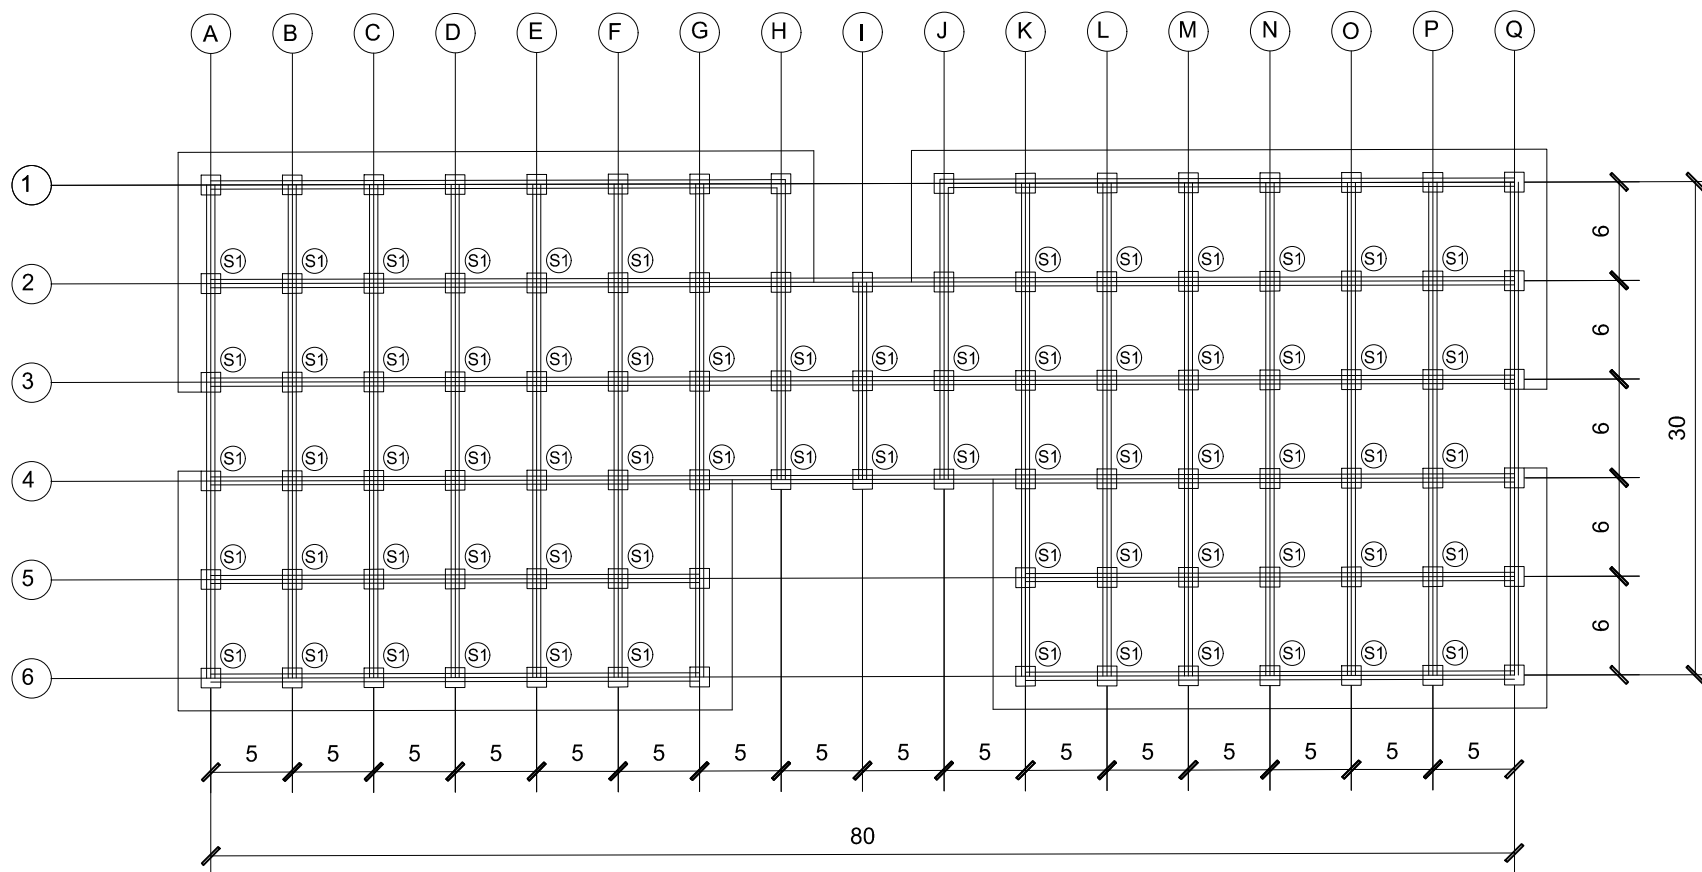

THIRD FLOOR SLAB LAYOUT

1:100

SLAB REINFORCEMENT DETAILS	
S1	10mm DIAMETER
S2	10mm DIAMETER



PROJECT:

PROPOSED 6-STOREY
MUNICIPAL BUILDING

LOCATION:

171 LAOAG - PAOAY RD, 2900
LAOG CITY, ILOCOS NORTE

PREPARED BY:

Ricki Lei D. Dela Rosa

BSCE IV-A

21-050147

OWNER:



ENGR. ARBIE MARIZ A. REVILLA

ARCHITECTURAL DRAWING

SHEET

S-4

29

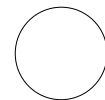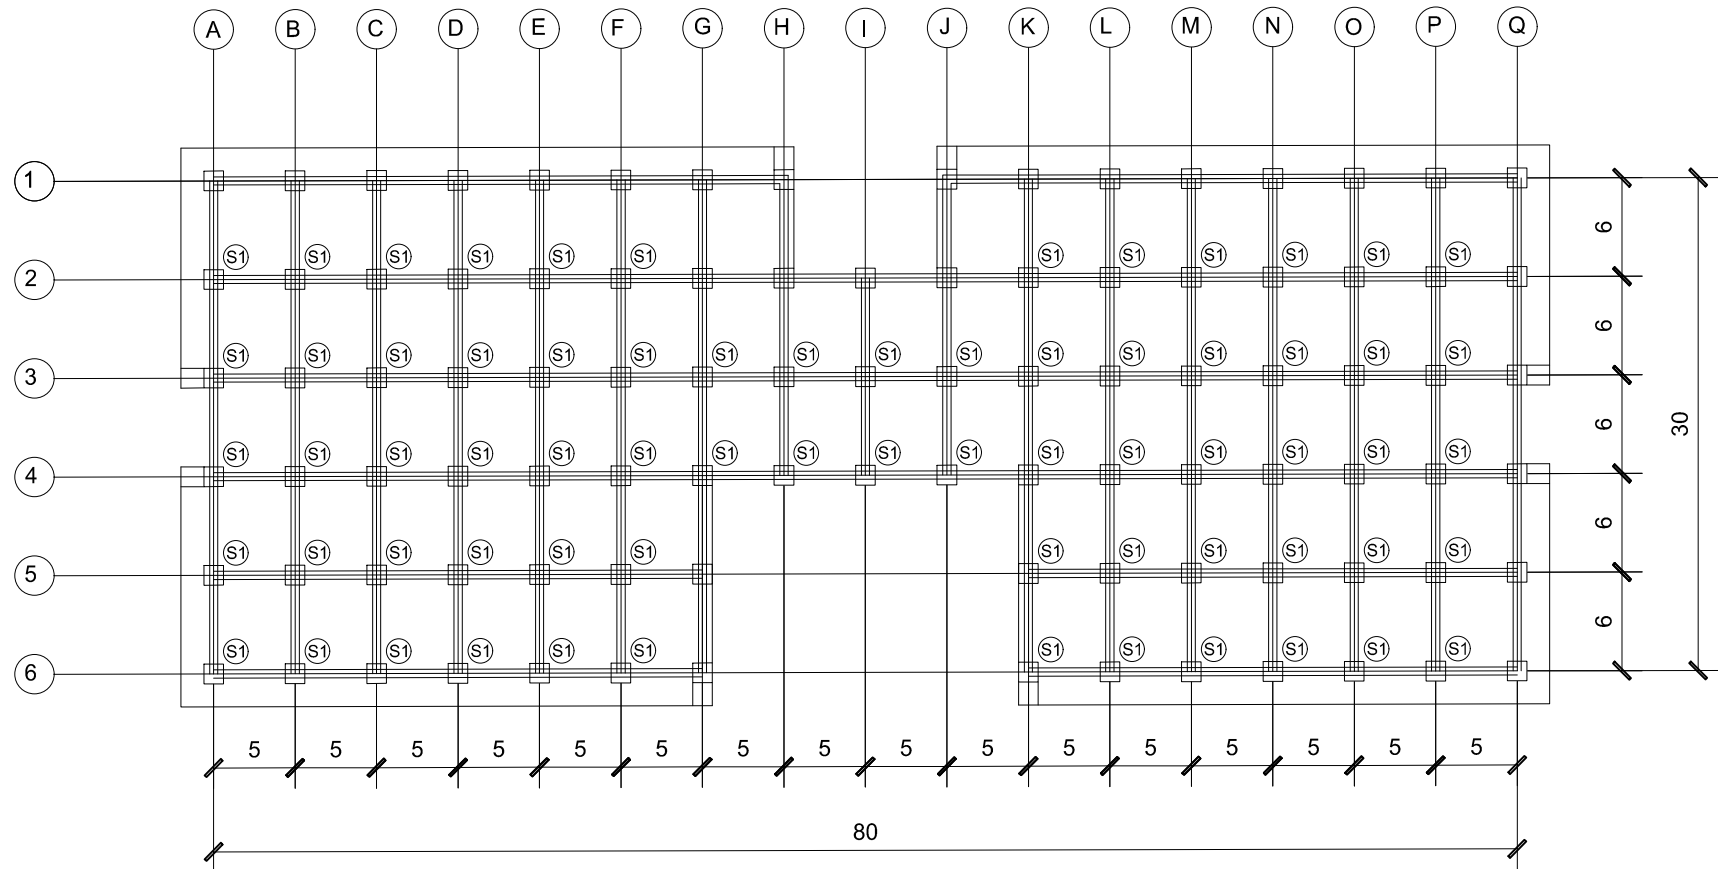

FOURTH FLOOR SLAB LAYOUT

1:100

SLAB REINFORCEMENT DETAILS	
S1	10mm DIAMETER
S2	10mm DIAMETER



PROJECT:

PROPOSED 6-STOREY
MUNICIPAL BUILDING

LOCATION:

171 LAOAG - PAOAY RD, 2900
LAOG CITY, ILOCOS NORTE

PREPARED BY:

Ricki Lei D. Dela Rosa

BSCE IV-A

21-050147

OWNER:


ENGR. ARBIE MARIZ A. REVILLA

ARCHITECTURAL DRAWING

SHEET

S-4

30

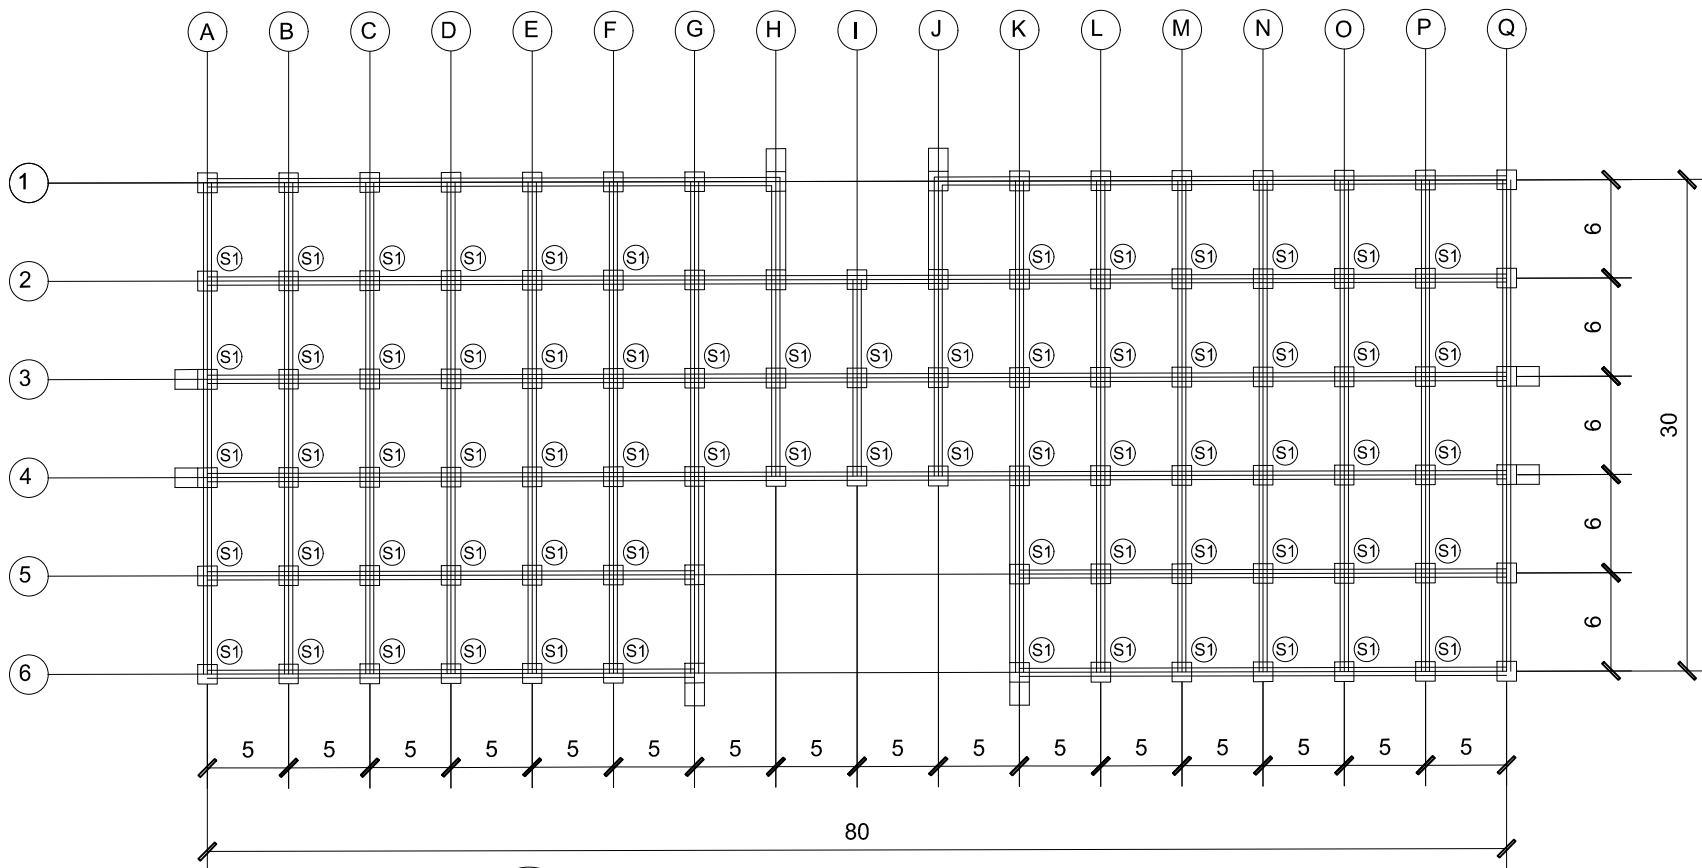



FIFTH FLOOR SLAB LAYOUT

1:100

SLAB REINFORCEMENT DETAILS	
S1	10mm DIAMETER
S2	10mm DIAMETER



PROJECT:	PROPOSED 6-STOREY MUNICIPAL BUILDING	PREPARED BY:	Ricki Lei D. Dela Rosa	OWNER:	ENGR. ARBIE MARIZ A. REVILLA	SHEET S-4 31
	LOCATION:		BSCE IV-A			
	171 LAOAG - PAOAY RD, 2900 LAOG CITY, ILOCOS NORTE		21-050147	ARCHITECTURAL DRAWING		

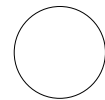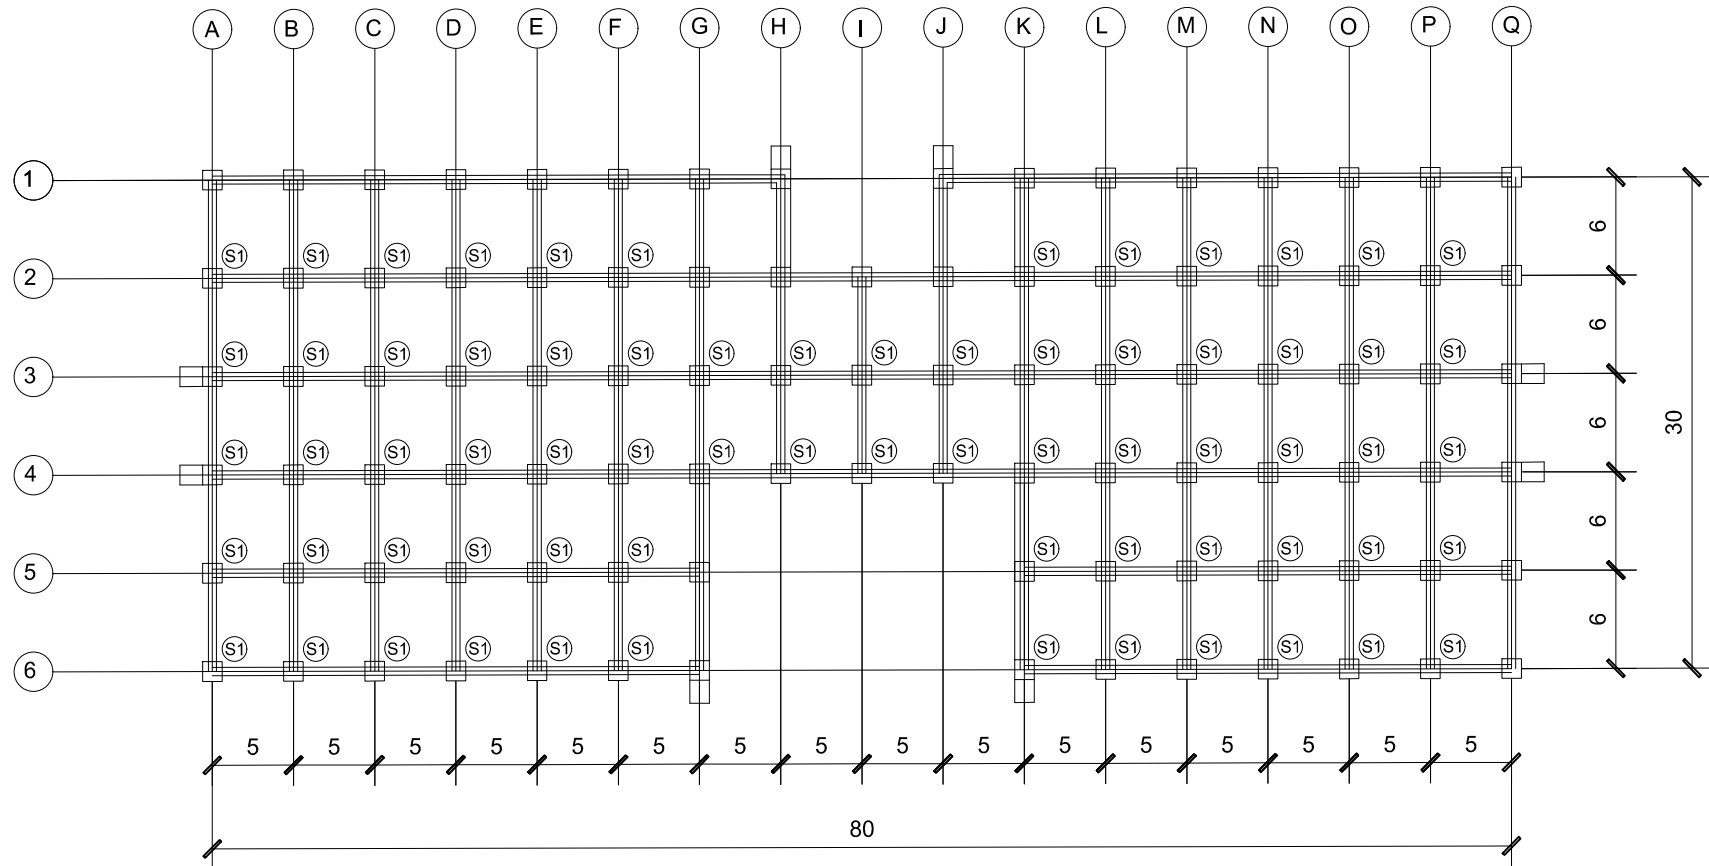

SIXTH FLOOR SLAB LAYOUT

1:100

SLAB REINFORCEMENT DETAILS	
S1	10mm DIAMETER
S2	10mm DIAMETER



PROJECT:

PROPOSED 6-STOREY
MUNICIPAL BUILDING

LOCATION:

171 LAOAG - PAOAY RD, 2900
LAOG CITY, ILOCOS NORTE

PREPARED BY:

Ricki Lei D. Dela Rosa

BSCE IV-A

21-050147

OWNER:



ENGR. ARBIE MARIZ A. REVILLA

ARCHITECTURAL DRAWING

SHEET

S-4

32

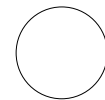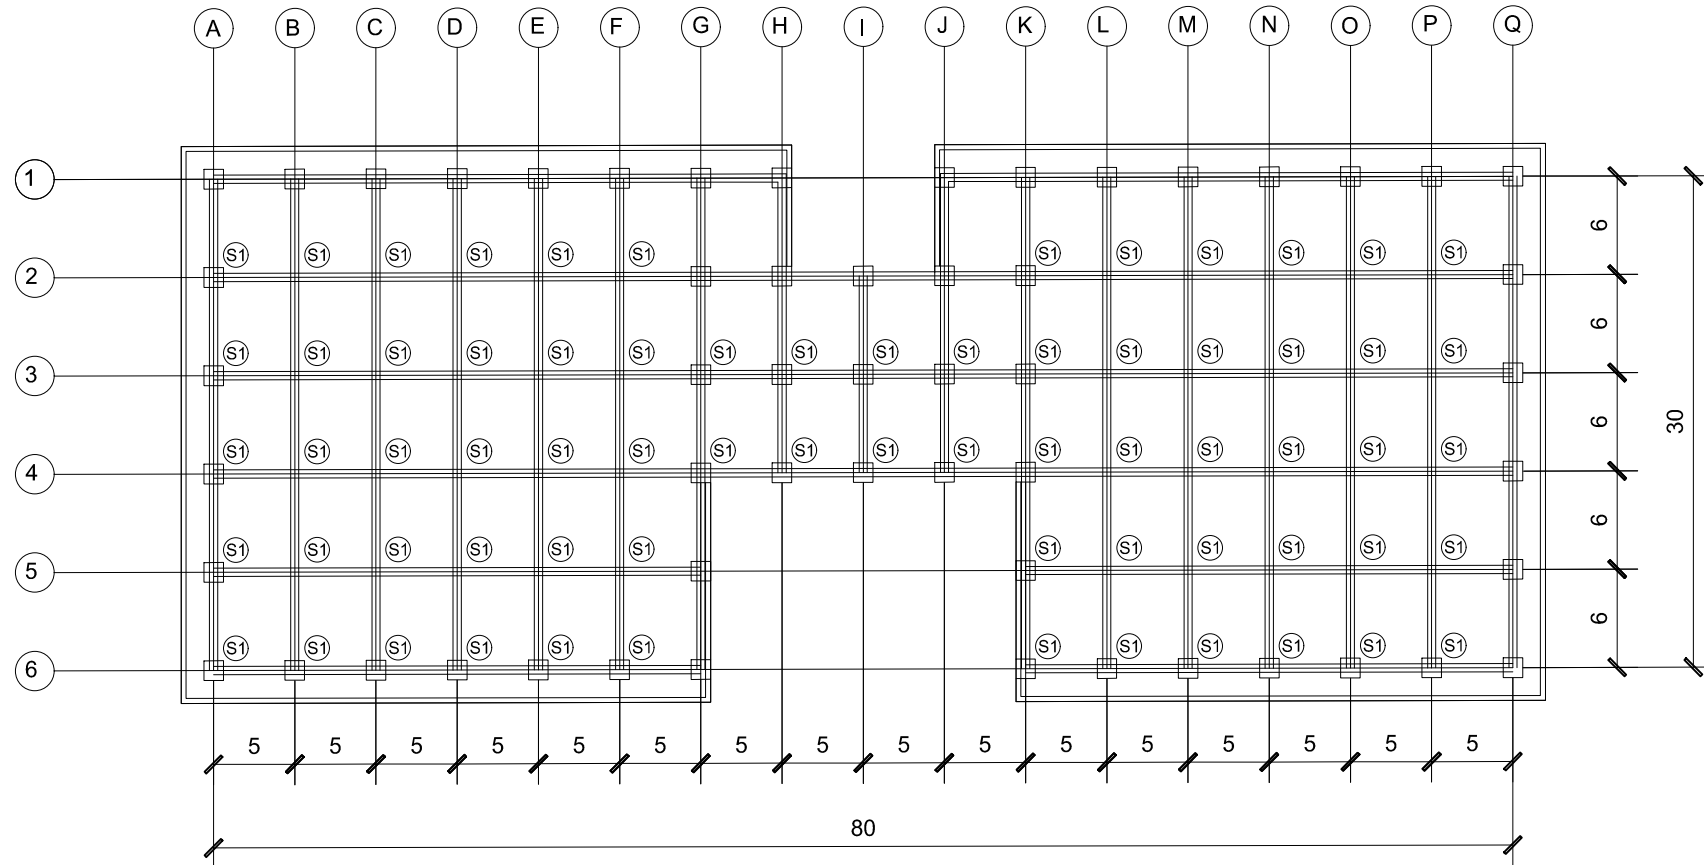

ROOF DECK FLOOR SLAB LAYOUT

1:100

SLAB REINFORCEMENT DETAILS	
S1	10mm DIAMETER
S2	10mm DIAMETER



PROJECT:

PROPOSED 6-STOREY
MUNICIPAL BUILDING

LOCATION:

171 LAOAG - PAOAY RD, 2900
LAOG CITY, ILOCOS NORTE

PREPARED BY:

Ricki Lei D. Dela Rosa

BSCE IV-A

21-050147

OWNER:



ENGR. ARBIE MARIZ A. REVILLA

ARCHITECTURAL DRAWING

SHEET

S-4

33

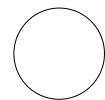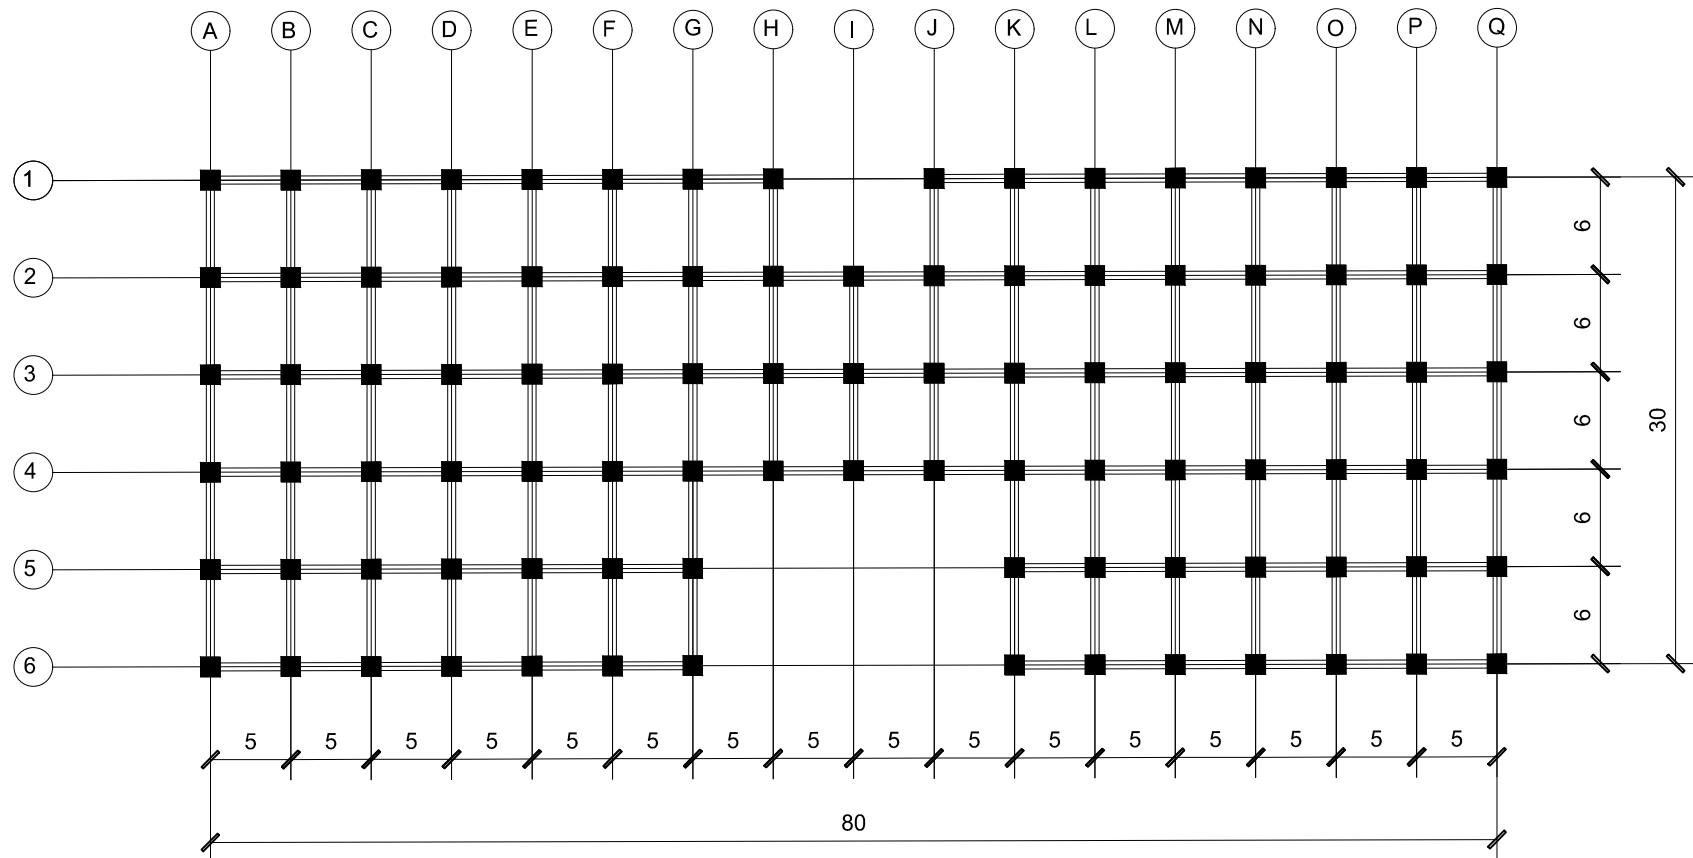

GROUND FLOOR STRUCTURAL FRAME

1:100



PROJECT:

PROPOSED 6-STOREY
MUNICIPAL BUILDING

LOCATION:

171 LAOAG - PAOAY RD, 2900
LAOG CITY, ILOCOS NORTE

PREPARED BY:

Ricki Lei D. Dela Rosa

BSCE IV-A

21-050147

OWNER:



ENGR. ARBIE MARIZ A. REVILLA

ARCHITECTURAL DRAWING

SHEET

S-5

34

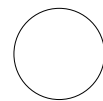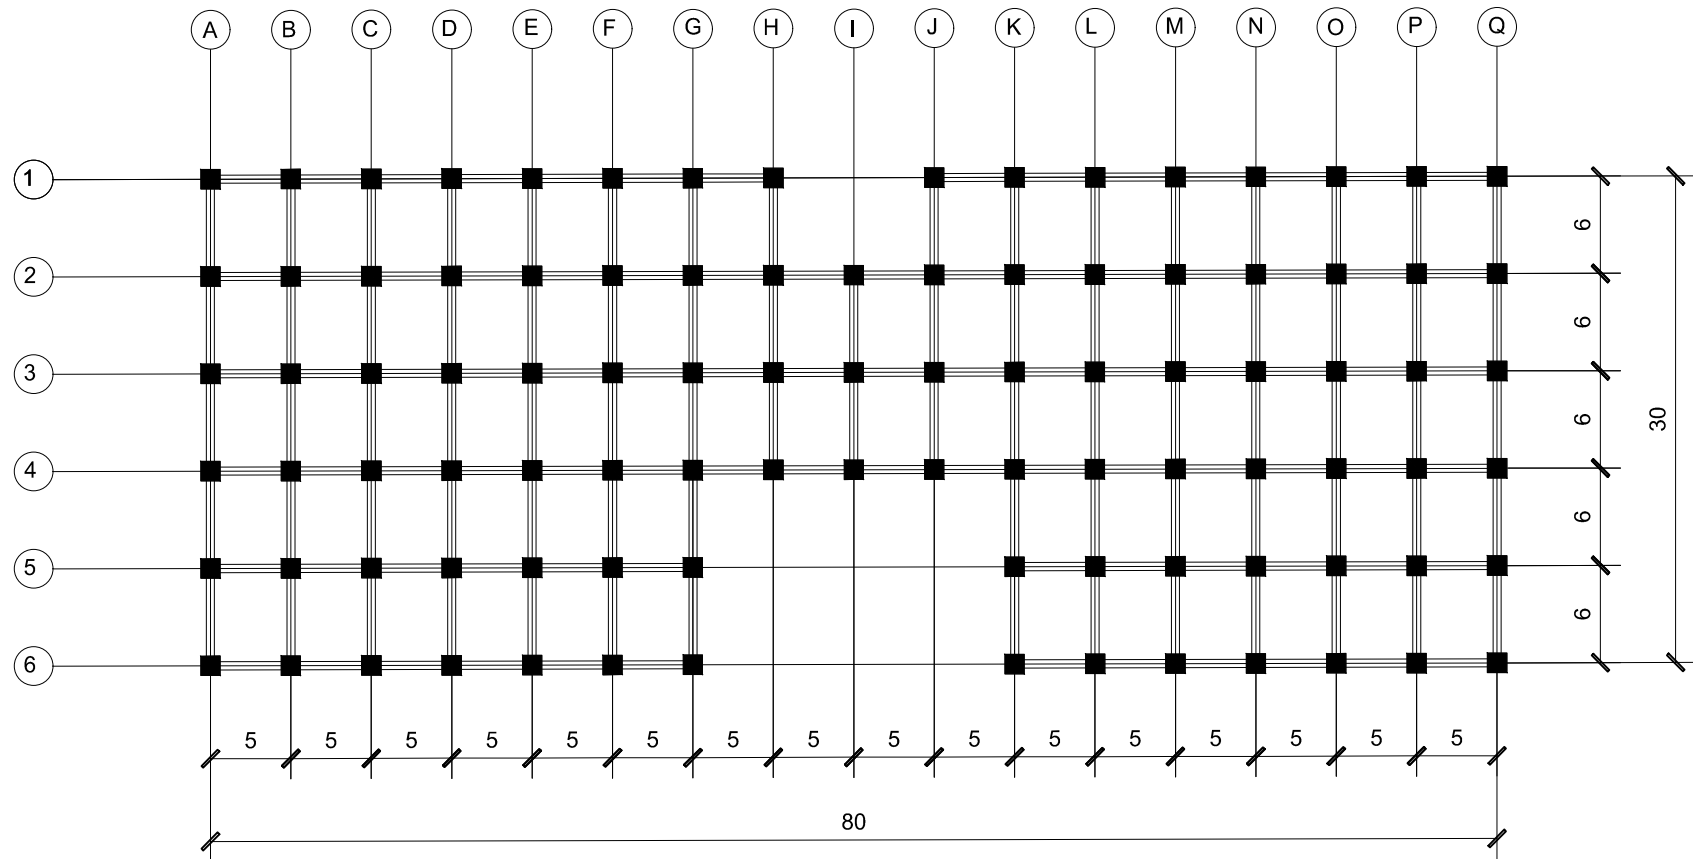

SECOND FLOOR STRUCTURAL FRAME

1:100



PROJECT:

PROPOSED 6-STOREY
MUNICIPAL BUILDING

LOCATION:

171 LAOAG - PAOAY RD, 2900
LAOG CITY, ILOCOS NORTE

PREPARED BY:

Ricki Lei D. Dela Rosa

BSCE IV-A

21-050147

OWNER:



ENGR. ARBIE MARIZ A. REVILLA

ARCHITECTURAL DRAWING

SHEET

S-5

35

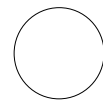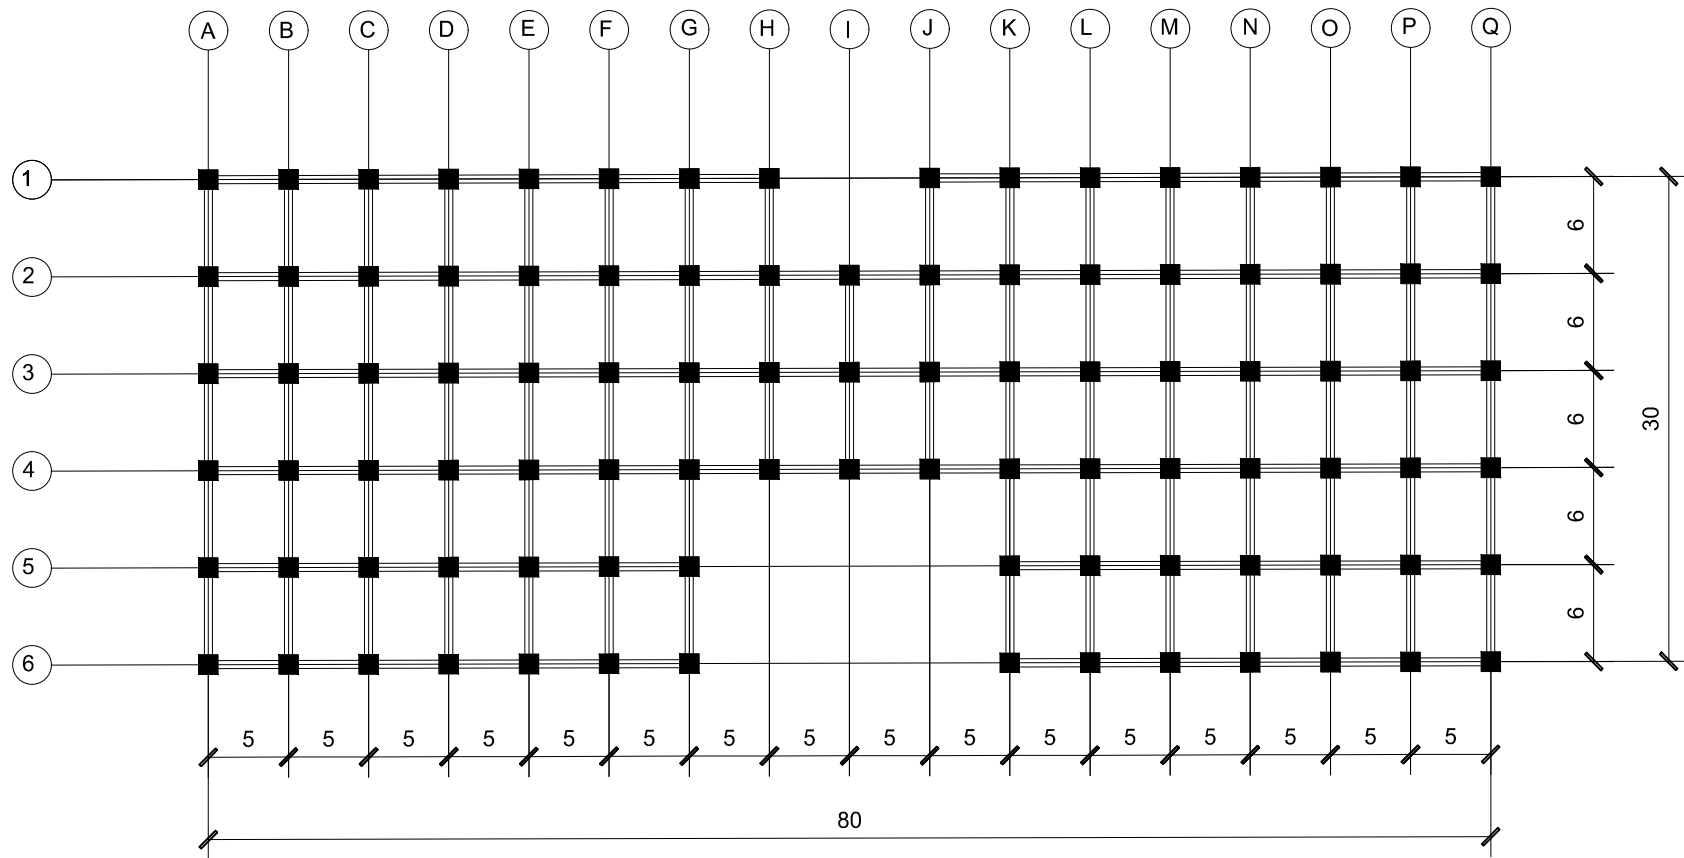

THIRD FLOOR STRUCTURAL FRAME

1:100



PROJECT:

PROPOSED 6-STOREY
MUNICIPAL BUILDING

LOCATION:

171 LAOAG - PAOAY RD, 2900
LAOG CITY, ILOCOS NORTE

PREPARED BY:

Ricki Lei D. Dela Rosa

BSCE IV-A

21-050147

OWNER:



ENGR. ARBIE MARIZ A. REVILLA

ARCHITECTURAL DRAWING

SHEET

S-5

36

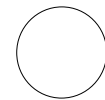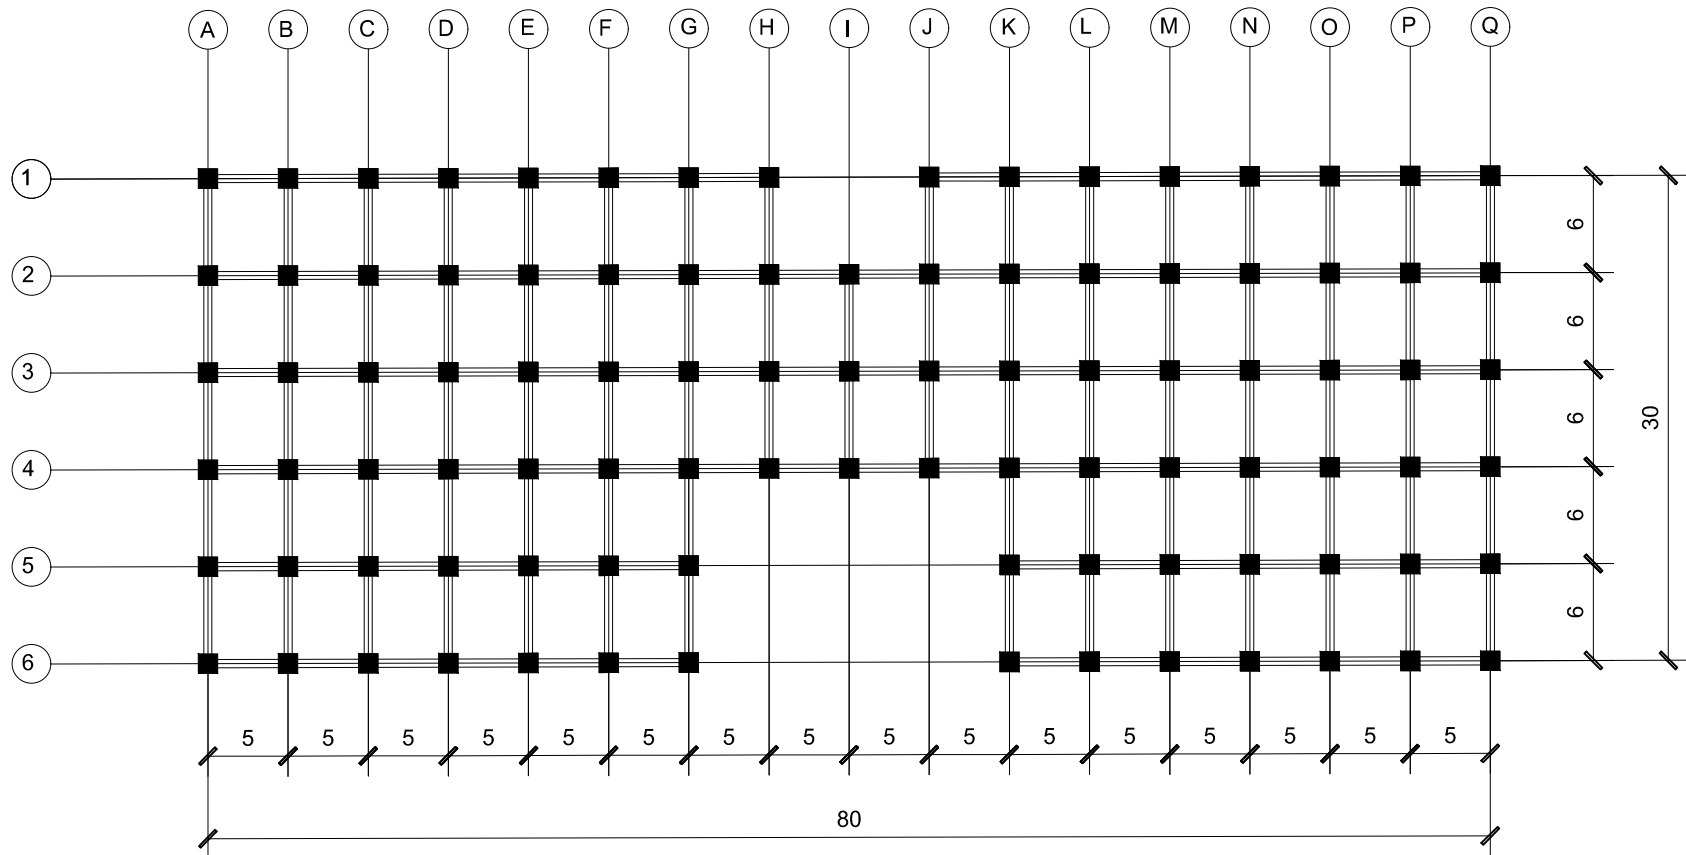

FOURTH FLOOR STRUCTURAL FRAME

1:100



PROJECT:

PROPOSED 6-STOREY
MUNICIPAL BUILDING

LOCATION:

171 LAOAG - PAOAY RD, 2900
LAOG CITY, ILOCOS NORTE

PREPARED BY:

Ricki Lei D. Dela Rosa

BSCE IV-A

21-050147

OWNER:



ENGR. ARBIE MARIZ A. REVILLA

ARCHITECTURAL DRAWING

SHEET

S-5

37

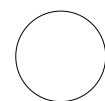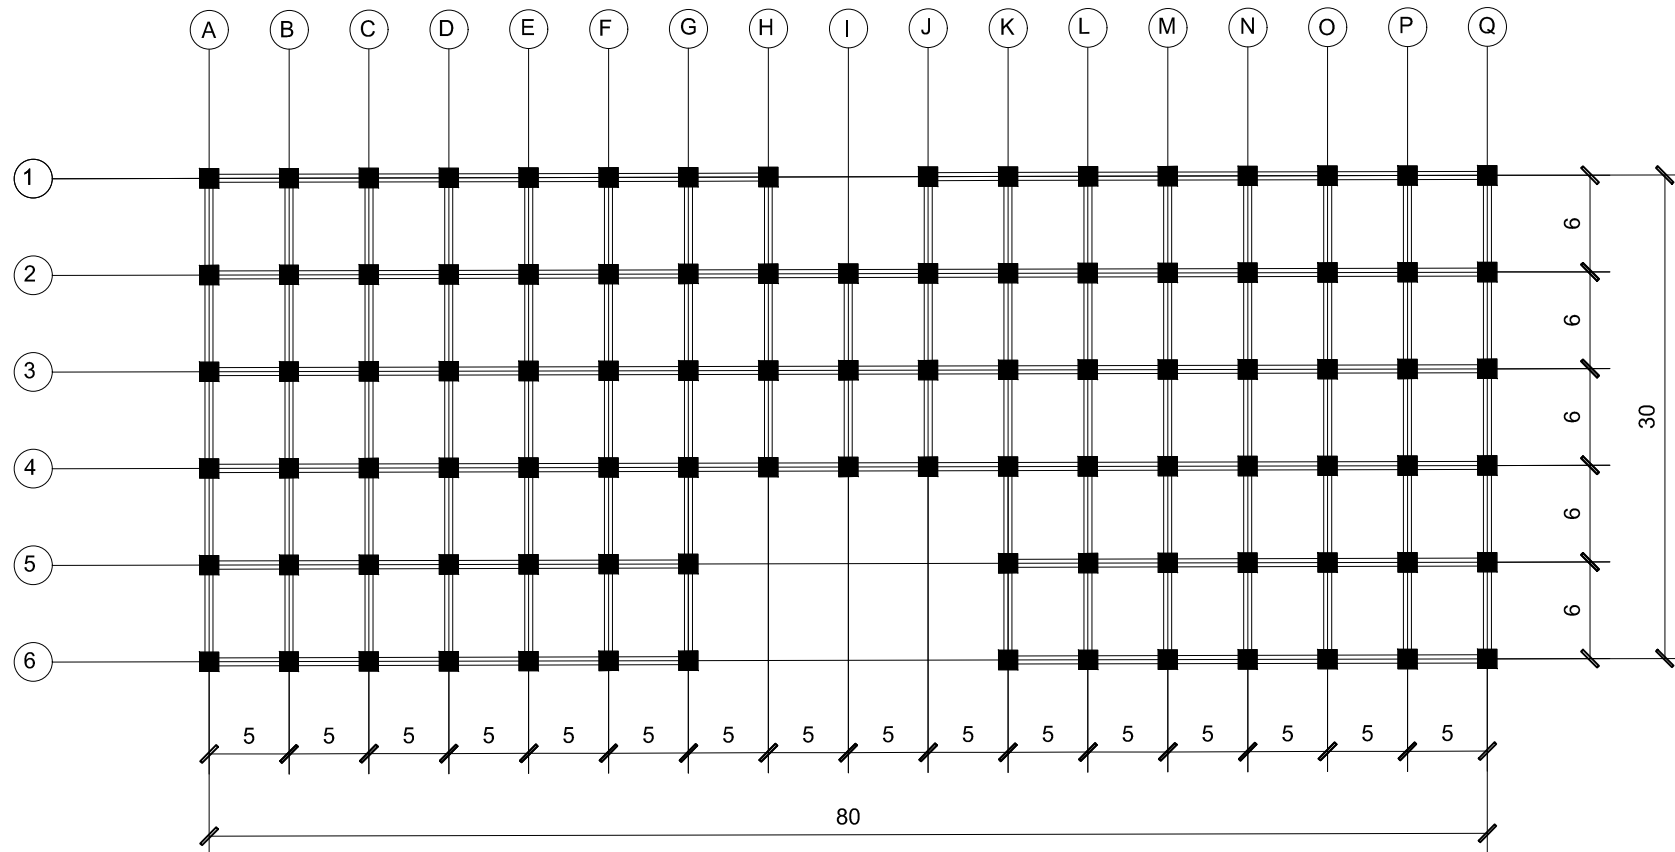

FIFTH FLOOR STRUCTURAL FRAME

1:100



PROJECT:

PROPOSED 6-STOREY
MUNICIPAL BUILDING

LOCATION:

171 LAOAG - PAOAY RD, 2900
LAOG CITY, ILOCOS NORTE

PREPARED BY:

Ricki Lei D. Dela Rosa

BSCE IV-A

21-050147

OWNER:



ENGR. ARBIE MARIZ A. REVILLA

ARCHITECTURAL DRAWING

SHEET

S-5

38

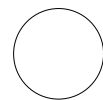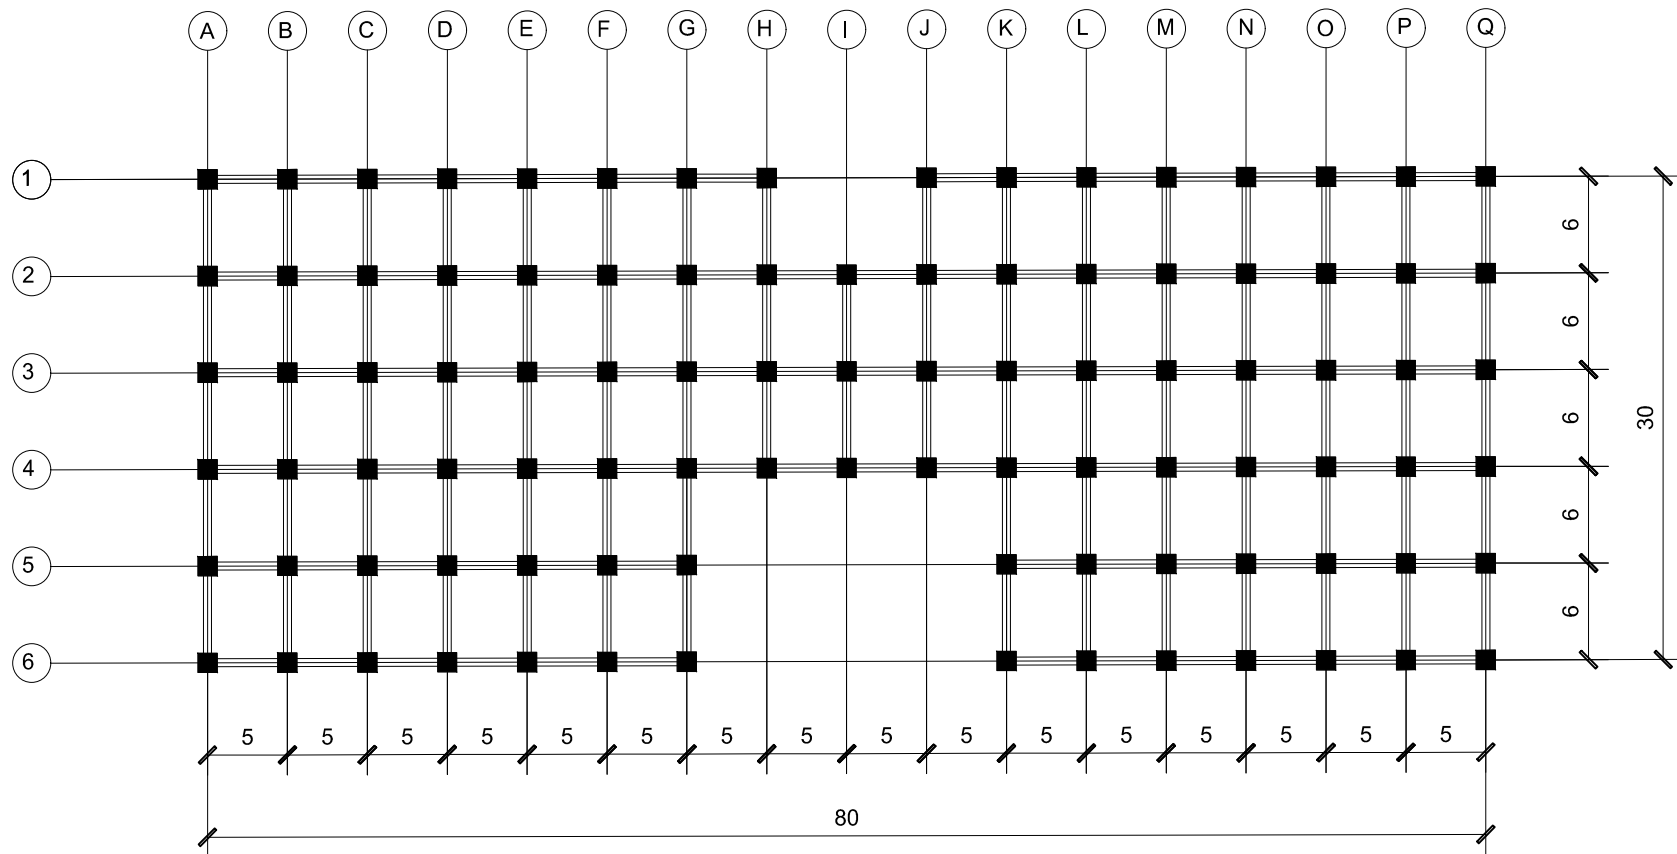

SIXTH FLOOR STRUCTURAL FRAME

1:100



PROJECT:

PROPOSED 6-STOREY
MUNICIPAL BUILDING

LOCATION:

171 LAOAG - PAOAY RD, 2900
LAOAG CITY, ILOCOS NORTE

PREPARED BY:

Ricki Lei D. Dela Rosa

BSCE IV-A

21-050147

OWNER:



ENGR. ARBIE MARIZ A. REVILLA

ARCHITECTURAL DRAWING

SHEET

S-5

39

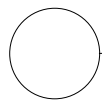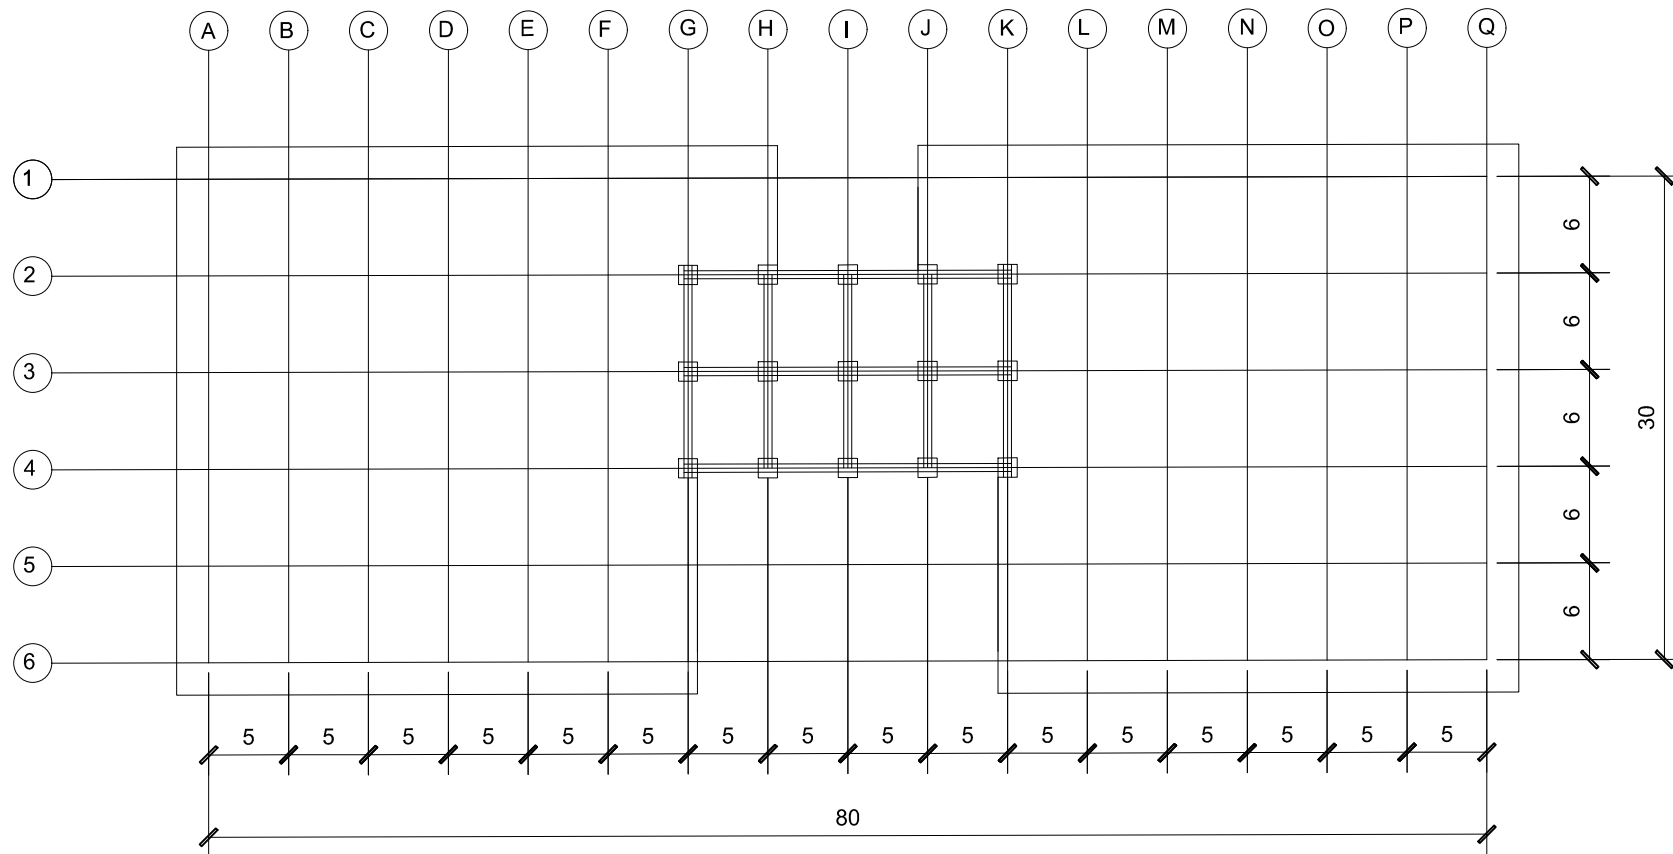

ROOF DECK STRUCTURAL FRAME

1:100



PROJECT:

PROPOSED 6-STOREY
MUNICIPAL BUILDING

LOCATION:

171 LAOAG - PAOAY RD, 2900
LAOG CITY, ILOCOS NORTE

PREPARED BY:

Ricki Lei D. Dela Rosa

BSCE IV-A

21-050147

OWNER:


ENGR. ARBIE MARIZ A. REVILLA

ARCHITECTURAL DRAWING

SHEET

S-5

40

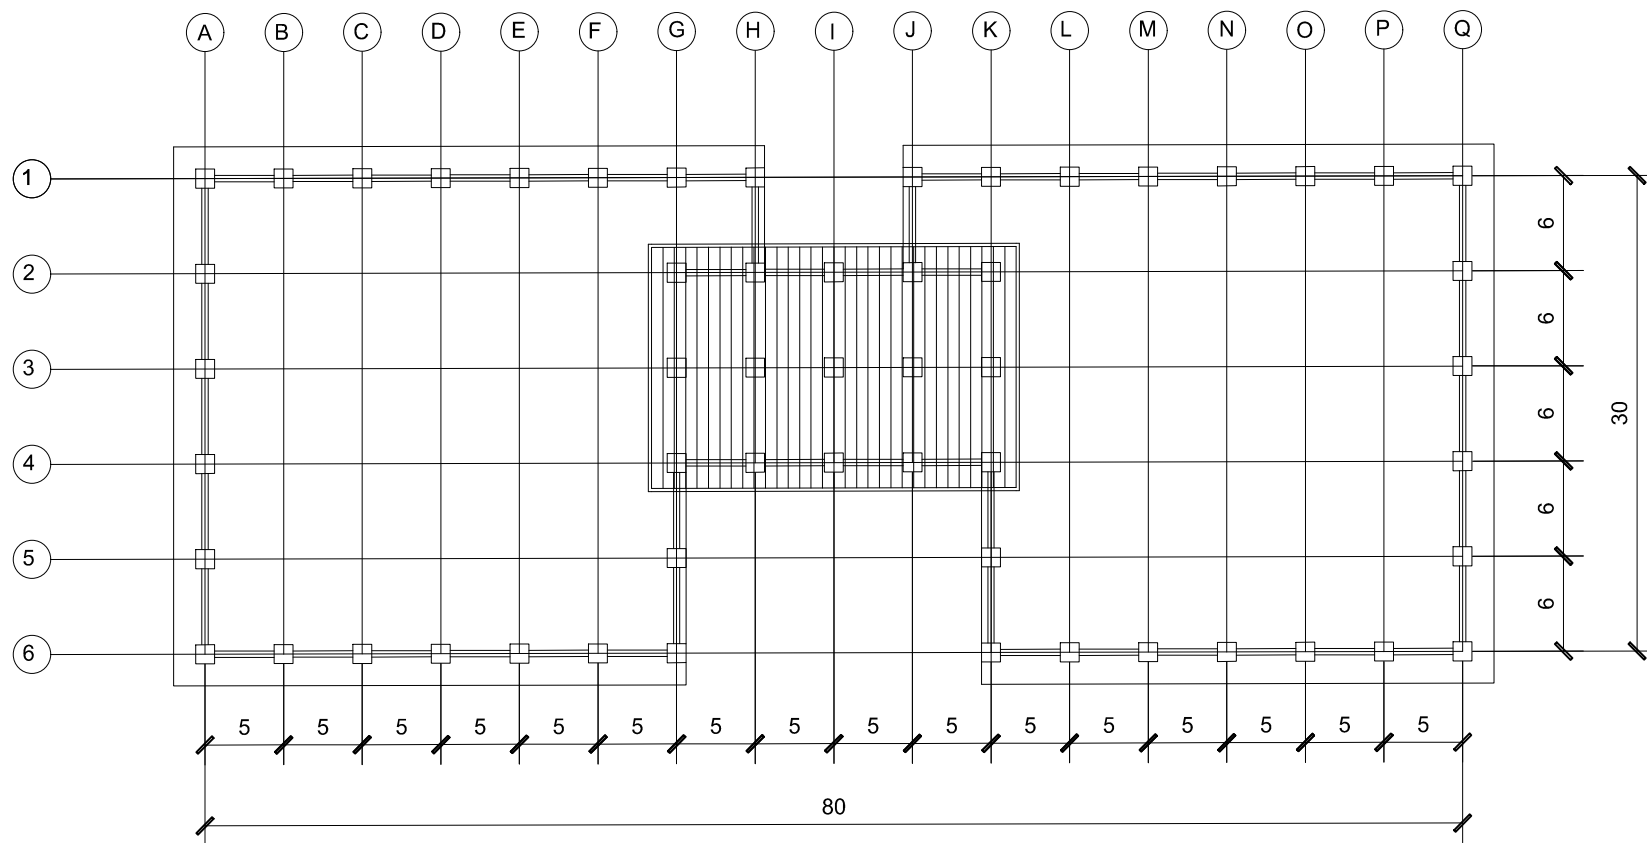

ROOF FRAMING PLAN
1:100



PROJECT:

PROPOSED 6-STOREY
MUNICIPAL BUILDING

LOCATION:

171 LAOAG - PAOAY RD, 2900
LAOG CITY, ILOCOS NORTE

PREPARED BY:

Ricki Lei D. Dela Rosa

BSCE IV-A

21-050147

OWNER:



ENGR. ARBIE MARIZ A. REVILLA

ARCHITECTURAL DRAWING

SHEET

S-6

41

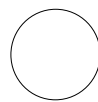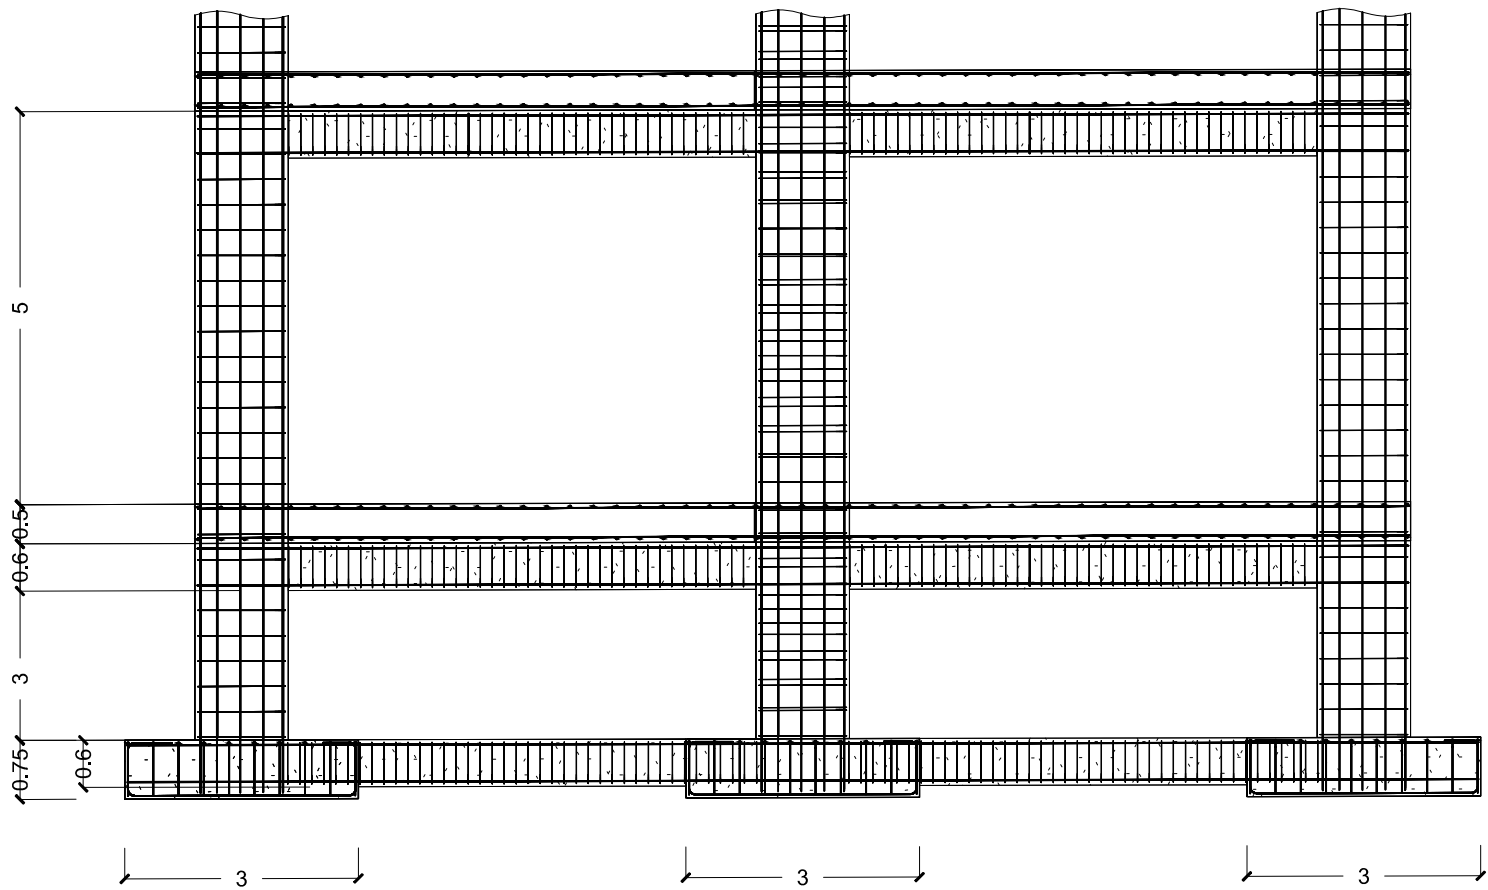

STRUCTURAL DETAILS

1:100



PROJECT:

PROPOSED 6-STOREY
MUNICIPAL BUILDING

LOCATION:

171 LAOAG - PAOAY RD, 2900
LAOG CITY, ILOCOS NORTE

PREPARED BY:

Ricki Lei D. Dela Rosa

BSCE IV-A

21-050147

OWNER:

ENGR. ARBIE MARIZ A. REVILLA

ARCHITECTURAL DRAWING

SHEET

S-7

42