




	PROJECT:	PREPARED BY:	OWNER:	SHEET: A-1 1
	PROPOSED 6-STOREY RESIDENTIAL BUILDING	IAIN MATTHEW B. BARRUGA ENGINEER	ENGR. ARBIE MARIZ A. PADILLA	
	LOCATION:	BSCE IV-A		
	51-A NANGALISAN,2900 LAOAG CITY, ILOCOS NORTE	21-050060	ARCHITECTURAL DRAWINGS	



	PROJECT:	PREPARED BY:	OWNER:	SHEET:
	PROPOSED 6-STOREY RESIDENTIAL BUILDING	<u>IAIN MATTHEW B. BARRUGA</u> ENGINEER	ENGR. ARBIE MARIZ A. PADILLA	A-1 2
	LOCATION:	BSCE IV-A		
	51-A NANGALISAN, 2900 LAOAG CITY, ILOCOS NORTE	21-050060	ARCHITECTURAL DRAWINGS	

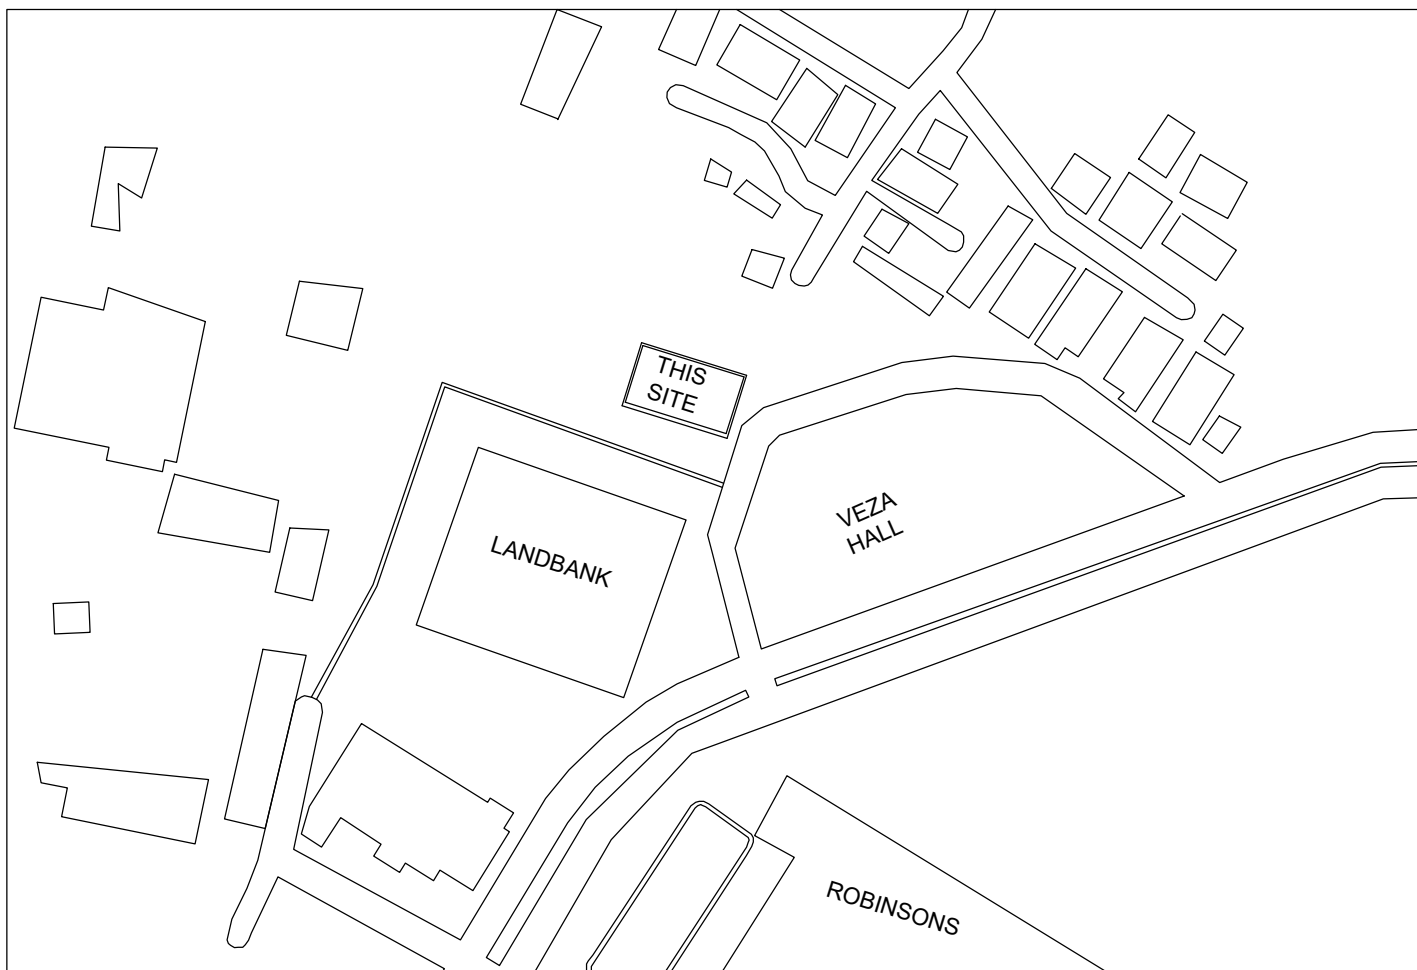


A-1
3

VICINITY MAP
SCALE NTS



PROJECT:	PROPOSED 6-STOREY RESIDENTIAL BUILDING	PREPARED BY:	<u>IAIN MATTHEW B. BARRUGA</u> ENGINEER	OWNER:	ENGR. ARBIE MARIZ A. PADILLA	SHEET:	A-1
LOCATION:	51-A NANGALISAN, 2900 LAOAG CITY, ILOCOS NORTE		BSCE IV-A				
			21-050060		ARCHITECTURAL DRAWINGS		3

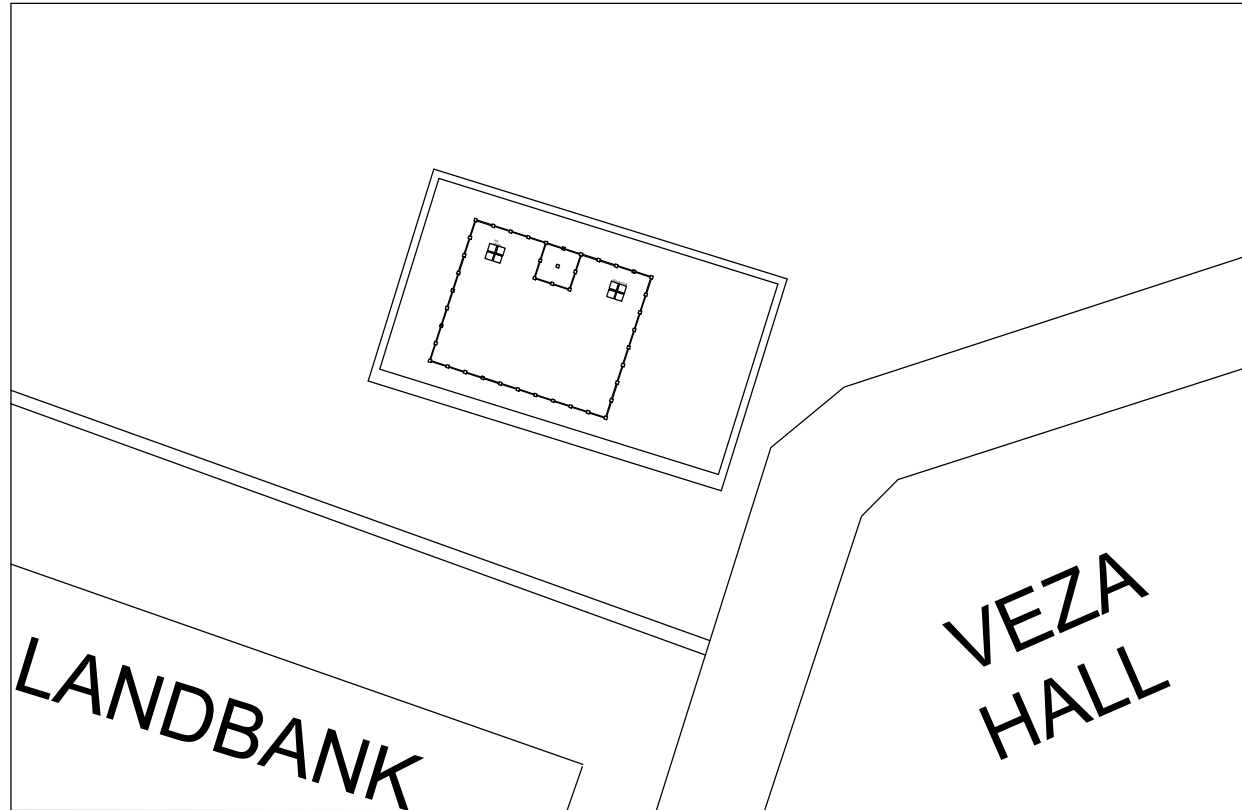


A-1
4

 SITE DEVELOPMENT PLAN
 SCALE NTS



PROJECT:	PROPOSED 6-STOREY RESIDENTIAL BUILDING	PREPARED BY:	<u>IAIN MATTHEW B. BARRUGA</u> ENGINEER	OWNER:	ENGR. ARBIE MARIZ A. PADILLA	SHEET:	A-1
LOCATION:	51-A NANGALISAN, 2900 LAOAG CITY, ILOCOS NORTE		BSCE IV-A				
			21-050060		ARCHITECTURAL DRAWINGS		4

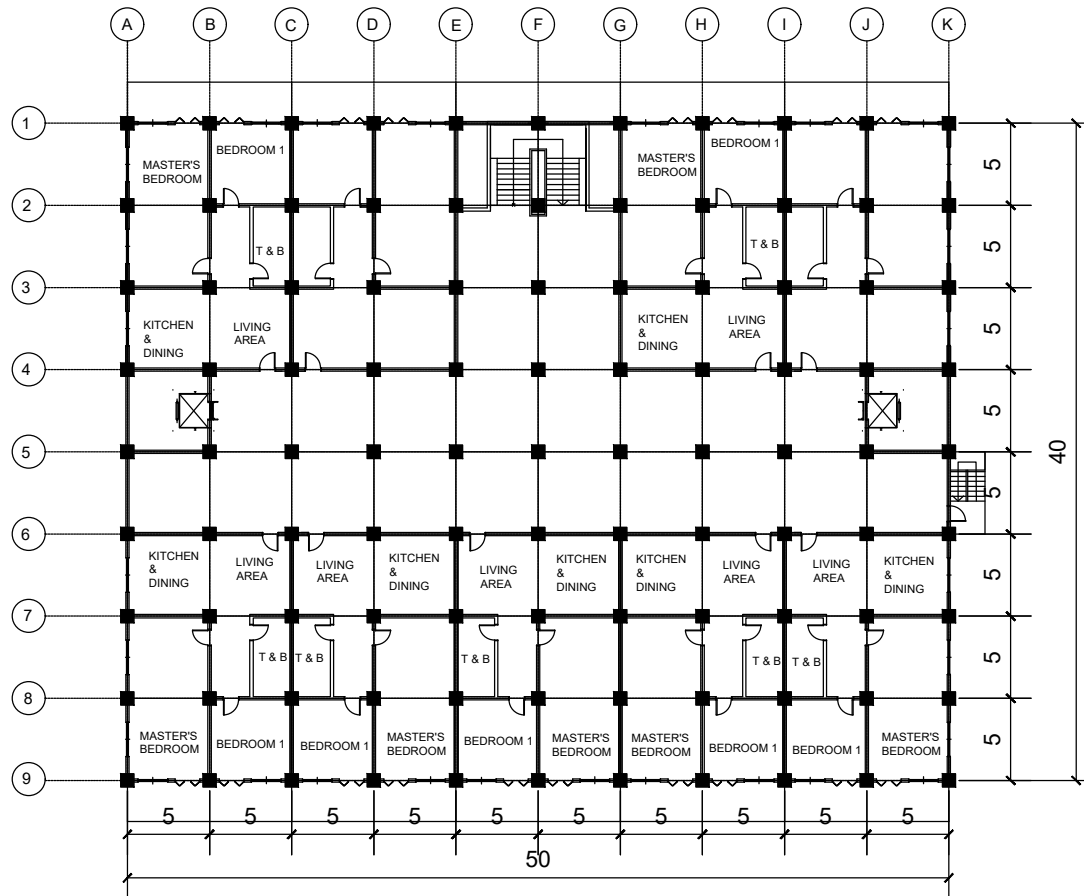

A-2
6

SECOND FLOOR PLAN

SCALE

NTS



PROJECT:

PROPOSED 6-STOREY
RESIDENTIAL BUILDING

LOCATION:

51-A NANGALISAN, 2900
LAOAG CITY, ILOCOS NORTE

PREPARED BY:

IAIN MATTHEW B. BARRUGA
ENGINEER

BSCE IV-A

21-050060

OWNER:


ENGR. ARBIE MARIZ A. PADILLA

ARCHITECTURAL DRAWINGS

SHEET:

A-2

6

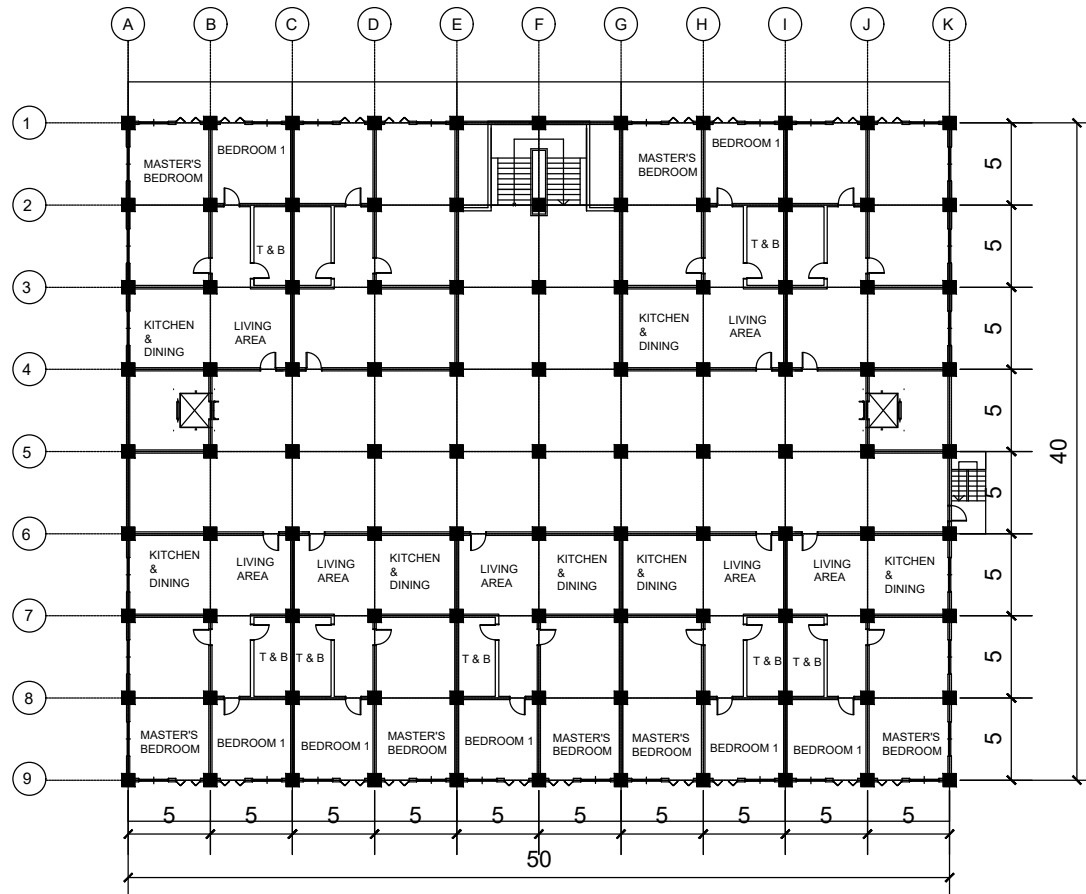


A-2
7

 THIRD FLOOR PLAN
 SCALE _____ NTS



PROJECT: PROPOSED 6-STOREY RESIDENTIAL BUILDING LOCATION: 51-A NANGALISAN, 2900 LAOAG CITY, ILOCOS NORTE	PREPARED BY: IAIN MATTHEW B. BARRUGA ENGINEER BSCE IV-A 21-050060	OWNER: ENGR. ARBIE MARIZ A. PADILLA ARCHITECTURAL DRAWINGS	SHEET: A-2 7

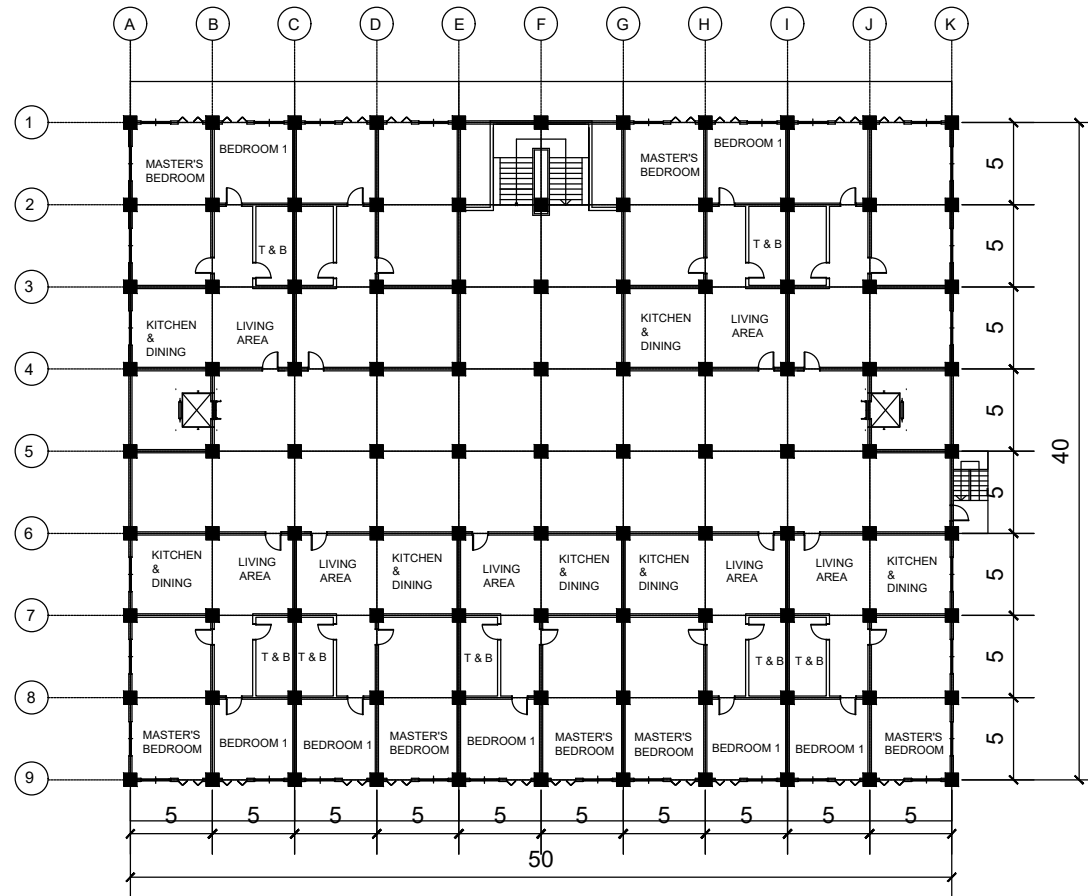

A-2
8 SCALE NTS

FOURTH FLOOR PLAN



PROJECT:

PROPOSED 6-STOREY
RESIDENTIAL BUILDING

LOCATION:

51-A NANGALISAN, 2900
LAOAG CITY, ILOCOS NORTE

PREPARED BY:

IAIN MATTHEW B. BARRUGA
ENGINEER

BSCE IV-A

21-050060

OWNER:


ENGR. ARBIE MARIZ A. PADILLA

ARCHITECTURAL DRAWINGS

SHEET:

A-2

8

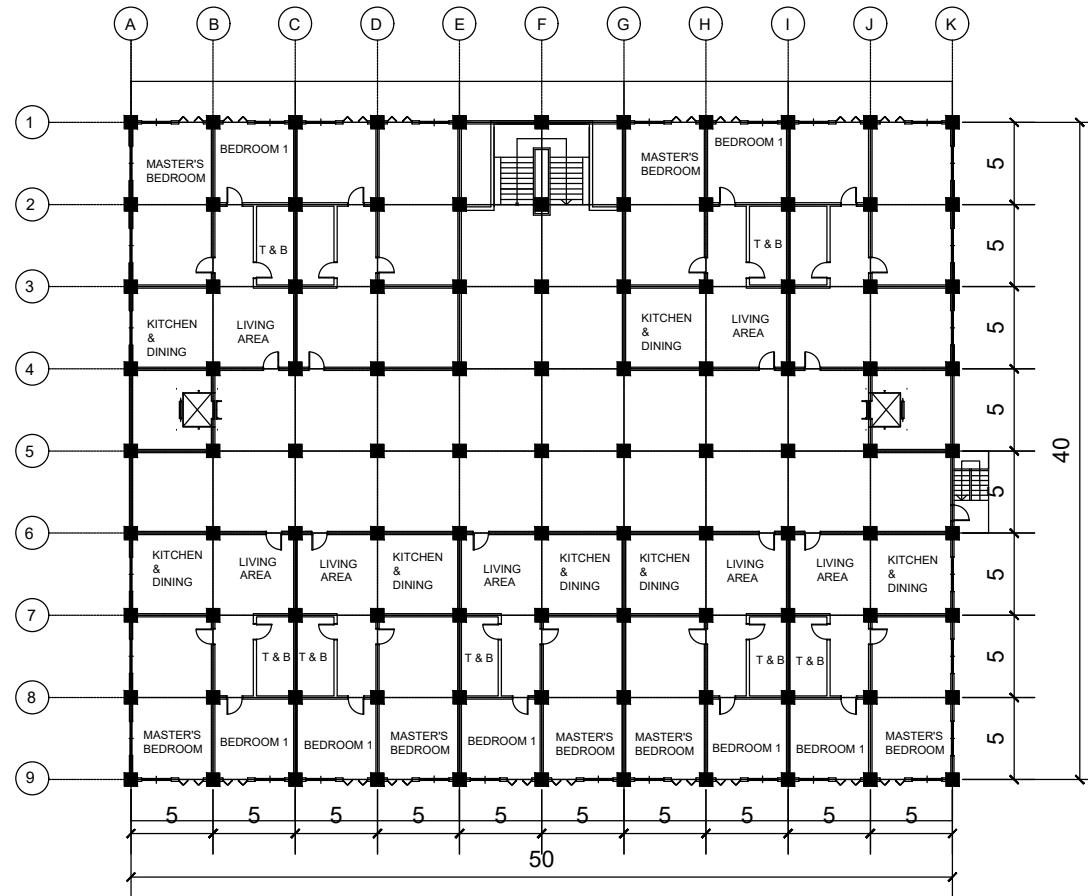

A-2
9

FIFTH FLOOR PLAN

SCALE

NTS



PROJECT:

PROPOSED 6-STOREY
RESIDENTIAL BUILDING

LOCATION:

51-A NANGALISAN, 2900
LAOAG CITY, ILOCOS NORTE

PREPARED BY:

IAIN MATTHEW B. BARRUGA
ENGINEER

BSCE IV-A

21-050060

OWNER:


ENGR. ARBIE MARIZ A. PADILLA

ARCHITECTURAL DRAWINGS

SHEET:

A-2


9

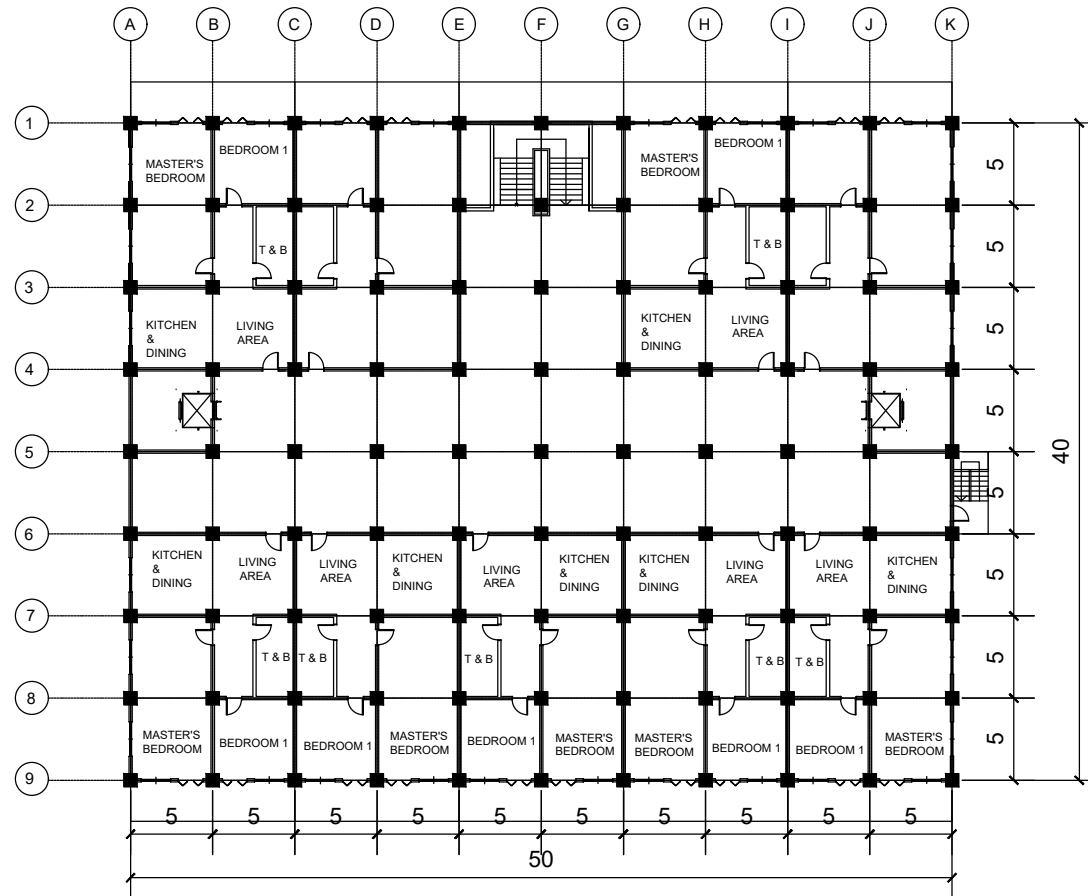

A-2
10 SCALE NTS



PROJECT:	PROPOSED 6-STOREY RESIDENTIAL BUILDING	PREPARED BY:	IAIN MATTHEW B. BARRUGA ENGINEER	OWNER:	ENGR. ARBIE MARIZ A. PADILLA	SHEET:	A-2
LOCATION:	51-A NANGALISAN, 2900 LAOAG CITY, ILOCOS NORTE		BSCE IV-A				
			21-050060		ARCHITECTURAL DRAWINGS		10

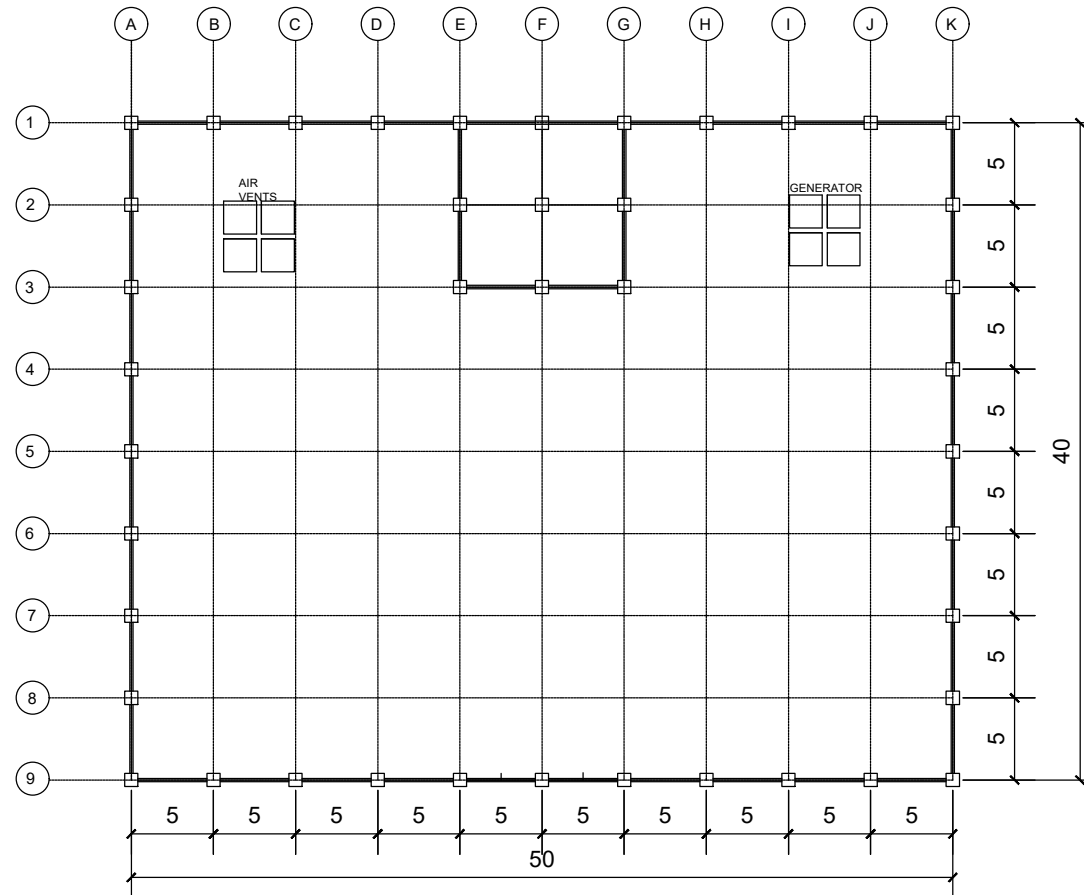

A-2
11

 ROOFDECK FLOOR PLAN
 SCALE NTS



PROJECT:	PREPARED BY:	OWNER:	SHEET:
PROPOSED 6-STOREY RESIDENTIAL BUILDING	<u>IAIN MATTHEW B. BARRUGA</u> ENGINEER	ENGR. ARBIE MARIZ A. PADILLA	A-2 11
LOCATION:	BSCE IV-A		
51-A NANGALISAN,2900 LAOAG CITY, ILOCOS NORTE	21-050060	ARCHITECTURAL DRAWINGS	



A-3
12

FRONT ELEVATION

SCALE

NTS



PROJECT:

PROPOSED 6-STOREY
RESIDENTIAL BUILDING

LOCATION:

51-A NANGALISAN, 2900
LAOAG CITY, ILOCOS NORTE

PREPARED BY:

IAIN MATTHEW B. BARRUGA
ENGINEER

BSCE IV-A

21-050060

OWNER:


ENGR. ARBIE MARIZ A. PADILLA

ARCHITECTURAL DRAWINGS

SHEET:

A-3

12

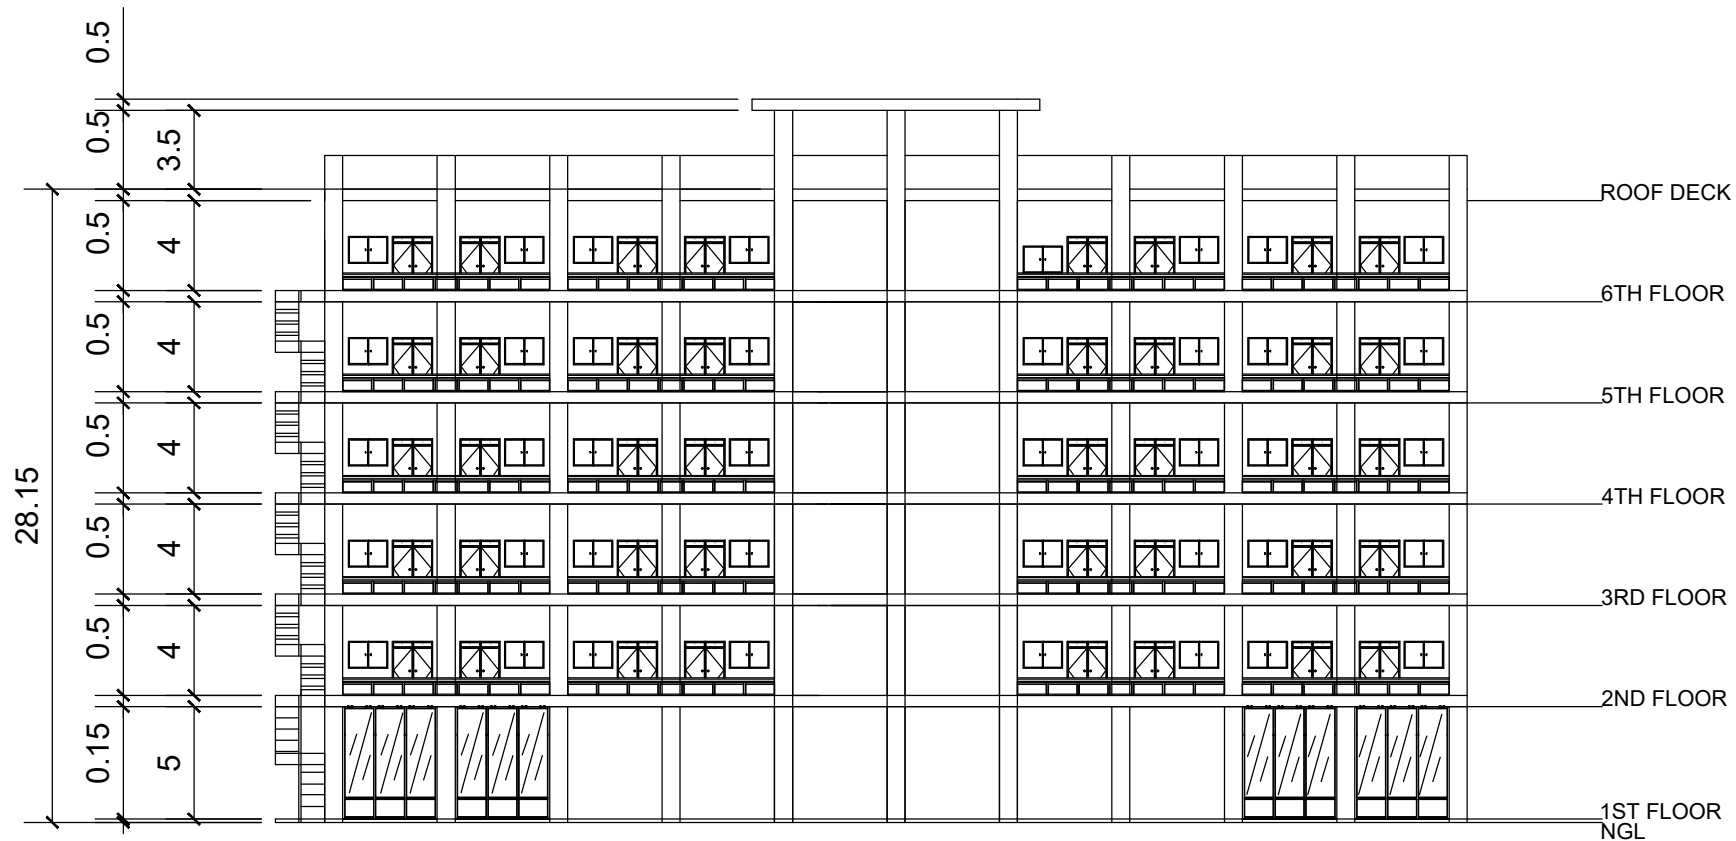

A-3
13

REAR ELEVATION

SCALE

NTS



PROJECT:

PROPOSED 6-STORY
RESIDENTIAL BUILDING

LOCATION:

51-A NANGALISAN, 2900
LAOAG CITY, ILOCOS NORTE

PREPARED BY:

IAIN MATTHEW B. BARRUGA
ENGINEER

BSCE IV-A

21-050060

OWNER:

ENGR. ARBIE MARIZ A. PADILLA

ARCHITECTURAL DRAWINGS

SHEET:

A-3


13



PROJECT:	PREPARED BY:	OWNER:	SHEET:
PROPOSED 6-STOREY RESIDENTIAL BUILDING	<u>IAIN MATTHEW B. BARRUGA</u> ENGINEER	ENGR. ARBIE MARIZ A. PADILLA	A-3 14
LOCATION:	BSCE IV-A		
51-A NANGALISAN,2900 LAOAG CITY, ILOCOS NORTE	21-050060	ARCHITECTURAL DRAWINGS	



PROJECT:	PREPARED BY:	OWNER:	SHEET:
PROPOSED 6-STOREY RESIDENTIAL BUILDING	<u>IAIN MATTHEW B. BARRUGA</u> ENGINEER	ENGR. ARBIE MARIZ A. PADILLA	A-3 15
LOCATION:	BSCE IV-A		
51-A NANGALISAN, 2900 LAOAG CITY, ILOCOS NORTE	21-050060	ARCHITECTURAL DRAWINGS	

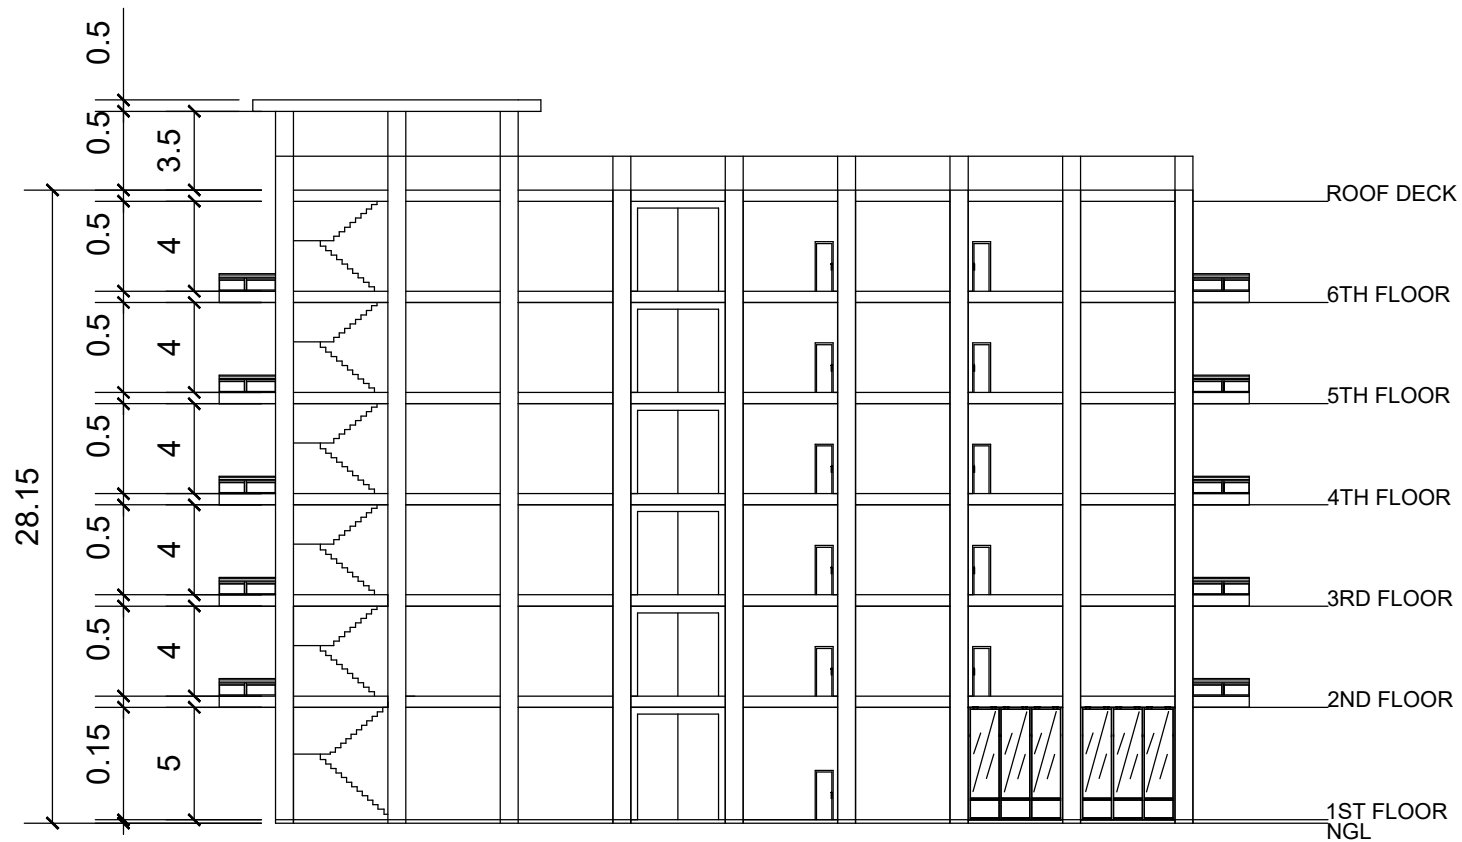

A-4
16

CROSS SECTION

SCALE

NTS



PROJECT:

PROPOSED 6-STORY
RESIDENTIAL BUILDING

LOCATION:

51-A NANGALISAN, 2900
LAOAG CITY, ILOCOS NORTE

PREPARED BY:

IAIN MATTHEW B. BARRUGA
ENGINEER

BSCE IV-A

21-050060

OWNER:


ENGR. ARBIE MARIZ A. PADILLA

ARCHITECTURAL DRAWINGS

SHEET:

A-4

16

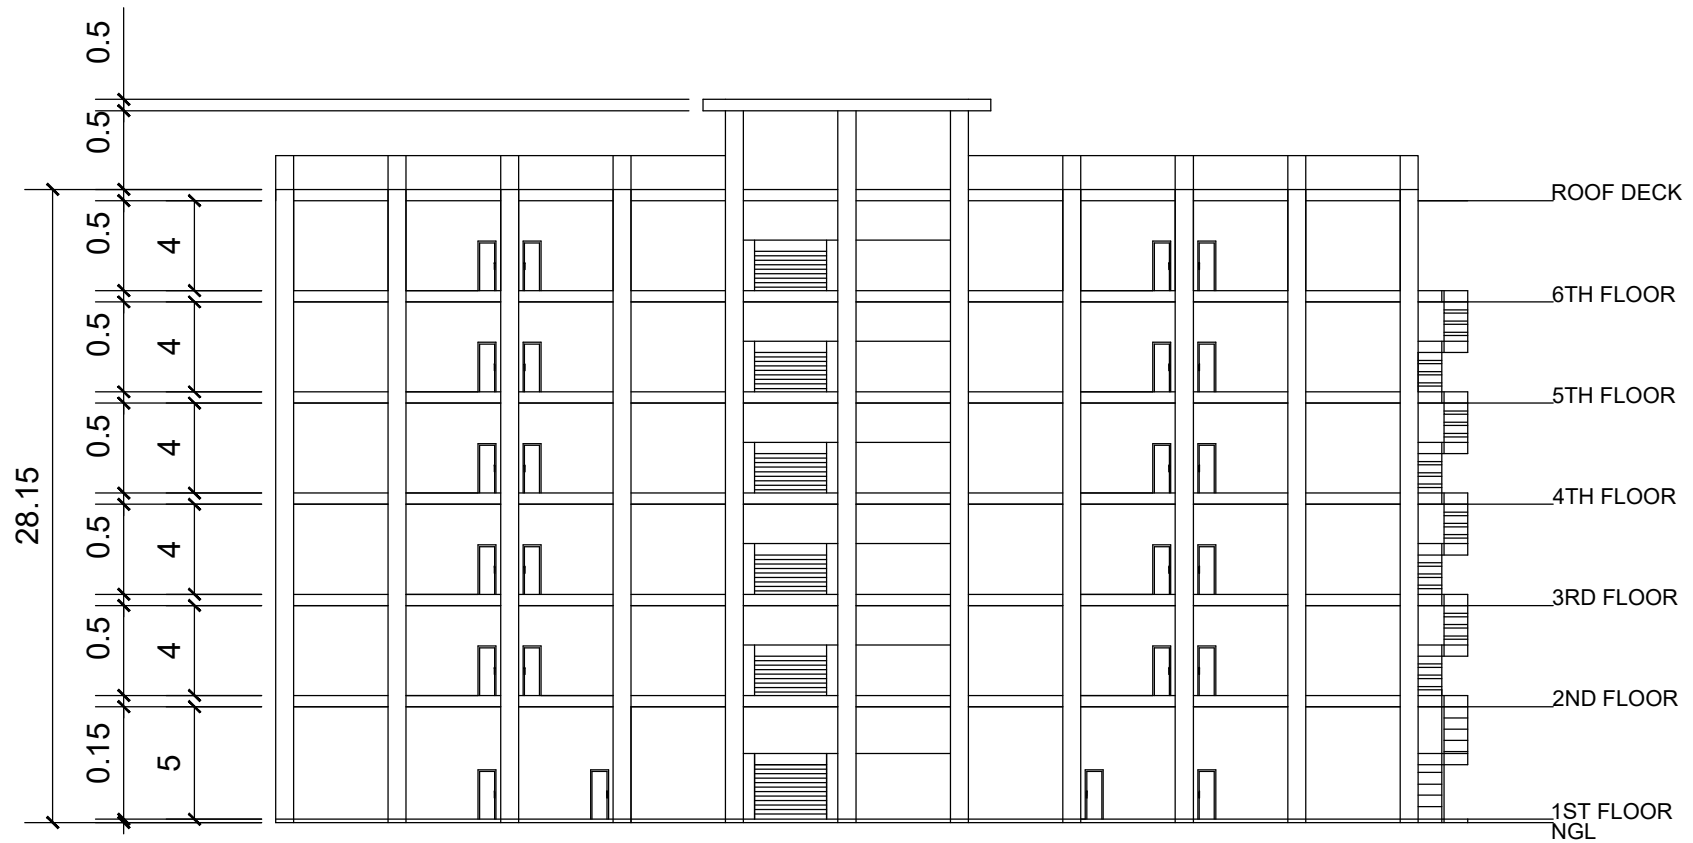

A-4
17

LONGITUDINAL CROSS SECTION

SCALE

NTS



PROJECT:

PROPOSED 6-STOREY
RESIDENTIAL BUILDING

LOCATION:

51-A NANGALISAN, 2900
LAOAG CITY, ILOCOS NORTE

PREPARED BY:

IAIN MATTHEW B. BARRUGA
ENGINEER

BSCE IV-A

21-050060

OWNER:


ENGR. ARBIE MARIZ A. PADILLA

ARCHITECTURAL DRAWINGS

SHEET:

A-4

17

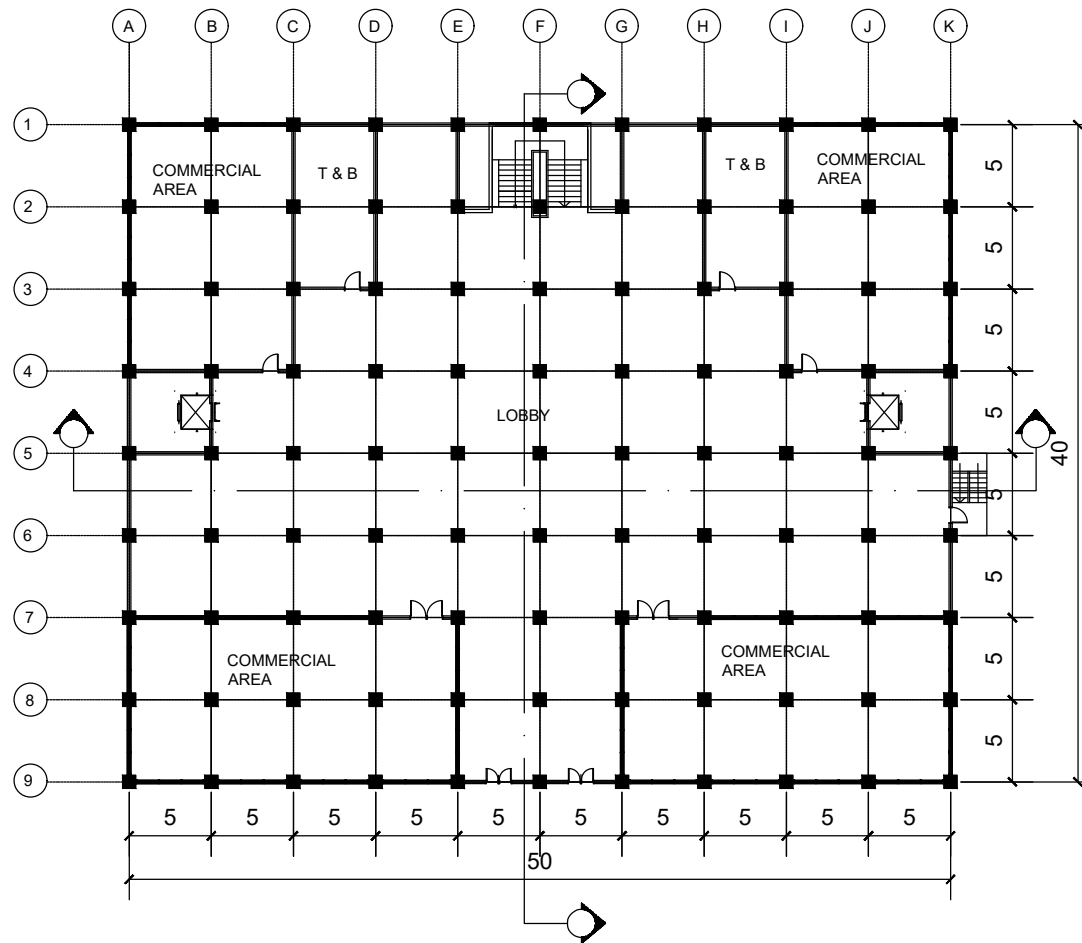

A-2
5

GROUND FLOOR PLAN

SCALE

NTS



PROJECT:

PROPOSED 6-STOREY
RESIDENTIAL BUILDING

LOCATION:

51-A NANGALISAN, 2900
LAOAG CITY, ILOCOS NORTE

PREPARED BY:

IAIN MATTHEW B. BARRUGA
ENGINEER

BSCE IV-A

21-050060

OWNER:

ENGR. ARBIE MARIZ A. PADILLA

ARCHITECTURAL DRAWINGS

SHEET:

A-2

5